

TENDER DRAWING LIST

PROJECT NAME	: HANA RESIDENCE, TROPICANA AMAN
CLIENT NAME	: MS SHEON & MR TEE
PROJECT CODE	: GS26-HANA
INTERIOR DESIGNER	: YANXIANG & YS
SALES PERSON	: RAYMOND
REVISION	: R0 - 1ST DRAFT 09 OCT 2026

DRAWING NO.	DESCRIPTION	REV.	REMARK
ID.00 COVER			
ID.00.01	TENDER DRAWING LIST	R0	
ID.00.02	MATERIAL LIST	R0	

ID.01 KEY DRAWING - PLANS			
ID.01.01	ORI. LAYOUT PLAN (GROUND FLOOR)	R0	
ID.01.02	ORI. LAYOUT PLAN (FIRST FLOOR)	R0	
ID.01.03	WET WORK & DEMOLISH PLAN (GROUND FLOOR)	R0	
ID.01.04	WET WORK & DEMOLISH PLAN (FIRST FLOOR)	R0	
ID.01.05	FURNITURE LAYOUT PLAN (GROUND FLOOR)	R0	
ID.01.06	FURNITURE LAYOUT PLAN (FIRST FLOOR)	R0	
ID.01.07	FURNITURE LAYOUT PLAN - DIMENSION (GROUND FLOOR)	R0	
ID.01.08	FURNITURE LAYOUT PLAN - DIMENSION (FIRST FLOOR)	R0	
ID.01.09	REFLECTED CEILING PLAN (GROUND FLOOR)	R0	
ID.01.10	REFLECTED CEILING PLAN (FIRST FLOOR)	R0	
ID.01.11	M&E PLAN - SOCKET (GROUND FLOOR)	R0	
ID.01.12	M&E PLAN - SOCKET (FIRST FLOOR)	R0	
ID.01.13	LIGHTING PLAN (GROUND FLOOR)	R0	
ID.01.14	LIGHTING PLAN (FIRST FLOOR)	R0	
ID.01.15	WALL FINISHES PLAN (GROUND FLOOR)	R0	
ID.01.16	WALL FINISHES PLAN (FIRST FLOOR)	R0	
ID.01.17	FLOOR FINISHES PLAN (GROUND FLOOR)	R0	
ID.01.18	FLOOR FINISHES PLAN (FIRST FLOOR)	R0	
ID.01.19	CURTAIN PLAN (GROUND FLOOR)	R0	
ID.01.20	CURTAIN PLAN (FIRST FLOOR)	R0	
ID.01.21	ELEVATION CODE PLAN (GROUND FLOOR)	R0	
ID.01.22	ELEVATION CODE PLAN (FIRST FLOOR)	R0	

DRAWING NO.	DESCRIPTION	REV.	REMARK
-------------	-------------	------	--------

ID.02 JOINERY - GROUND FLOOR			
ID.02.01	CF01 - ENTRANCE SHOE CABINET ELEVATION	R0	
ID.02.02	CF02 - FOYER ALTAR & STORAGE WALL ELEVATION	R0	
ID.02.03	CF03 - LIVING TV FEATURE WALL ELEVATION	R0	
ID.02.04	CF04 - LOUNGE FRONT WALL STORAGE & KEY CONSOLE ELEVATION	R0	
ID.02.05	CF05 - DRY KITCHEN DRINK COUNTER & STORAGE WALL ELEVATION	R0	
ID.02.06	CF06 - DRY KITCHEN ISLAND ELEVATION	R0	
ID.02.07	CF07 - WET KITCHEN HOB WALL BASE & WALL CABINET ELEVATION	R0	
ID.02.08	CF08 - WET KITCHEN SINK WALL BASE CABINET ELEVATION	R0	
ID.02.09	CF09 - WET KITCHEN TALL UNIT / OVEN / FRIDGE ELEVATION	R0	
ID.02.10	CF10 - WET KITCHEN FOOD PREPARATION ISLAND ELEVATION	R0	
ID.02.11	CF11 - LAUNDRY AREA WASHER & BASE UNIT ELEVATION	R0	
ID.02.12	CF12 - PARENT'S ROOM OPEN WARDROBE ELEVATION	R0	
ID.02.13	CF13 - MAID ROOM STORAGE CABINET & TATAMI ELEVATION	R0	
ID.02.14	CF14 - POWDER ROOM VANITY ELEVATION	R0	

ID.03 JOINERY - FIRST FLOOR			
ID.03.01	CF15 - MASTER BEDROOM HEADBOARD & BEDSIDE ELEVATION	R0	
ID.03.02	CF16 - MASTER BEDROOM TV DIVIDER W/ FIREPLACE ELEVATION	R0	
ID.03.03	CF17 - WALK IN CLOSET WARDROBE (GLASS DOOR) ELEVATION	R0	
ID.03.04	CF18 - MASTER BATH DOUBLE VANITY ELEVATION	R0	
ID.03.05	CF19 - FAMILY AREA FEATURE WALL / PIANO WALL ELEVATION	R0	
ID.03.06	CF20 - SON'S ROOM WARDROBE & DISPLAY ELEVATION	R0	
ID.03.07	CF21 - DAUGHTER'S ROOM WARDROBE & DISPLAY ELEVATION	R0	
ID.03.08	CF22 - SON'S / DAUGHTER'S BATH VANITY ELEVATION	R0	

TENDER DRAWING LIST



COVER

ID
00

PROJECT TYPE :		DESIGN & BUILD		DRAWING TITLE :		TENDER DRAWING LIST		DRAWING'S STATUS :		ALL DRAWINGS ARE COPY-RIGHT OF: GROO SPACE SDN BHD (1662567-V) LEVEL 3A, WISMA JAG, JALAN DESA UTAMA, TAMAN DESA, 58100 KUALA LUMPUR T: +6016-913 6785 / +6012-528 7212 E: groospacemy@gmail.com IG: @groospace.my groospace		CLIENTS ACKNOWLEDGE & SIGN :			
PROJECT :		HANA RESIDENCE, TROPICANA AMAN		INTERIOR DESIGNER : YANXIANG & YS		SALE PERSON : RAYMOND		1ST DRAFT (R0)						09 OCT' 26	
								AMENDMENT 01							
								AMENDMENT 02							
CLIENT :		MS SHEON & MR TEE		CHECK BY :		RAYMOND		ID.00.01						AMENDMENT 03	
										AMENDMENT 04					

"NOTICE TO CONTRACTOR: DO NOT SCALE DRAWINGS. All dimensions and site levels must be Verified In Field (V.I.F.) before any fabrication or commencement of work. Any discrepancies between these drawings and actual site conditions must be reported to the Designer immediately for clarification. Failure to do so will be at the Contractor's own risk."


HANA RESIDENCE MATERIAL LIST (SUPPLY & INSTALL BY GROO SPACE)

  MELAMINE				
CODE	BRAND	REF	DESCRIPTION	AREA
M01	PANEL PLUS		69A OAK MELAMINE 16MM	WHOLE AREA - CARCASS FRONT
M02	TOP MIX		M1-1002DM COTTON WHITE MELAMINE 16MM	FOYER / LIVING / DRY KITCHEN
M03	PANEL PLUS		BX6 SUPER BLACK MELAMINE 16MM	SON'S ROOM / LAUNDRY
M04	-		INNER CARCASS WHITE MELAMINE 16MM	ALL INNER CARCASS
M05	PANEL PLUS		DARK OAK (TBC) MELAMINE 16MM	ENTRANCE / LAUNDRY / MAID

STONE				
CODE	BRAND	REF	DESCRIPTION	AREA
S01	TBC		SINTERED STONE 12MM SINTERED	KITCHEN / VANITY TOPS

FLOORING				
CODE	BRAND	REF	DESCRIPTION	AREA
W01	PORTER		ROSEWOOD ENGINEERED WOOD 15-20MM	PARENT'S ROOM / FIRST FLOOR

LAMINATE				
CODE	BRAND	REF	DESCRIPTION	AREA
L01	PANEL PLUS		PL0242 BW OAK PLYWOOD + LAMINATE	DRY KITCHEN / MASTER / M.BATH
L02	TOPMIX		TS4-1017 M BLACK PLYWOOD + LAMINATE	SON'S ROOM / LAUNDRY
L03	TOPMIX		TS8-1251 VM IVORY WHITE PLYWOOD + LAMINATE	LIVING / FOYER

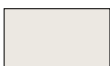TILES				
CODE	BRAND	REF	DESCRIPTION	AREA
T01	DONG PENG		LING HUA BAI 900x1800 SINTERED STONE	LIVING / DINING / KITCHEN FLOOR
T02	BELLEZZA		X-OLIVETTI X01 BLANCO 600x1200 PORCELAIN	FOYER / ENTRANCE / LAUNDRY
T03	DONG PENG		750x1500 (TBC) PORCELAIN	FF BATHROOMS
T04	DONG PENG		AMAZON TRAVERTINE 600x1200 MATT PORCELAIN	POWDER / PARENT'S BATH
T05	DONG PENG		LIMESTONE JH12352GZ 600x1200 STRUCTURED	WET KITCHEN / LAUNDRY WALL

PAINT				
CODE	BRAND	REF	DESCRIPTION	AREA
P01	JOTUN		TBC (WARM WHITE) EMULSION MATT	WHOLE UNIT
P02	SUZUKA		TBC (LIMEWASH) TEXTURE	MASTER / DAUGHTER FEATURE WALL
P03	JOTUN		TBC (WARM GREY) EMULSION MATT	SON'S ROOM

ALL MATERIAL CODES TBC UPON CLIENT CONFIRMATION OF PHYSICAL SAMPLES.

MATERIAL LIST

COVER

D
00


PROJECT TYPE :		DESIGN & BUILD		DRAWING TITLE :		MATERIAL LIST		DRAWING'S STATUS :		ALL DRAWINGS ARE COPY-RIGHT OF: GROO SPACE SDN BHD (1662567-V) LEVEL 3A, WISMA JAG, JALAN DESA UTAMA, TAMAN DESA, 58100 KUALA LUMPUR T: +6016-913 6785 / +6012-528 7212 E: groospacemy@gmail.com IG: @groospace.my groospace	CLIENTS ACKNOWLEDGE & SIGN :
PROJECT :		HANA RESIDENCE, TROPICANA AMAN		INTERIOR DESIGNER : YANXIANG & YS		SALE PERSON : RAYMOND		1ST DRAFT (R0)	09 OCT' 26		
								AMENDMENT 01			
								AMENDMENT 02			
								AMENDMENT 03			
CLIENT :		MS SHEON & MR TEE		CHECK BY : RAYMOND		ID.00.02		AMENDMENT 04			

"NOTICE TO CONTRACTOR: DO NOT SCALE DRAWINGS. All dimensions and site levels must be Verified In Field (V.I.F.) before any fabrication or commencement of work. Any discrepancies between these drawings and actual site conditions must be reported to the Designer immediately for clarification. Failure to do so will be at the Contractor's own risk."



ID
01

"NOTICE TO CONTRACTOR: DO NOT SCALE DRAWINGS. All dimensions and site levels must be Verified In Field (V.I.F.) before any fabrication or commencement of work. Any discrepancies between these drawings and actual site conditions must be reported to the Designer immediately for clarification. Failure to do so will be at the Contractor's own risk."

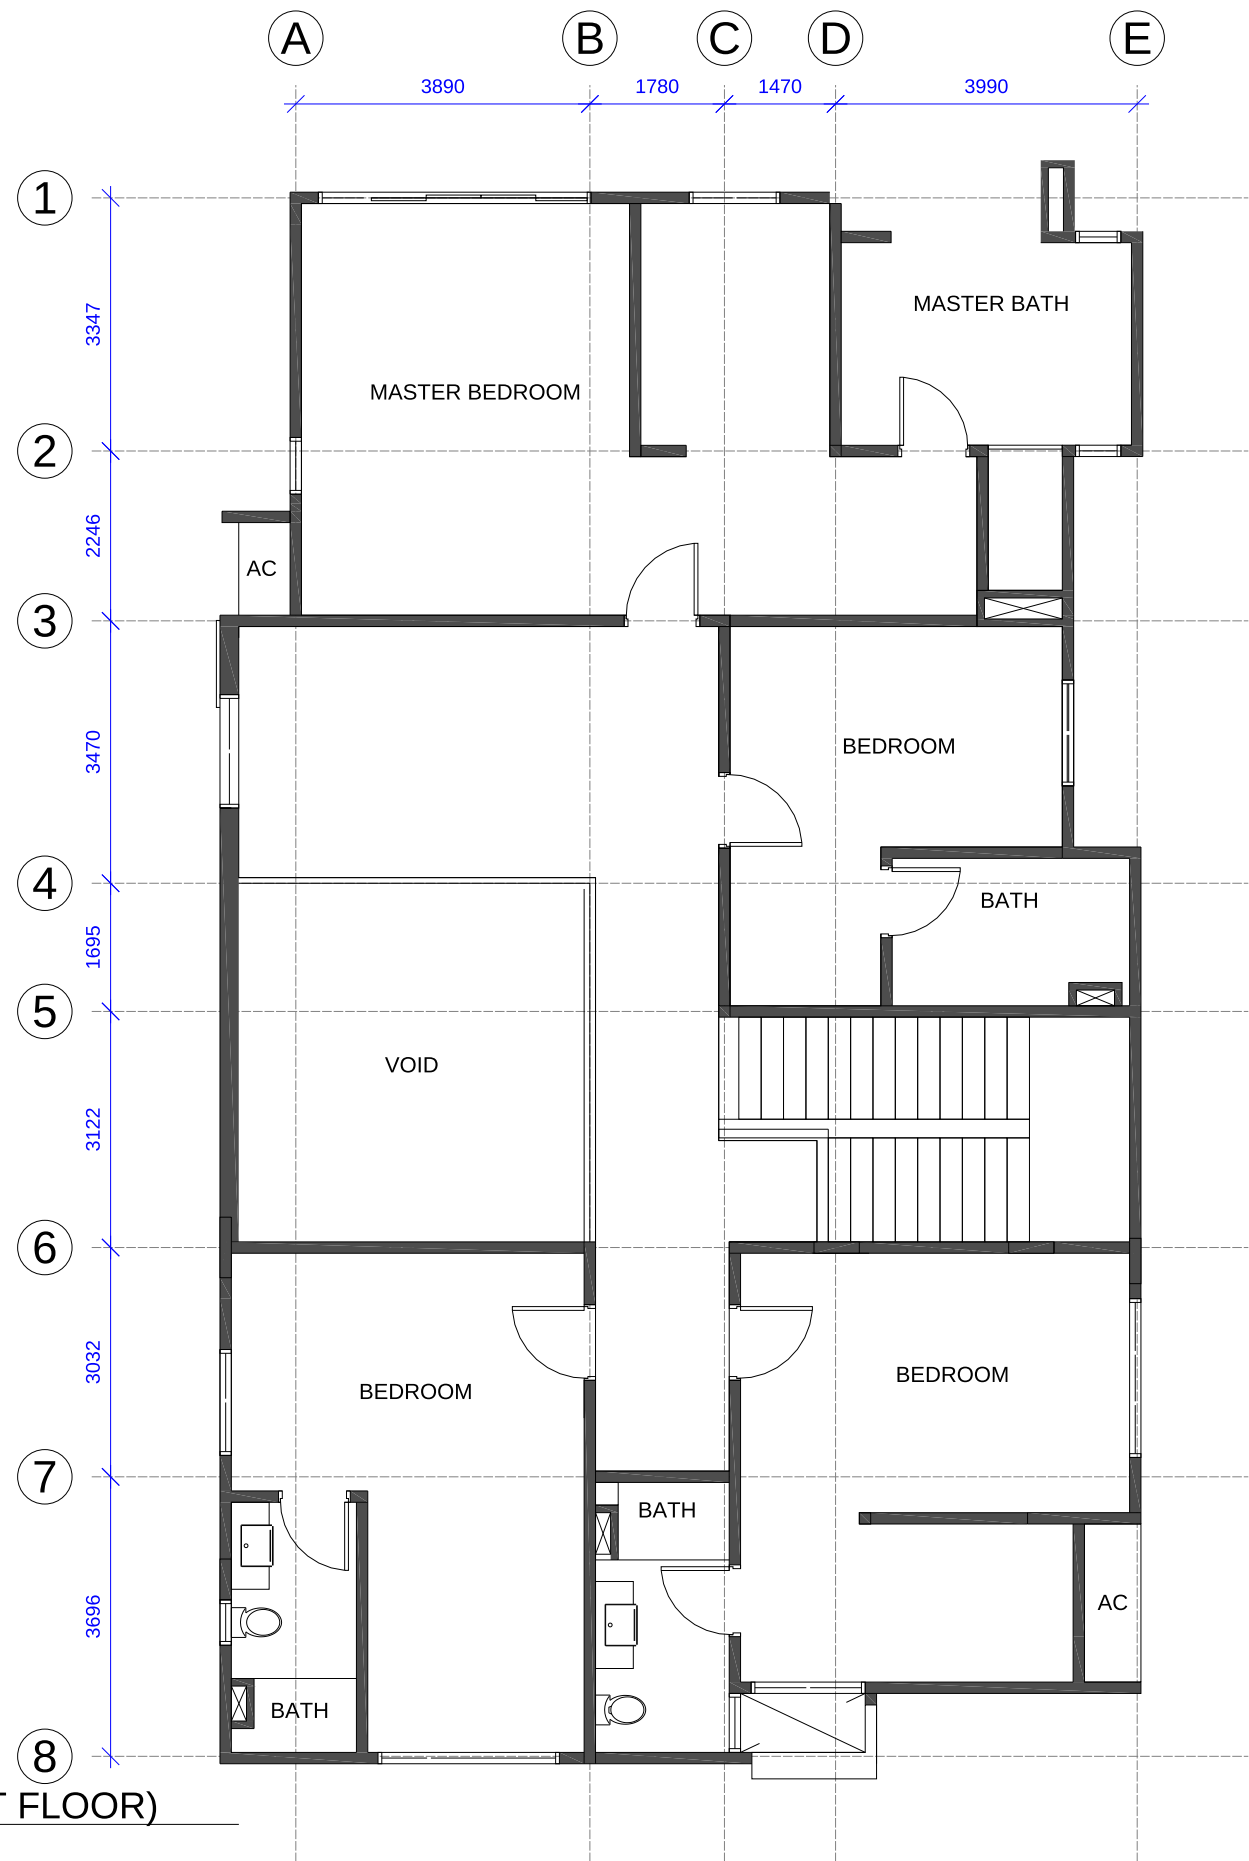


ID 01
ORI. LAYOUT PLAN (FIRST FLOOR)
SCALE 1:100

ORI. LAYOUT PLAN
FIRST FLOOR ID 02

PROJECT TYPE :		DESIGN & BUILD		DRAWING TITLE :		ORI. LAYOUT PLAN (FIRST FLOOR)		DRAWING'S STATUS :		ALL DRAWINGS ARE COPY-RIGHT OF: GROO SPACE SDN BHD (1662567-V) LEVEL 3A, WISMA JAG, JALAN DESA UTAMA, TAMAN DESA, 58100 KUALA LUMPUR T: +6016-913 6785 / +6012-528 7212 E: groospacemy@gmail.com IG: @groospace.my groospace	CLIENTS ACKNOWLEDGE & SIGN :
PROJECT :		HANA RESIDENCE, TROPICANA AMAN		INTERIOR DESIGNER : YANXIANG & YS		SALE PERSON : RAYMOND		1ST DRAFT (R0)	09 OCT' 26		
CLIENT :		MS SHEON & MR TEE		CHECK BY : RAYMOND		ID.01.02		AMENDMENT 01			
								AMENDMENT 02			
								AMENDMENT 03			
								AMENDMENT 04			

"NOTICE TO CONTRACTOR: DO NOT SCALE DRAWINGS. All dimensions and site levels must be Verified In Field (V.I.F.) before any fabrication or commencement of work. Any discrepancies between these drawings and actual site conditions must be reported to the Designer immediately for clarification. Failure to do so will be at the Contractor's own risk."

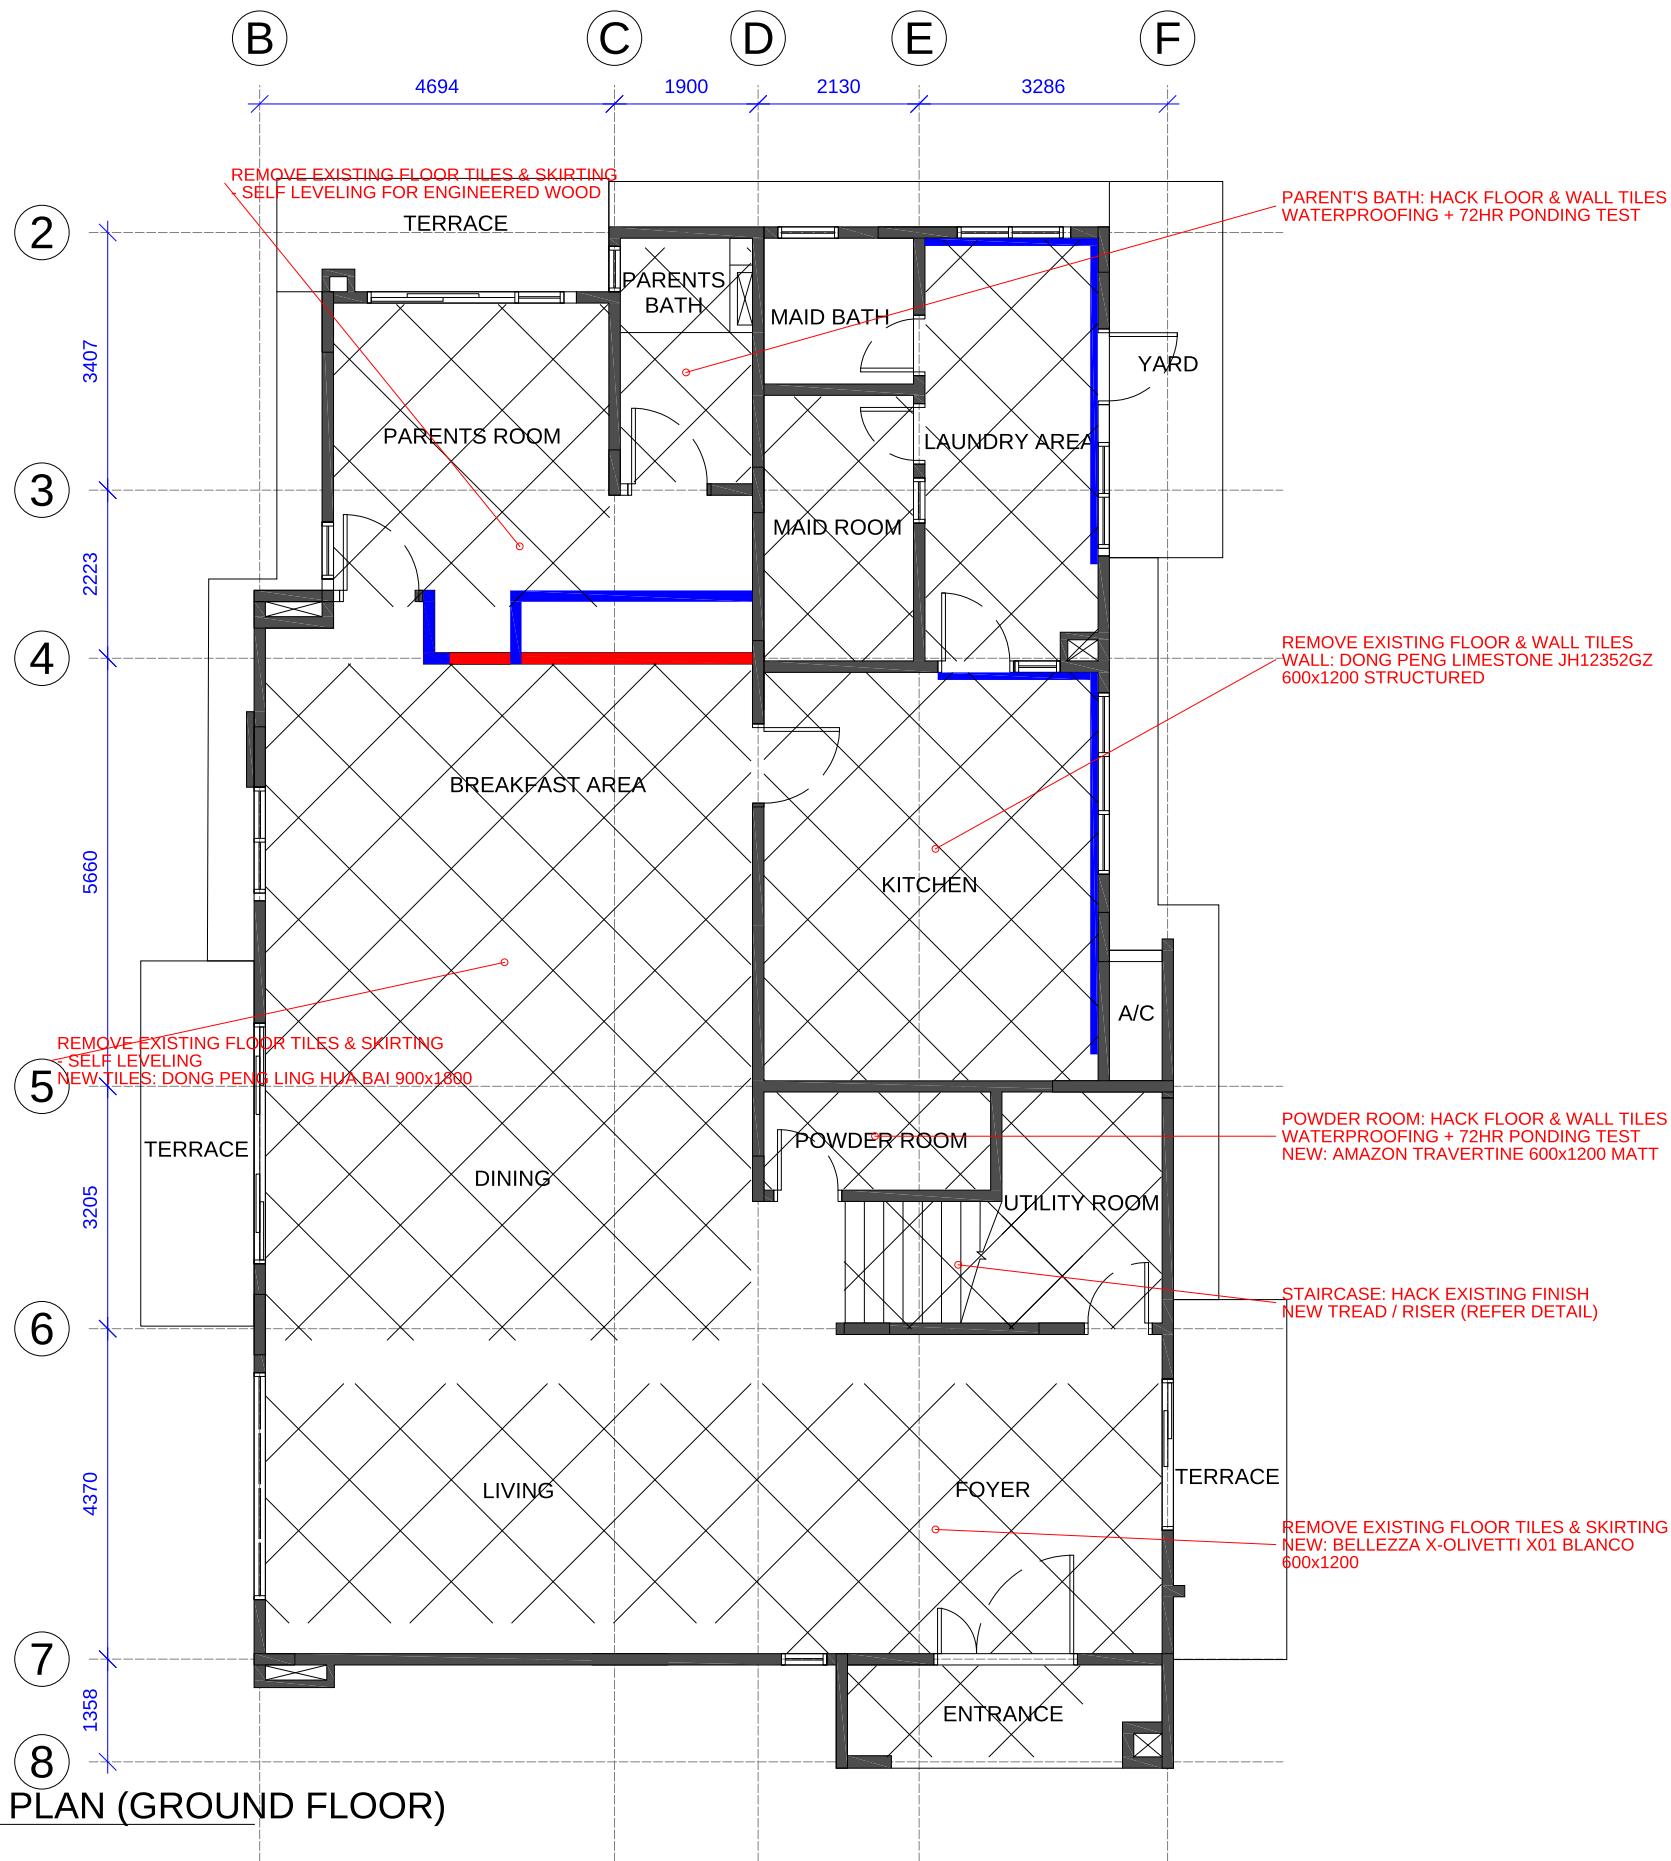

LEGEND (DEMOLISH):

	EXISTING WALL
	WALL TO BE HACKED
	NEW WALL (BRICK / BOARD)
	EXISTING FLOOR TILES TO BE HACKED / REMOVED

WET WORK & DEMOLISH PLAN (GROUND FLOOR)
SCALE 1:100

WET WORK & DEMOLISH PLAN
GROUND FLOOR

PROJECT TYPE :	DESIGN & BUILD	DRAWING TITLE :	WET WORK & DEMOLISH PLAN (GROUND FLOOR)		DRAWING'S STATUS :	09 OCT' 26		ALL DRAWINGS ARE COPY-RIGHT OF:	CLIENTS ACKNOWLEDGE & SIGN :
PROJECT :	HANA RESIDENCE, TROPICANA AMAN	INTERIOR DESIGNER :	YANXIANG & YS	SALE PERSON :	RAYMOND	1ST DRAFT (R0)			GROO SPACE SDN BHD (1662567-V) LEVEL 3A, WISMA JAG, JALAN DESA UTAMA, TAMAN DESA, 58100 KUALA LUMPUR T: +6016-913 6785 / +6012-528 7212 E: groospacemy@gmail.com IG: @groospace.my
CLIENT :	MS SHEON & MR TEE	CHECK BY :	RAYMOND	ID.01.03	AMENDMENT 01				
					AMENDMENT 02				
					AMENDMENT 03				
					AMENDMENT 04				

"NOTICE TO CONTRACTOR: DO NOT SCALE DRAWINGS. All dimensions and site levels must be Verified In Field (V.I.F.) before any fabrication or commencement of work. Any discrepancies between these drawings and actual site conditions must be reported to the Designer immediately for clarification. Failure to do so will be at the Contractor's own risk."



	EXISTING WALL
	WALL TO BE HACKED
	NEW WALL (BRICK / BOARD)
	EXISTING FLOOR TILES TO BE HACKED / REMOVED

ID
01

DAUGHTER'S BATH: HACK FLOOR & WALL TILES (TBC)

SCALE 1:100

D
4

FIRST FLOOR (0


PROJECT TYPE :		DESIGN & BUILD		DRAWING TITLE :			WET WORK & DEMOLISH PLAN (FIRST FLOOR)			DRAWING'S STATUS :			ALL DRAWINGS ARE COPY-RIGHT OF: GROO SPACE SDN BHD (1662567-V) LEVEL 3A, WISMA JAG, JALAN DESA UTAMA, TAMAN DESA, 58100 KUALA LUMPUR T: +6016-913 6785 / +6012-528 7212 E: groospacemy@gmail.com IG: @groospace.my			CLIENTS ACKNOWLEDGE & SIGN :					
PROJECT :		HANA RESIDENCE, TROPICANA AMAN		INTERIOR DESIGNER :		YANXIANG & YS		SALE PERSON :		RAYMOND		1ST DRAFT (R0)							09 OCT' 26		
												AMENDMENT 01									
												AMENDMENT 02									
CLIENT :		MS SHEON & MR TEE		CHECK BY :		RAYMOND				ID.01.04		AMENDMENT 03									
												AMENDMENT 04									

"NOTICE TO CONTRACTOR: DO NOT SCALE DRAWINGS. All dimensions and site levels must be Verified In Field (V.I.F.) before any fabrication or commencement of work. Any discrepancies between these drawings and actual site conditions must be reported to the Designer immediately for clarification. Failure to do so will be at the Contractor's own risk."



PROJECT TYPE :		DESIGN & BUILD		DRAWING TITLE :		FURNITURE LAYOUT PLAN (GROUND FLOOR)		DRAWING'S STATUS :		ALL DRAWINGS ARE COPY-RIGHT OF: groo space GROO SPACE SDN BHD (1662567-V) LEVEL 3A, WISMA JAG, JALAN DESA UTAMA, TAMAN DESA, 58100 KUALA LUMPUR T: +6016-913 6785 / +6012-528 7212 E: groospacemy@gmail.com IG: @groospace.my		CLIENTS ACKNOWLEDGE & SIGN :			
PROJECT :		HANA RESIDENCE, TROPICANA AMAN		INTERIOR DESIGNER :		YANXIANG & YS		SALE PERSON :						RAYMOND	
CLIENT :		MS SHEON & MR TEE		CHECK BY :		RAYMOND		ID.01.05							

"NOTICE TO CONTRACTOR: DO NOT SCALE DRAWINGS. All dimensions and site levels must be Verified In Field (V.I.F.) before any fabrication or commencement of work. Any discrepancies between these drawings and actual site conditions must be reported to the Designer immediately for clarification. Failure to do so will be at the Contractor's own risk."

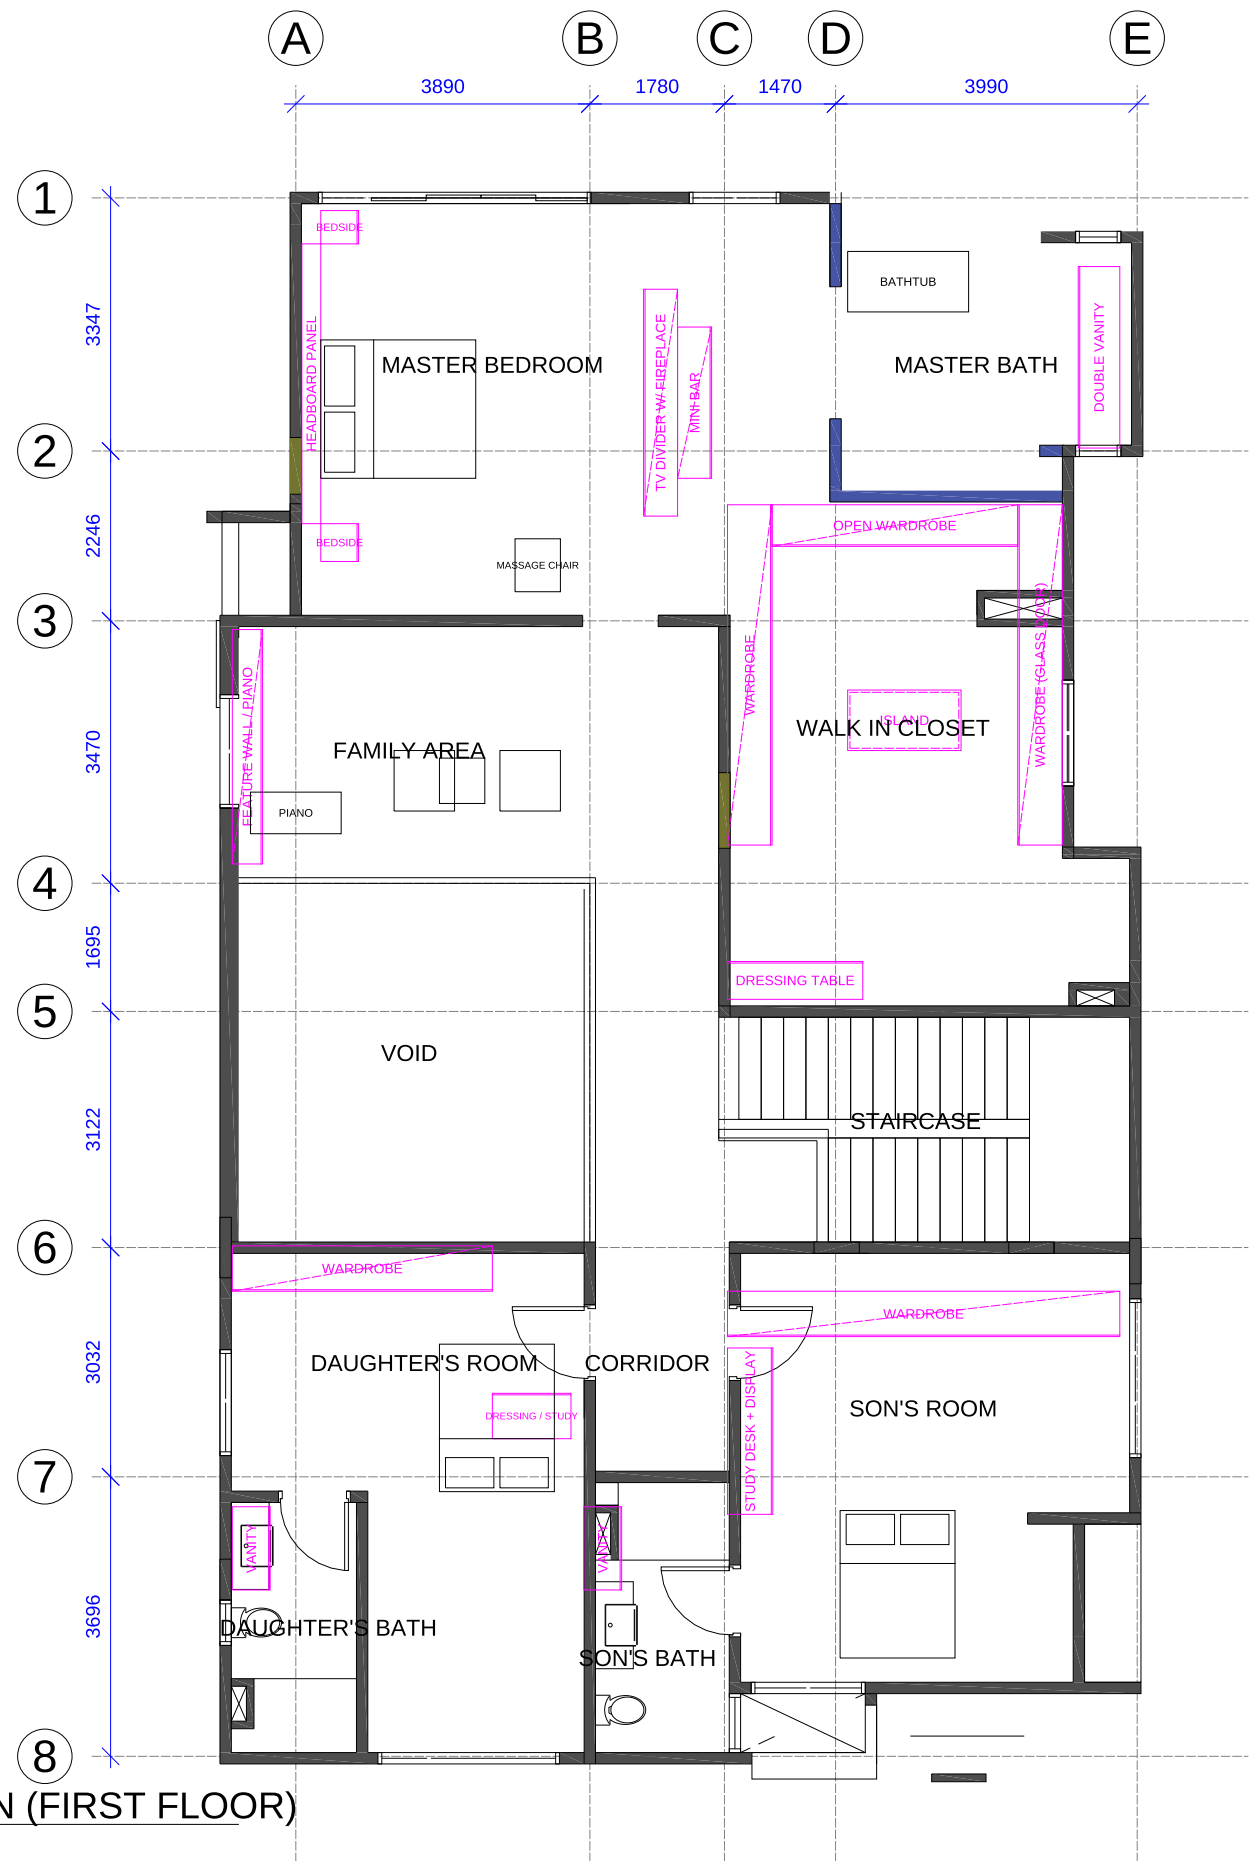


ID 01 FURNITURE LAYOUT PLAN (FIRST FLOOR)
SCALE 1:100

FURNITURE LAYOUT PLAN ID 06
FIRST FLOOR

PROJECT TYPE :	DESIGN & BUILD	DRAWING TITLE :	FURNITURE LAYOUT PLAN (FIRST FLOOR)	DRAWING'S STATUS :	1ST DRAFT (R0) 09 OCT' 26	ALL DRAWINGS ARE COPY-RIGHT OF:	CLIENTS ACKNOWLEDGE & SIGN :
PROJECT :	HANA RESIDENCE, TROPICANA AMAN	INTERIOR DESIGNER :	YANXIANG & YS	SALE PERSON :	RAYMOND	GROO SPACE SDN BHD (1662567-V)	
CLIENT :	MS SHEON & MR TEE	CHECK BY :	RAYMOND	ID.01.06		LEVEL 3A, WISMA JAG, JALAN DESA UTAMA, TAMAN DESA, 58100 KUALA LUMPUR	
						T: +6016-913 6785 / +6012-528 7212	
						E: groospacemy@gmail.com IG: @groospace.my	

"NOTICE TO CONTRACTOR: DO NOT SCALE DRAWINGS. All dimensions and site levels must be Verified In Field (V.I.F.) before any fabrication or commencement of work. Any discrepancies between these drawings and actual site conditions must be reported to the Designer immediately for clarification. Failure to do so will be at the Contractor's own risk."

ROOM CLEAR DIMENSIONS ARE FROM WALL FINISH TO WALL FINISH. JOINERY SIZES TO BE V.I.F. AFTER PLASTERING & TILING.

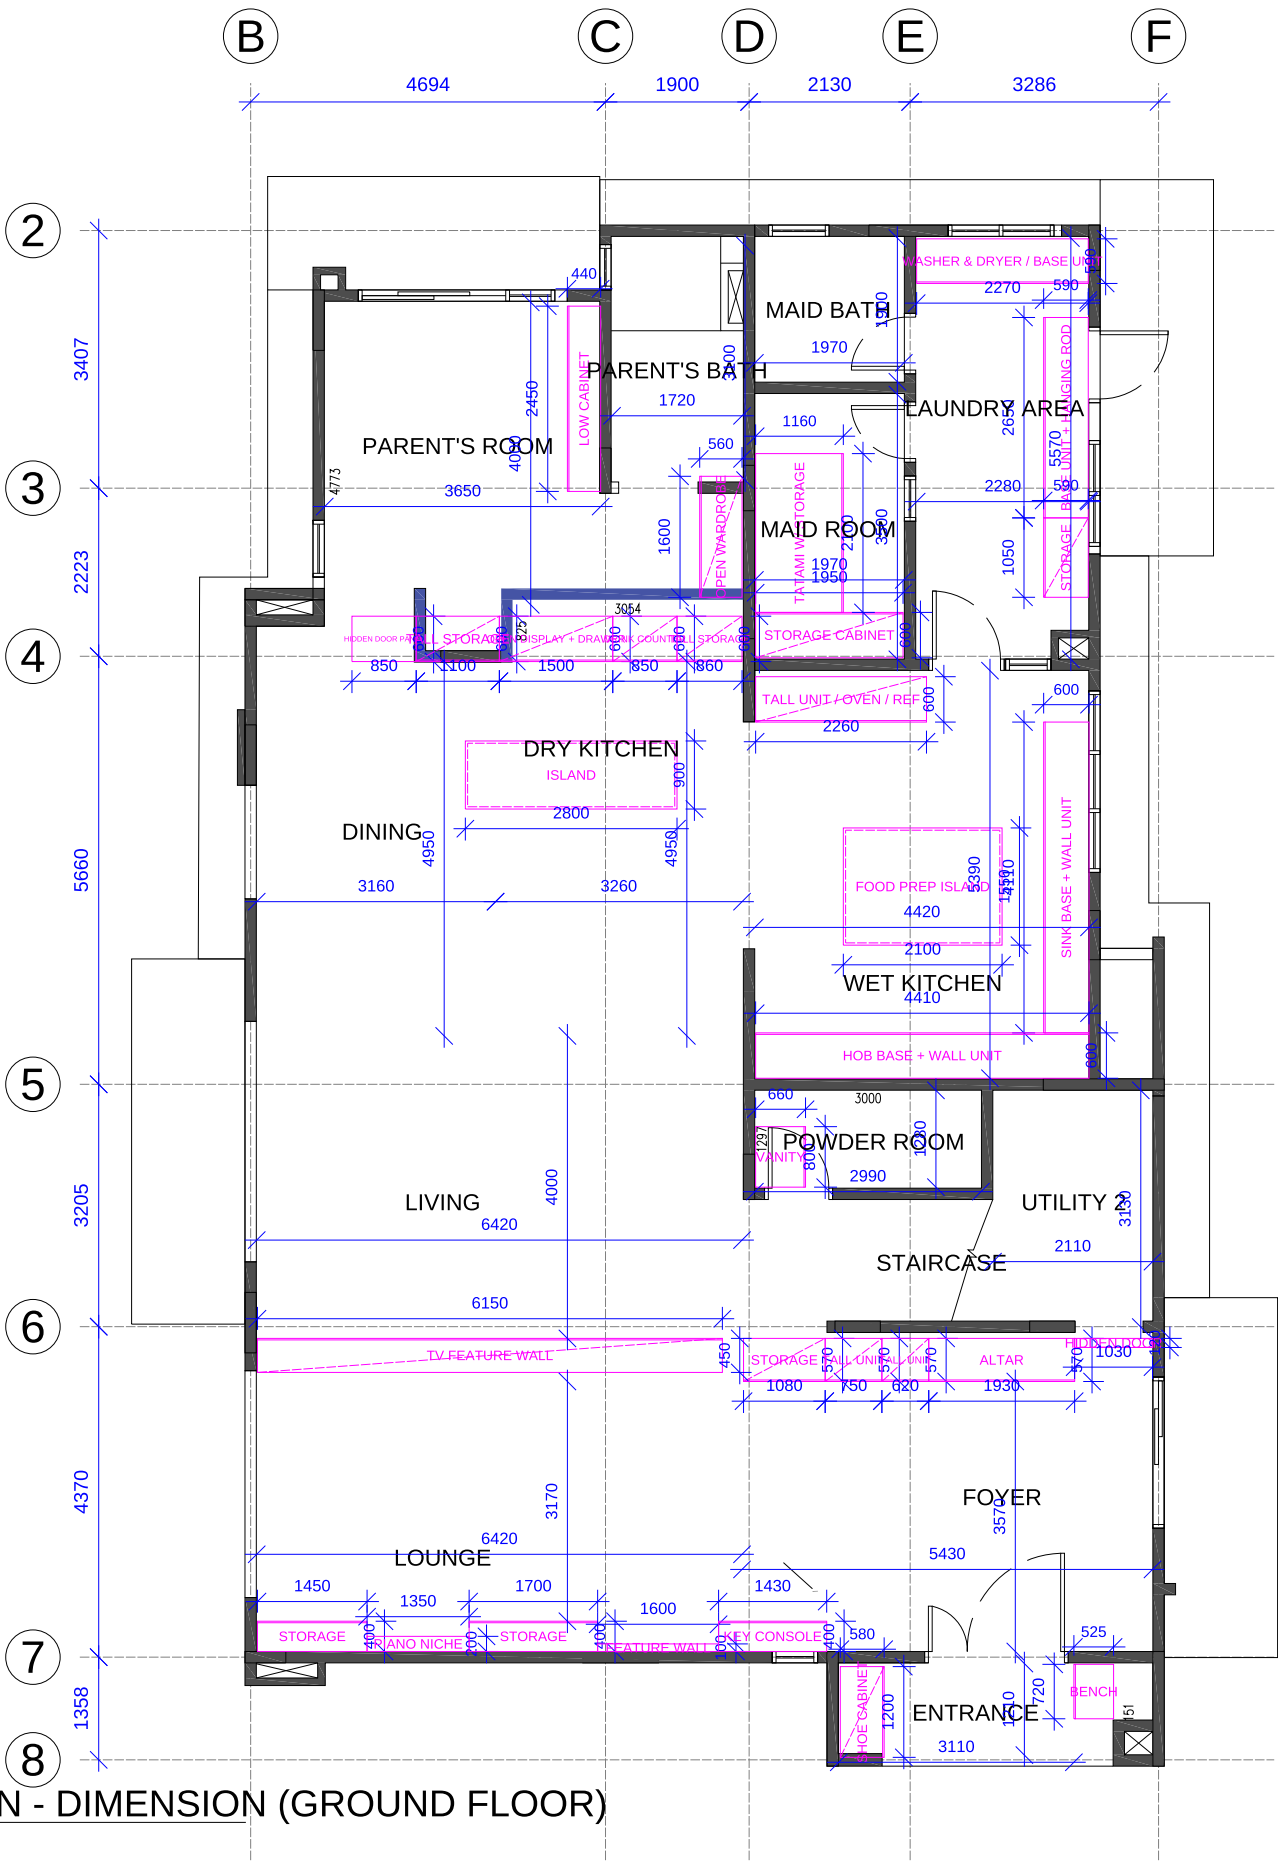


ID 01 FURNITURE LAYOUT PLAN - DIMENSION (GROUND FLOOR)
SCALE 1:100

FURNITURE LAYOUT PLAN - DIMENSION ID 07
GROUND FLOOR

PROJECT TYPE :	DESIGN & BUILD	DRAWING TITLE :	FURNITURE LAYOUT PLAN - DIMENSION (GROUND FLOOR)		DRAWING'S STATUS :		ALL DRAWINGS ARE COPY-RIGHT OF: GROO SPACE SDN BHD (1662567-V) LEVEL 3A, WISMA JAG, JALAN DESA UTAMA, TAMAN DESA, 58100 KUALA LUMPUR T: +6016-913 6785 / +6012-528 7212 E: groospacemy@gmail.com IG: @groospace.my	CLIENTS ACKNOWLEDGE & SIGN :
PROJECT :	HANA RESIDENCE, TROPICANA AMAN	INTERIOR DESIGNER :	YANXIANG & YS	SALE PERSON :	RAYMOND	1ST DRAFT (R0)	09 OCT' 26	
CLIENT :	MS SHEON & MR TEE	CHECK BY :	RAYMOND	ID.01.07		AMENDMENT 01		
						AMENDMENT 02		
						AMENDMENT 03		
						AMENDMENT 04		

"NOTICE TO CONTRACTOR: DO NOT SCALE DRAWINGS. All dimensions and site levels must be Verified In Field (V.I.F.) before any fabrication or commencement of work. Any discrepancies between these drawings and actual site conditions must be reported to the Designer immediately for clarification. Failure to do so will be at the Contractor's own risk."

ROOM CLEAR DIMENSIONS ARE FROM WALL FINISH TO WALL FINISH.JOINERY SIZES TO BE V.I.F. AFTER PLASTERING & TILING.

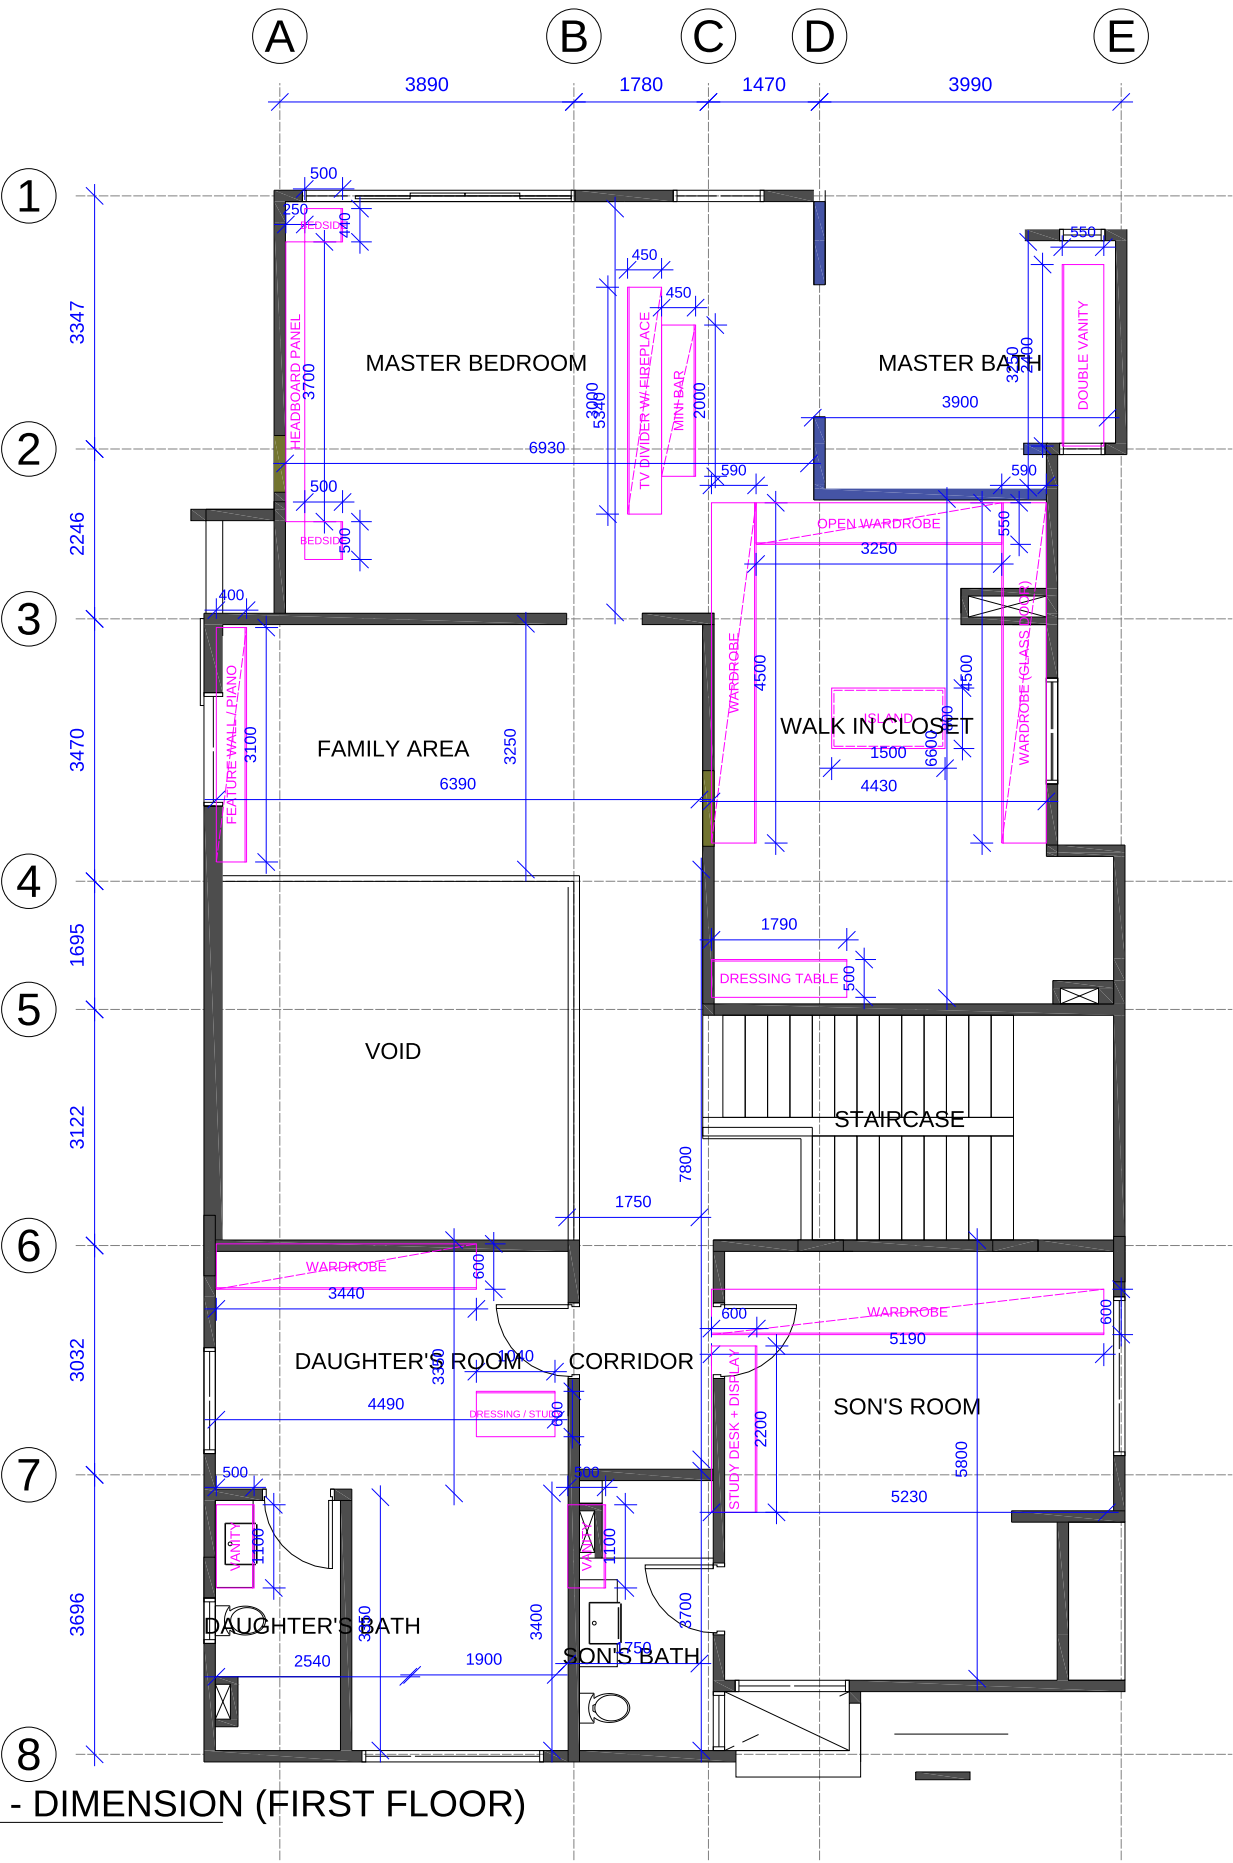

ID 01 FURNITURE LAYOUT PLAN - DIMENSION (FIRST FLOOR) SCALE 1:100

FURNITURE LAYOUT PLAN - DIMENSION FIRST FLOOR ID 08

PROJECT TYPE :	DESIGN & BUILD	DRAWING TITLE :	FURNITURE LAYOUT PLAN - DIMENSION (FIRST FLOOR)	DRAWING'S STATUS :	1ST DRAFT (R0) 09 OCT' 26	ALL DRAWINGS ARE COPY-RIGHT OF:	CLIENTS ACKNOWLEDGE & SIGN :
PROJECT :	HANA RESIDENCE, TROPICANA AMAN	INTERIOR DESIGNER :	YANXIANG & YS	SALE PERSON :	RAYMOND	GROO SPACE SDN BHD (1662567-V)	
CLIENT :	MS SHEON & MR TEE	CHECK BY :	RAYMOND	ID.01.08		LEVEL 3A, WISMA JAG, JALAN DESA UTAMA, TAMAN DESA, 58100 KUALA LUMPUR	
						T: +6016-913 6785 / +6012-528 7212	
						E: groospacemy@gmail.com IG: @groospace.my	

"NOTICE TO CONTRACTOR: DO NOT SCALE DRAWINGS. All dimensions and site levels must be Verified In Field (V.I.F.) before any fabrication or commencement of work. Any discrepancies between these drawings and actual site conditions must be reported to the Designer immediately for clarification. Failure to do so will be at the Contractor's own risk."




ALL CEILING LEVELS ARE DESIGN LEVELS (TBC).
SITE SOFFIT HEIGHTS PER SITE MEASURE: FOYER S3814, LIVING
SH4207, BREAKFAST SH4273, DINING SH8118 (VOID), WET KITCHEN
CH3539, ENTRANCE CH3334.

ALL DRAWINGS ARE COPY-RIGHT OF:

GROO SPACE SDN BHD (1662567-V)
LEVEL 3A, WISMA JAG, JALAN DESA UTAMA,
TAMAN DESA, 58100 KUALA LUMPUR
T: +6016-913 6785 / +6012-528 7212
E: groospacemy@gmail.com IG: @groospace.my

PROJECT TYPE :		DESIGN & BUILD		DRAWING TITLE :		REFLECTED CEILING PLAN (GROUND FLOOR)		DRAWING'S STATUS :			
PROJECT :		HANA RESIDENCE, TROPICANA AMAN		INTERIOR DESIGNER : YANXIANG & YS		SALE PERSON : RAYMOND		1ST DRAFT (R0)		09 OCT' 26	
								AMENDMENT 01			
								AMENDMENT 02			
CLIENT :		MS SHEON & MR TEE		CHECK BY : RAYMOND		ID.01.09		AMENDMENT 03			
								AMENDMENT 04			

NOTICE TO CONTRACTOR: DO NOT SCALE DRAWINGS. All dimensions and site levels must be Verified In Field (V.I.F.) before any fabrication or commencement of work. Any discrepancies between these drawings and actual site conditions must be reported to the Designer immediately for clarification. Failure to do so will be at the Contractor's own risk.

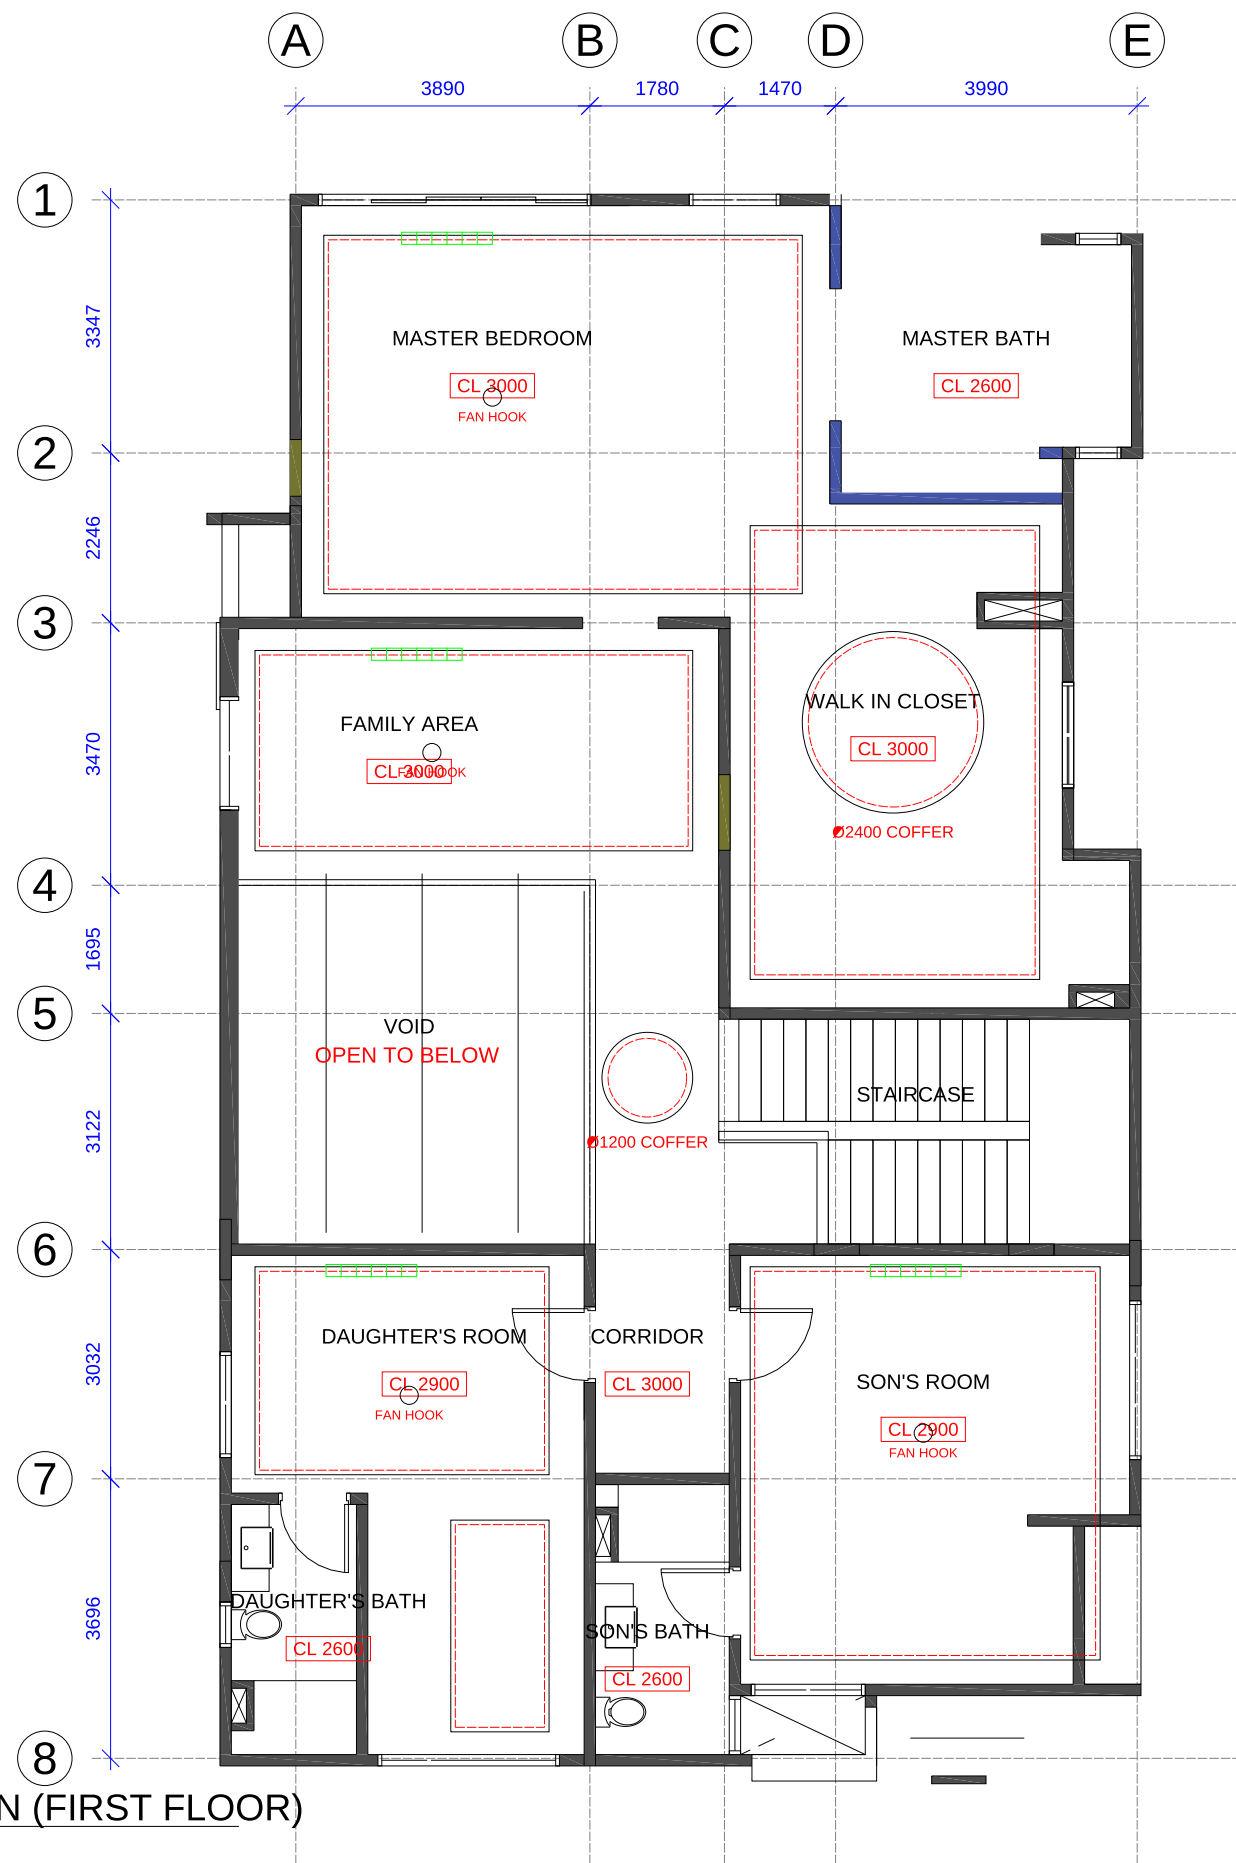


REFLECTED CEILING PLAN (FIRST FLOOR)

REFLECTED CEILING PLAN

FIRST FLOOR

PROJECT TYPE :	DESIGN & BUILD	DRAWING TITLE :		REFLECTED CEILING PLAN (FIRST FLOOR)		DRAWING'S STATUS :		ALL DRAWINGS ARE COPY-RIGHT OF:  GROO SPACE SDN BHD (1662567-V) LEVEL 3A, WISMA JAG, JALAN DESA UTAMA, TAMAN DESA, 58100 KUALA LUMPUR T: +6016-913 6785 / +6012-528 7212 E: groospacemy@gmail.com IG: @groospace.my	CLIENTS ACKNOWLEDGE & SIGN :
PROJECT :	HANA RESIDENCE, TROPICANA AMAN	INTERIOR DESIGNER :	YANXIANG & YS	SALE PERSON :	RAYMOND	1ST DRAFT (R0)	09 OCT' 26		
						AMENDMENT 01			
						AMENDMENT 02			
						AMENDMENT 03			
CLIENT :	MS SHEON & MR TEE	CHECK BY :	RAYMOND			ID.01.10	AMENDMENT 04		
"NOTICE TO CONTRACTOR: DO NOT SCALE DRAWINGS. All dimensions and site levels must be Verified In Field (V.I.F.) before any fabrication or commencement of work. Any discrepancies between these drawings and actual site conditions must be reported to the Designer immediately for clarification. Failure to do so will be at the Contractor's own risk."									

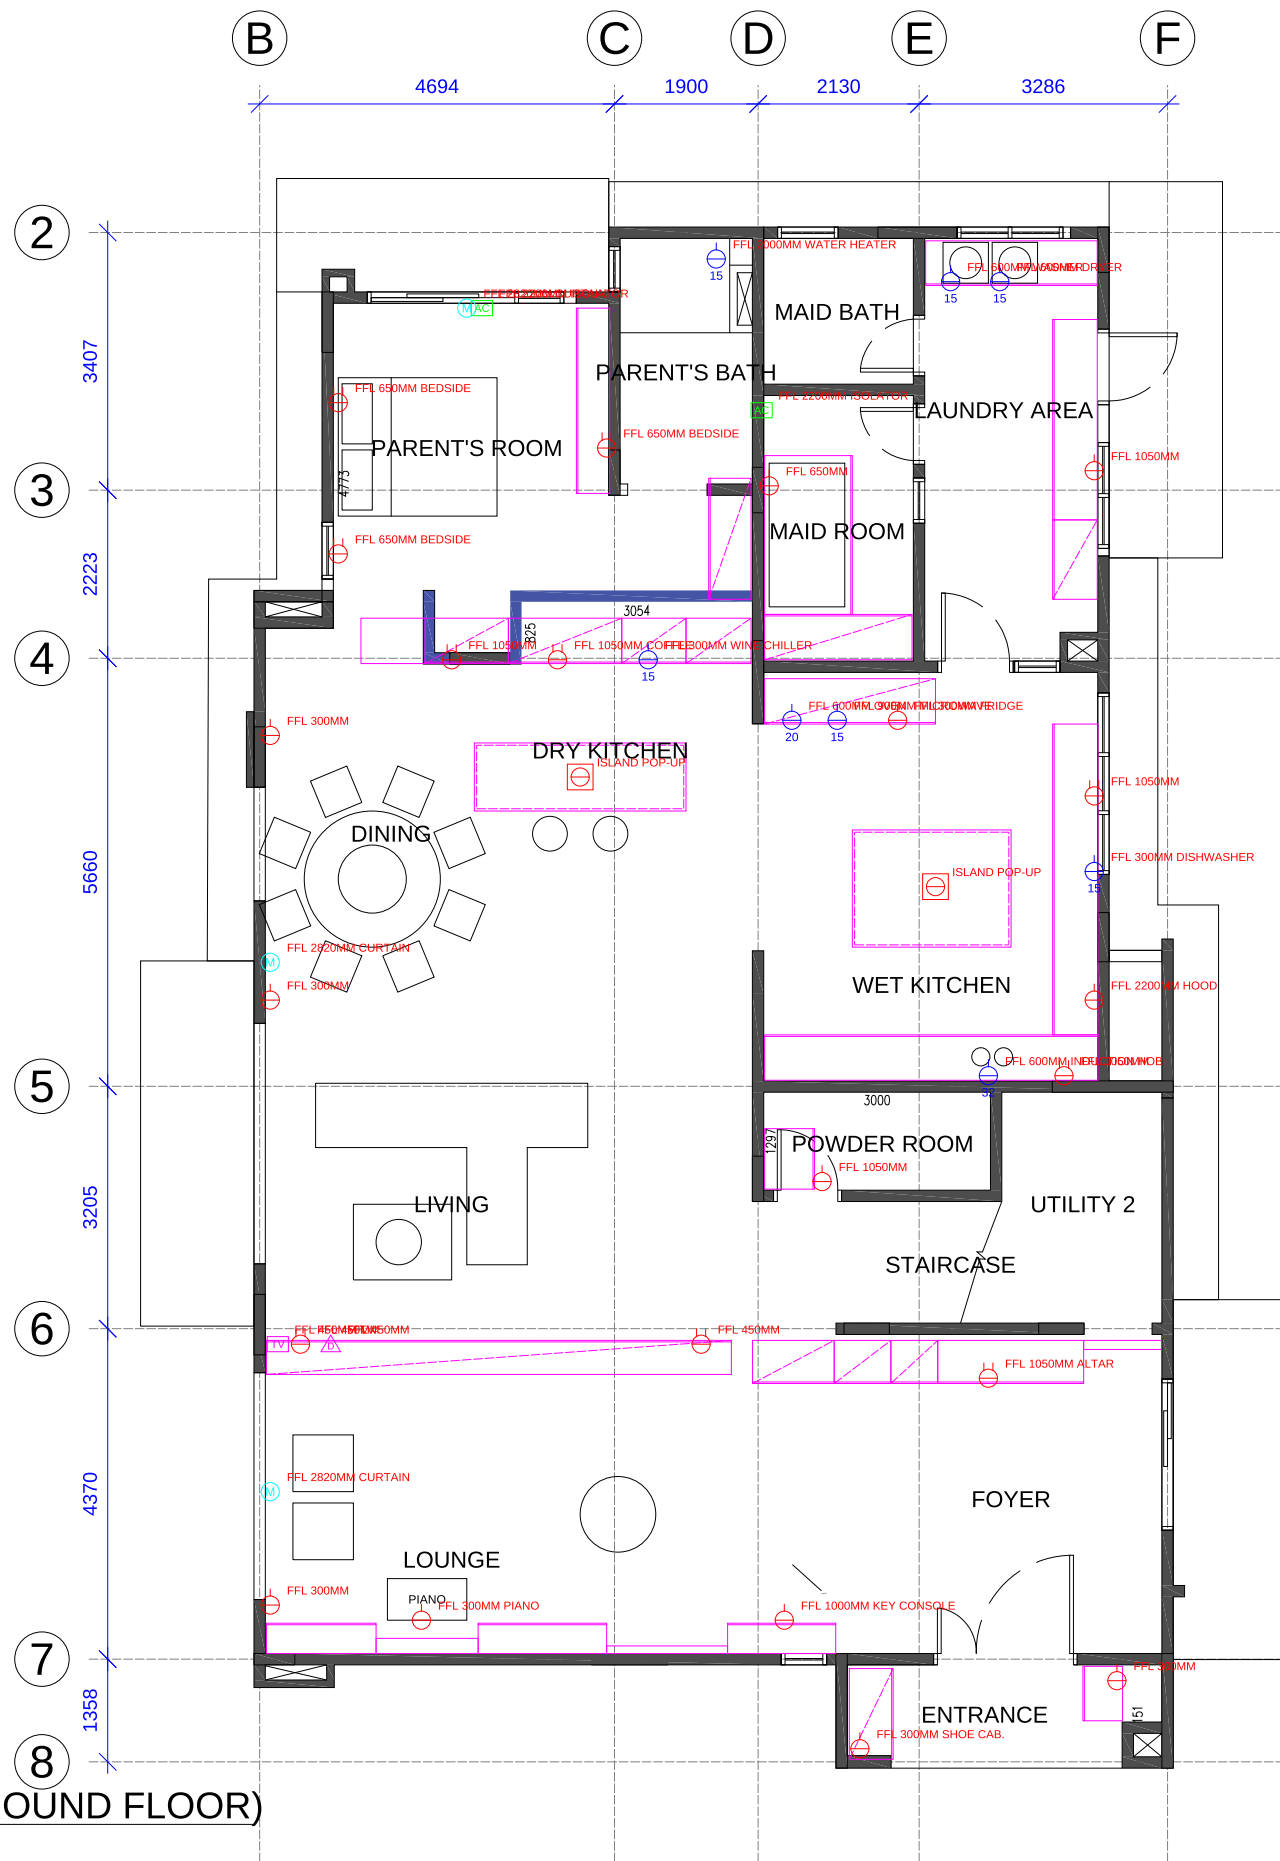


LEGEND (SOCKET):		
	NEW 13AMP SINGLE POWER POINT	12
	NEW 13AMP TWIN POWER POINT	10
	NEW 15AMP POWER POINT	6
	NEW 20AMP POWER POINT (OVEN)	1
	NEW 32AMP POWER POINT (INDUCTION HOB)	1
	AIR-COND ISOLATOR POINT	2
	TV POINT	1
	DATA / CAT6 POINT	1
	SMART CURTAIN MOTOR POINT	3
	FLOOR / POP-UP SOCKET	2

ALL HEIGHTS FFL TO CENTRE OF FACEPLATE.
DB UPGRADE / NEW SUB-DB TO BE CONFIRMED AFTER LOAD CHECK.

ID 01 M&E PLAN - SOCKET (GROUND FLOOR)
SCALE 1:100

M&E PLAN - SOCKET ID 11
GROUND FLOOR

PROJECT TYPE :	DESIGN & BUILD	DRAWING TITLE :	M&E PLAN - SOCKET (GROUND FLOOR)	DRAWING'S STATUS :	09 OCT '26	ALL DRAWINGS ARE COPY-RIGHT OF:	CLIENTS ACKNOWLEDGE & SIGN :
PROJECT :	HANA RESIDENCE, TROPICANA AMAN	INTERIOR DESIGNER :	YANXIANG & YS	SALE PERSON :	RAYMOND	 GROO SPACE SDN BHD (1662567-V) LEVEL 3A, WISMA JAG, JALAN DESA UTAMA, TAMAN DESA, 58100 KUALA LUMPUR T: +6016-913 6785 / +6012-528 7212 E: groospacemy@gmail.com IG: @groospace.my	
CLIENT :	MS SHEON & MR TEE	CHECK BY :	RAYMOND	ID.01.11			
"NOTICE TO CONTRACTOR: DO NOT SCALE DRAWINGS. All dimensions and site levels must be Verified In Field (V.I.F.) before any fabrication or commencement of work. Any discrepancies between these drawings and actual site conditions must be reported to the Designer immediately for clarification. Failure to do so will be at the Contractor's own risk."							

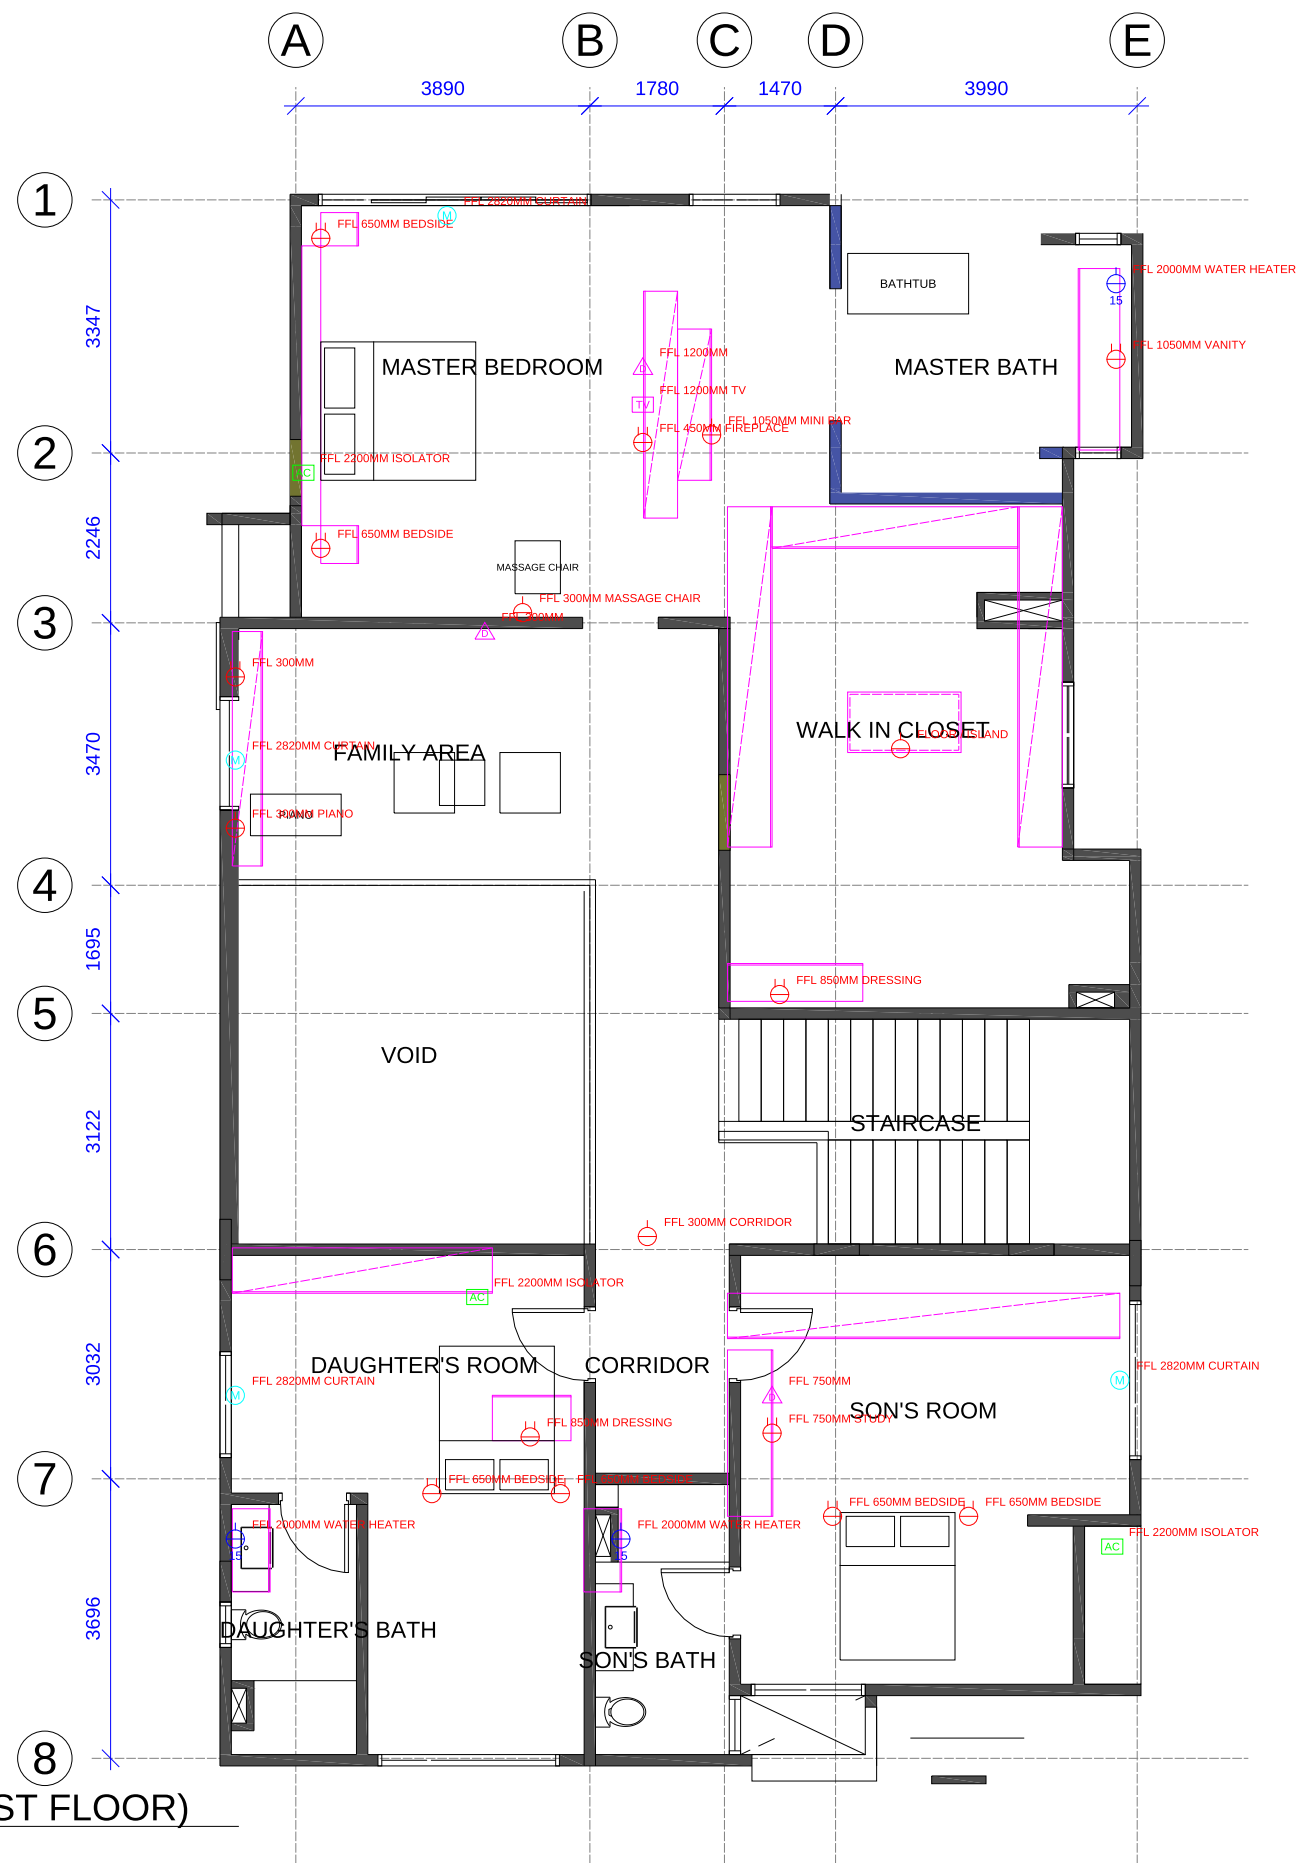

ID	M&E PLAN - SOCKET (FIRST FLOOR)
01	SCALE 1:100

<u>LEGEND (SOCKET):</u>		
	NEW 13AMP SINGLE POWER POINT	5
	NEW 13AMP TWIN POWER POINT	12
	NEW 15AMP POWER POINT	3
	NEW 20AMP POWER POINT (OVEN)	0
	NEW 32AMP POWER POINT (INDUCTION HOB)	0
	AIR-COND ISOLATOR POINT	3
	TV POINT	1
	DATA / CAT6 POINT	3
	SMART CURTAIN MOTOR POINT	4
	FLOOR / POP-UP SOCKET	0

ALL HEIGHTS FFL TO CENTRE OF FACEPLATE.
DB UPGRADE / NEW SUB-DB TO BE CONFIRMED AFTER LOAD CHECK.

M&E PLAN - SOCKET
FIRST FLOOR

PROJECT TYPE :	DESIGN & BUILD	DRAWING TITLE :		M&E PLAN - SOCKET (FIRST FLOOR)		DRAWING'S STATUS :		ALL DRAWINGS ARE COPY-RIGHT OF:  GROO SPACE SDN BHD (1662567-V) LEVEL 3A, WISMA JAG, JALAN DESA UTAMA, TAMAN DESA, 58100 KUALA LUMPUR T: +6016-913 6785 / +6012-528 7212 E: groospacemy@gmail.com IG: @groospace.my	CLIENTS ACKNOWLEDGE & SIGN :
PROJECT :	HANA RESIDENCE, TROPICANA AMAN	INTERIOR DESIGNER :	YANXIANG & YS	SALE PERSON :	RAYMOND	1ST DRAFT (R0)	09 OCT' 26		
						AMENDMENT 01			
						AMENDMENT 02			
CLIENT :	MS SHEON & MR TEE	CHECK BY :	RAYMOND		ID.01.12	AMENDMENT 03			
						AMENDMENT 04			

"NOTICE TO CONTRACTOR: DO NOT SCALE DRAWINGS. All dimensions and site levels must be Verified In Field (V.I.F.) before any fabrication or commencement of work. Any discrepancies between these drawings and actual site conditions must be reported to the Designer immediately for clarification. Failure to do so will be at the Contractor's own risk."




	1 GANG LIGHT SWITCH	5
	2 GANG LIGHT SWITCH	5
	3 GANG LIGHT SWITCH	4

LIGHTING PLAN

GROUND FLOOR

"NOTICE TO CONTRACTOR: DO NOT SCALE DRAWINGS. All dimensions and site levels must be Verified In Field (V.I.F.) before any fabrication or commencement of work. Any discrepancies between these drawings and actual site conditions must be reported to the Designer immediately for clarification. Failure to do so will be at the Contractor's own risk."

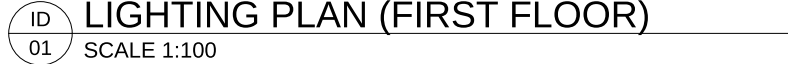

	1 GANG LIGHT SWITCH	3
	2 GANG LIGHT SWITCH	6
	3 GANG LIGHT SWITCH	1

LIGHTING PLAN
FIRST FLOOR

"NOTICE TO CONTRACTOR: DO NOT SCALE DRAWINGS. All dimensions and site levels must be Verified In Field (V.I.F.) before any fabrication or commencement of work. Any discrepancies between these drawings and actual site conditions must be reported to the Designer immediately for clarification. Failure to do so will be at the Contractor's own risk."




	JOTUN EMULSION (TBC) - WHOLE UNIT INCL. EXISTING DOOR & FRAME
	SUZUKA LIMEWASH / TEXTURE (TBC) FEATURE WALL
	JOTUN WARM GREY (TBC)
	LIMESTONE JH12352GZ WALL TILE 600x1200 STRUCTURED
	PL0242 BW OAK BACK PANEL (ALTAR)

WALL FINISHES PLAN

GROUND FLOOR

PROJECT TYPE :		DESIGN & BUILD		DRAWING TITLE :		WALL FINISHES PLAN (GROUND FLOOR)		DRAWING'S STATUS :		ALL DRAWINGS ARE COPY-RIGHT OF:		CLIENTS ACKNOWLEDGE & SIGN :	
PROJECT :		HANA RESIDENCE, TROPICANA AMAN		INTERIOR DESIGNER :		YANXIANG & YS		SALE PERSON :		RAYMOND		ID.01.15	
CLIENT :		MS SHEON & MR TEE		CHECK BY :		RAYMOND		ID.01.15		groo space		GROO SPACE SDN BHD (1662567-V) LEVEL 3A, WISMA JAG, JALAN DESA UTAMA, TAMAN DESA, 58100 KUALA LUMPUR T: +6016-913 6785 / +6012-528 7212 E: groospacemy@gmail.com IG: @groospace.my	

"NOTICE TO CONTRACTOR: DO NOT SCALE DRAWINGS. All dimensions and site levels must be Verified In Field (V.I.F.) before any fabrication or commencement of work. Any discrepancies between these drawings and actual site conditions must be reported to the Designer immediately for clarification. Failure to do so will be at the Contractor's own risk."

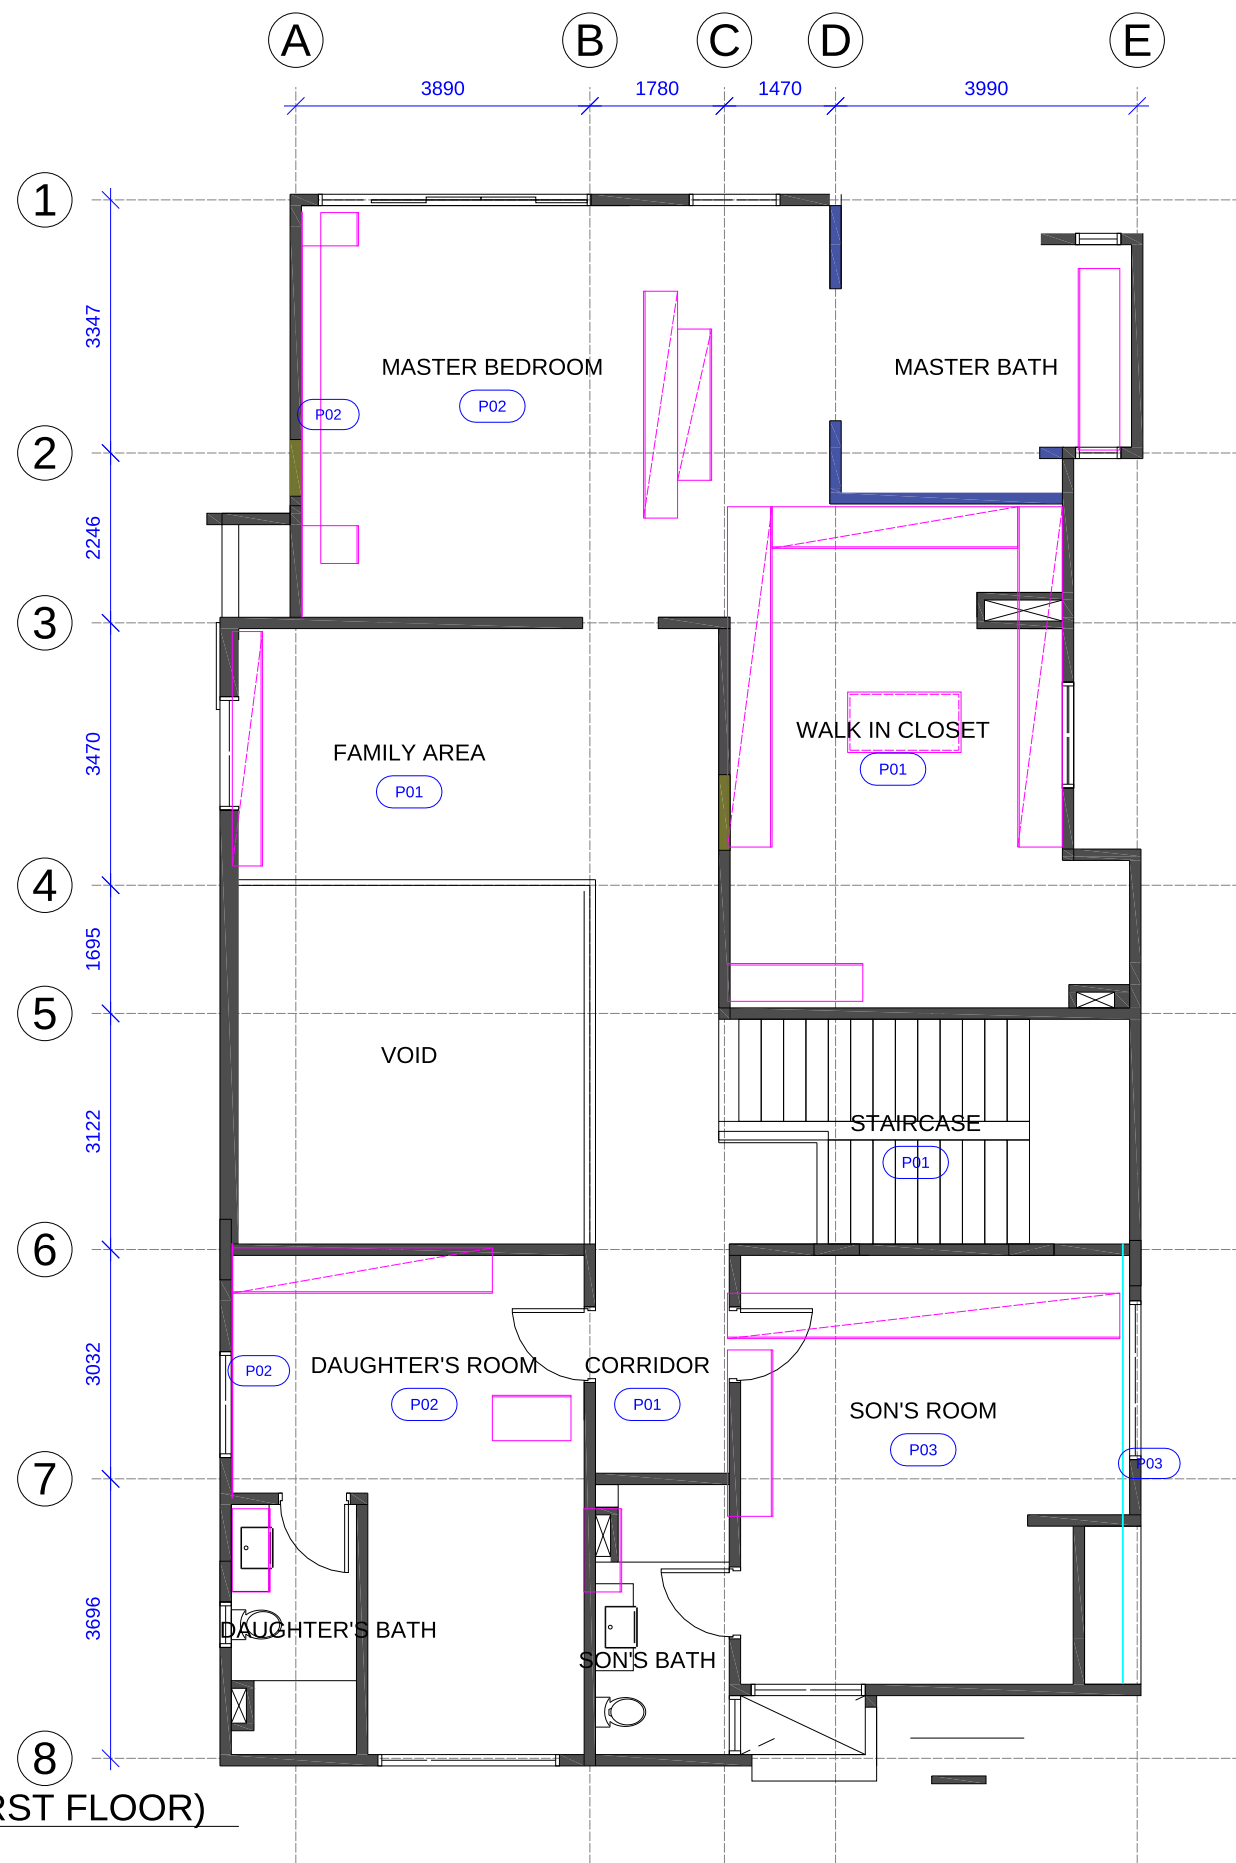

	JOTUN EMULSION (TBC) - WHOLE UNIT INCL. EXISTING DOOR & FRAME
	SUZUKA LIMEWASH / TEXTURE (TBC) FEATURE WALL
	JOTUN WARM GREY (TBC)
	LIMESTONE JH12352GZ WALL TILE 600x1200 STRUCTURED
	PL0242 BW OAK BACK PANEL (ALTAR)

WALL FINISHES PLAN (FIRST FLOOR)

WALL FINISHES PLAN

FIRST FLOOR

PROJECT TYPE :		DESIGN & BUILD		DRAWING TITLE :		WALL FINISHES PLAN (FIRST FLOOR)		DRAWING'S STATUS :		ALL DRAWINGS ARE COPY-RIGHT OF:		CLIENTS ACKNOWLEDGE & SIGN :	
PROJECT :		HANA RESIDENCE, TROPICANA AMAN		INTERIOR DESIGNER :		YANXIANG & YS		SALE PERSON :		RAYMOND		RAYMOND	
CLIENT :		MS SHEON & MR TEE		CHECK BY :		RAYMOND		ID.01.16		1ST DRAFT (R0)		09 OCT' 26	
										groo space		GROO SPACE SDN BHD (1662567-V) LEVEL 3A, WISMA JAG, JALAN DESA UTAMA, TAMAN DESA, 58100 KUALA LUMPUR T: +6016-913 6785 / +6012-528 7212 E: groospacemy@gmail.com IG: @groospace.my	

"NOTICE TO CONTRACTOR: DO NOT SCALE DRAWINGS. All dimensions and site levels must be Verified In Field (V.I.F.) before any fabrication or commencement of work. Any discrepancies between these drawings and actual site conditions must be reported to the Designer immediately for clarification. Failure to do so will be at the Contractor's own risk."



FLOORING INTERFACE (TILES TO ENGINEERED WOOD):
 - 100% FLUSH, ZERO DROP.
 - FLEXIBLE L-SHAPE S/STEEL EDGE TRIM ALONG TILE BORDER INCL. CURVES - 3MM EXPANSION GAP SEALED W/ ANTI-FUNGUS SILICONE MATCHING FLOOR COLOUR.
 AREAS ARE ROUGH TAKE-OFF (EXCL. WASTAGE) - V.I.F.


FLOOR FINISHES PLAN

GROUND FLOOR

ID

17

PROJECT TYPE :	DESIGN & BUILD	DRAWING TITLE :		FLOOR FINISHES PLAN (GROUND FLOOR)		DRAWING'S STATUS :		ALL DRAWINGS ARE COPY-RIGHT OF:  GROO SPACE SDN BHD (1662567-V) LEVEL 3A, WISMA JAG, JALAN DESA UTAMA, TAMAN DESA, 58100 KUALA LUMPUR T: +6016-913 6785 / +6012-528 7212 E: groospacemy@gmail.com IG: @groospace.my	CLIENTS ACKNOWLEDGE & SIGN :
PROJECT :	HANA RESIDENCE, TROPICANA AMAN	INTERIOR DESIGNER :	YANXIANG & YS	SALE PERSON :	RAYMOND	1ST DRAFT (R0)	09 OCT' 26		
						AMENDMENT 01			
						AMENDMENT 02			
						AMENDMENT 03			
CLIENT :	MS SHEON & MR TEE	CHECK BY :	RAYMOND		ID.01.17	AMENDMENT 04			
"NOTICE TO CONTRACTOR: DO NOT SCALE DRAWINGS. All dimensions and site levels must be Verified In Field (V.I.F.) before any fabrication or commencement of work. Any discrepancies between these drawings and actual site conditions must be reported to the Designer immediately for clarification. Failure to do so will be at the Contractor's own risk."									

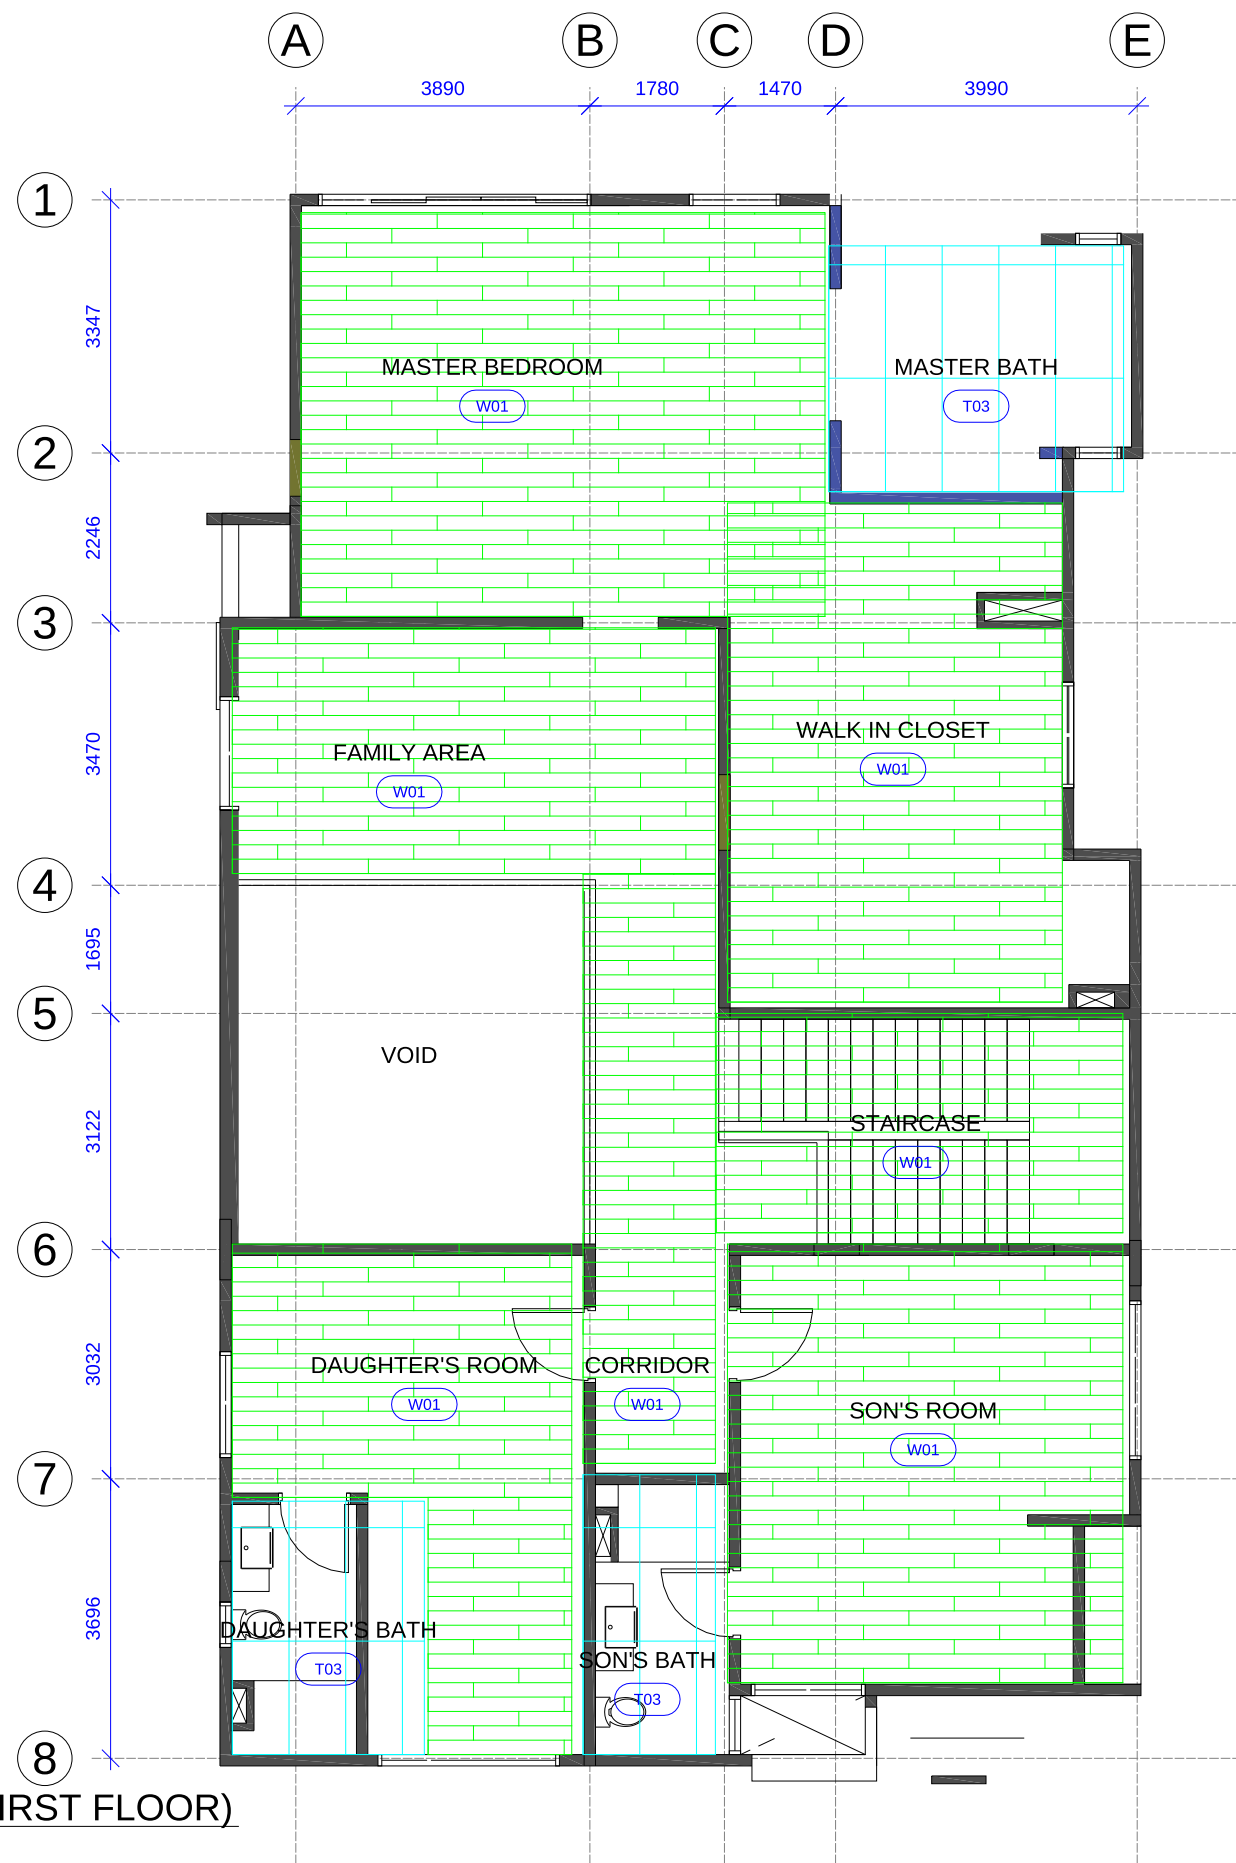

<u>LEGEND (FLOORING):</u>		
	DONG PENG 750x1500 (TBC) PORCELAIN	298 SF
	PORTER ROSEWOOD ENGINEERED WOOD 15-20MM	1809 SF

FLOORING INTERFACE (TILES TO ENGINEERED WOOD):
 - 100% FLUSH, ZERO DROP.
 - FLEXIBLE L-SHAPE S/STEEL EDGE TRIM ALONG TILE BORDER INCL. CURVES.- 3MM EXPANSION GAP SEALED W/ ANTI-FUNGUS SILICONE MATCHING FLOOR COLOUR.
AREAS ARE ROUGH TAKE-OFF (EXCL. WASTAGE) - V.I.F.

ID 01 FLOOR FINISHES PLAN (FIRST FLOOR) SCALE 1:100

FLOOR FINISHES PLAN

FIRST FLOOR

ID
18

PROJECT TYPE :		DESIGN & BUILD		DRAWING TITLE :		FLOOR FINISHES PLAN (FIRST FLOOR)		DRAWING'S STATUS :		ALL DRAWINGS ARE COPY-RIGHT OF:		CLIENTS ACKNOWLEDGE & SIGN :	
PROJECT :		HANA RESIDENCE, TROPICANA AMAN		INTERIOR DESIGNER :		YANXIANG & YS		SALE PERSON :		RAYMOND		RAYMOND	
CLIENT :		MS SHEON & MR TEE		CHECK BY :		RAYMOND		ID.01.18		1ST DRAFT (R0)		09 OCT' 26	
										groo space		GROO SPACE SDN BHD (1662567-V) LEVEL 3A, WISMA JAG, JALAN DESA UTAMA, TAMAN DESA, 58100 KUALA LUMPUR T: +6016-913 6785 / +6012-528 7212 E: groospacemy@gmail.com IG: @groospace.my	

"NOTICE TO CONTRACTOR: DO NOT SCALE DRAWINGS. All dimensions and site levels must be Verified In Field (V.I.F.) before any fabrication or commencement of work. Any discrepancies between these drawings and actual site conditions must be reported to the Designer immediately for clarification. Failure to do so will be at the Contractor's own risk."



WIDTHS INCLUDE 150MM OVERLAP EACH SIDE. HEIGHTS FROM CEILING / PELMET TO FFL+10MM. WINDOW SIZES V.I.F.

CURTAIN PLAN
GROUND FLOOR


PROJECT TYPE :		DESIGN & BUILD		DRAWING TITLE :		CURTAIN PLAN (GROUND FLOOR)		DRAWING'S STATUS :		ALL DRAWINGS ARE COPY-RIGHT OF:		CLIENTS ACKNOWLEDGE & SIGN :			
PROJECT :		HANA RESIDENCE, TROPICANA AMAN		INTERIOR DESIGNER :		YANXIANG & YS		SALE PERSON :		RAYMOND		1ST DRAFT (R0)		09 OCT' 26	
CLIENT :		MS SHEON & MR TEE		CHECK BY :		RAYMOND		ID.01.19		AMENDMENT 01		AMENDMENT 02		AMENDMENT 03	
										AMENDMENT 04					

groo

space

GROO SPACE SDN BHD (1662567-V)
LEVEL 3A, WISMA JAG, JALAN DESA UTAMA,
TAMAN DESA, 58100 KUALA LUMPUR
T: +6016-913 6785 / +6012-528 7212
E: groospacemy@gmail.com IG: @groospace.my

"NOTICE TO CONTRACTOR: DO NOT SCALE DRAWINGS. All dimensions and site levels must be Verified In Field (V.I.F.) before any fabrication or commencement of work. Any discrepancies between these drawings and actual site conditions must be reported to the Designer immediately for clarification. Failure to do so will be at the Contractor's own risk."

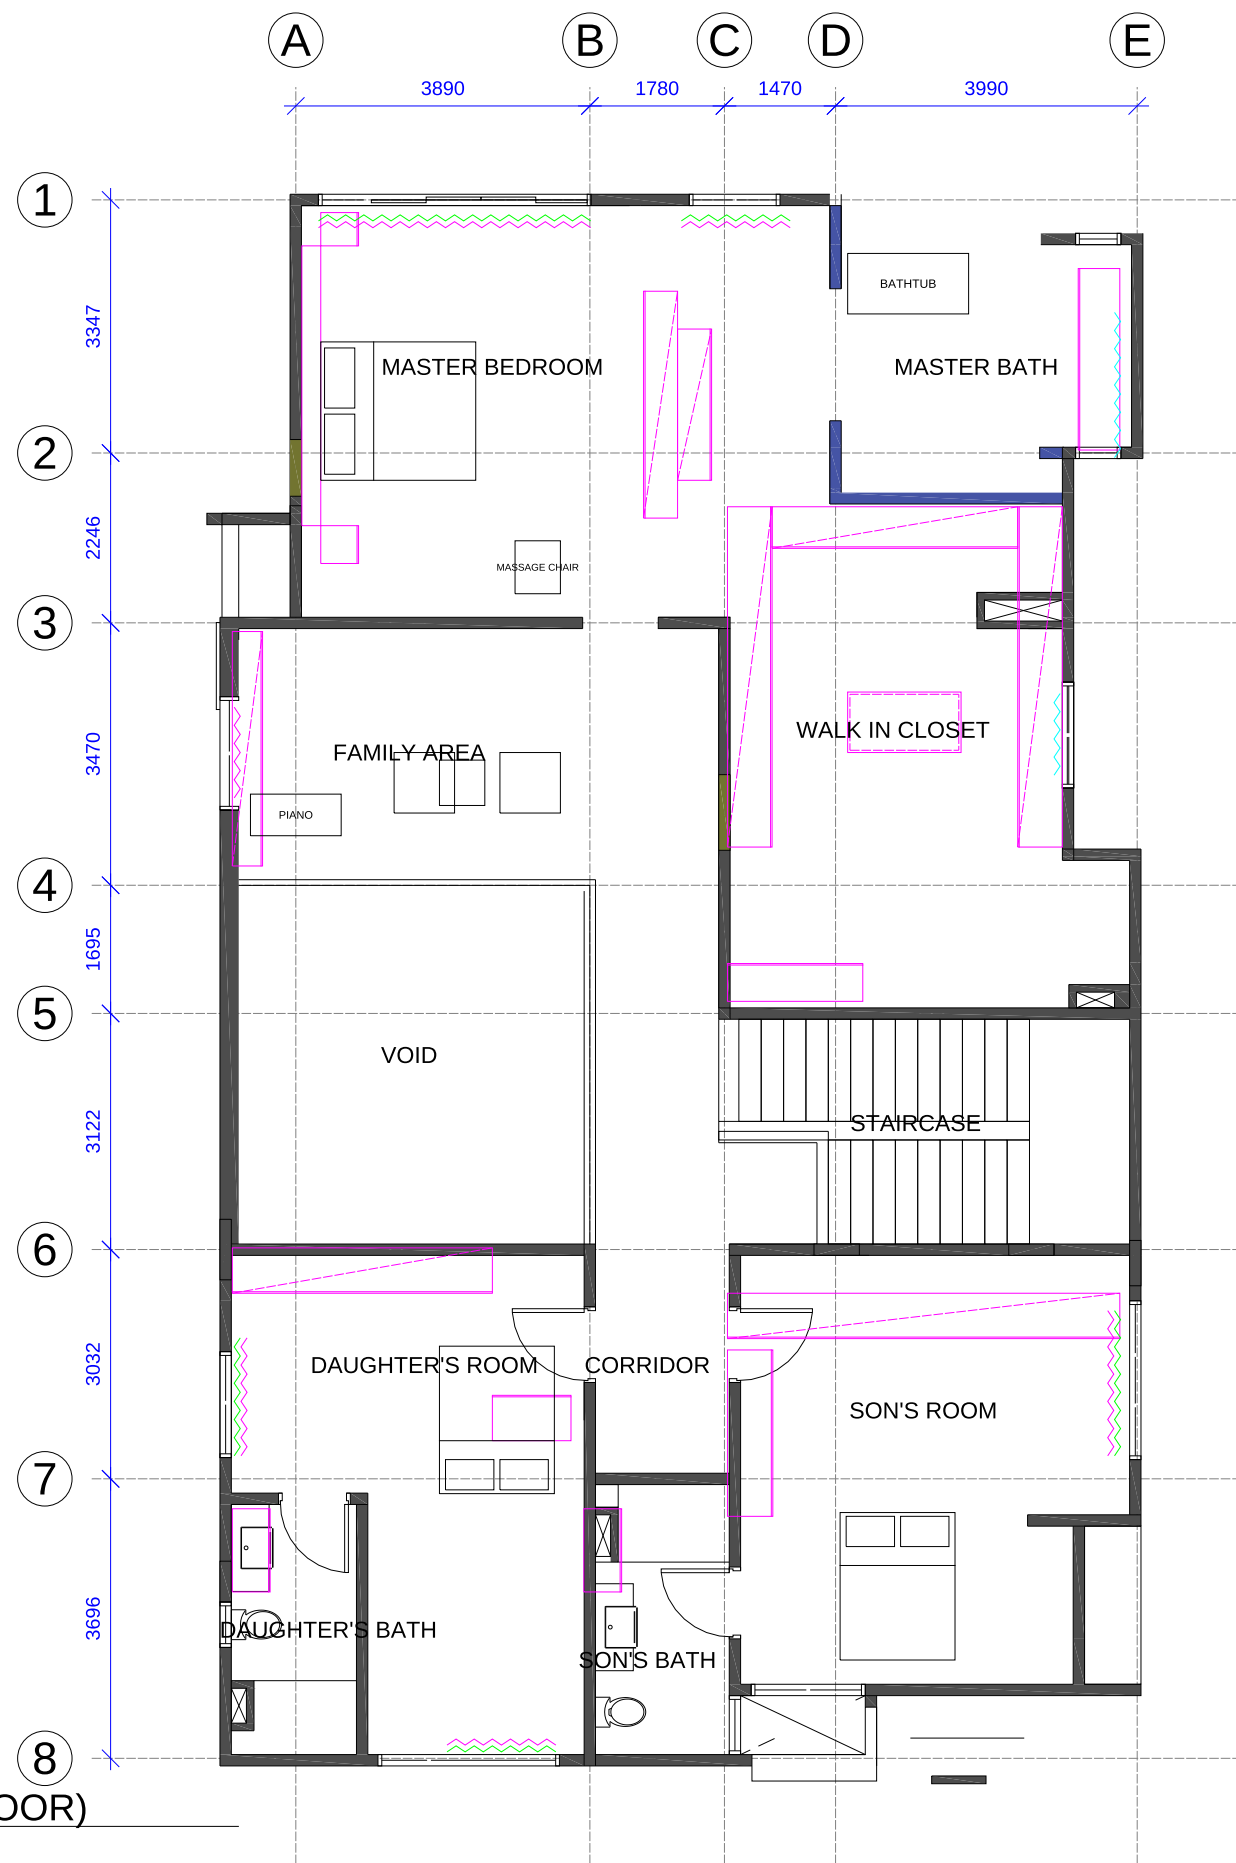

ID CURTAIN PLAN (FIRST FLOOR) 01 SCALE 1:100

LEGEND (CURTAIN / BLIND):

	SHEER CURTAIN (MOTORISED) RIPPLE FOLD	5 FT
	DAY + NIGHT CURTAIN (MOTORISED, SINGAPORE PLEAT)	38 FT
	ROLLER BLIND	0 FT
	ROMAN BLIND	12 FT
	SHOJI-STYLE PANEL / BLIND	0 FT

WIDTHS INCLUDE 150MM OVERLAP EACH SIDE. HEIGHTS FROM CEILING / PELMET TO FFL+10MM. WINDOW SIZES V.I.F.


CURTAIN PLAN

FIRST FLOOR

ID
20

PROJECT TYPE :		DESIGN & BUILD		DRAWING TITLE :		CURTAIN PLAN (FIRST FLOOR)		DRAWING'S STATUS :		ALL DRAWINGS ARE COPY-RIGHT OF:		CLIENTS ACKNOWLEDGE & SIGN :			
PROJECT :		HANA RESIDENCE, TROPICANA AMAN		INTERIOR DESIGNER :		YANXIANG & YS		SALE PERSON :		RAYMOND		1ST DRAFT (R0)		09 OCT' 26	
CLIENT :		MS SHEON & MR TEE		CHECK BY :		RAYMOND		ID.01.20		AMENDMENT 01		AMENDMENT 02		AMENDMENT 03	
										AMENDMENT 04					

"NOTICE TO CONTRACTOR: DO NOT SCALE DRAWINGS. All dimensions and site levels must be Verified In Field (V.I.F.) before any fabrication or commencement of work. Any discrepancies between these drawings and actual site conditions must be reported to the Designer immediately for clarification. Failure to do so will be at the Contractor's own risk."

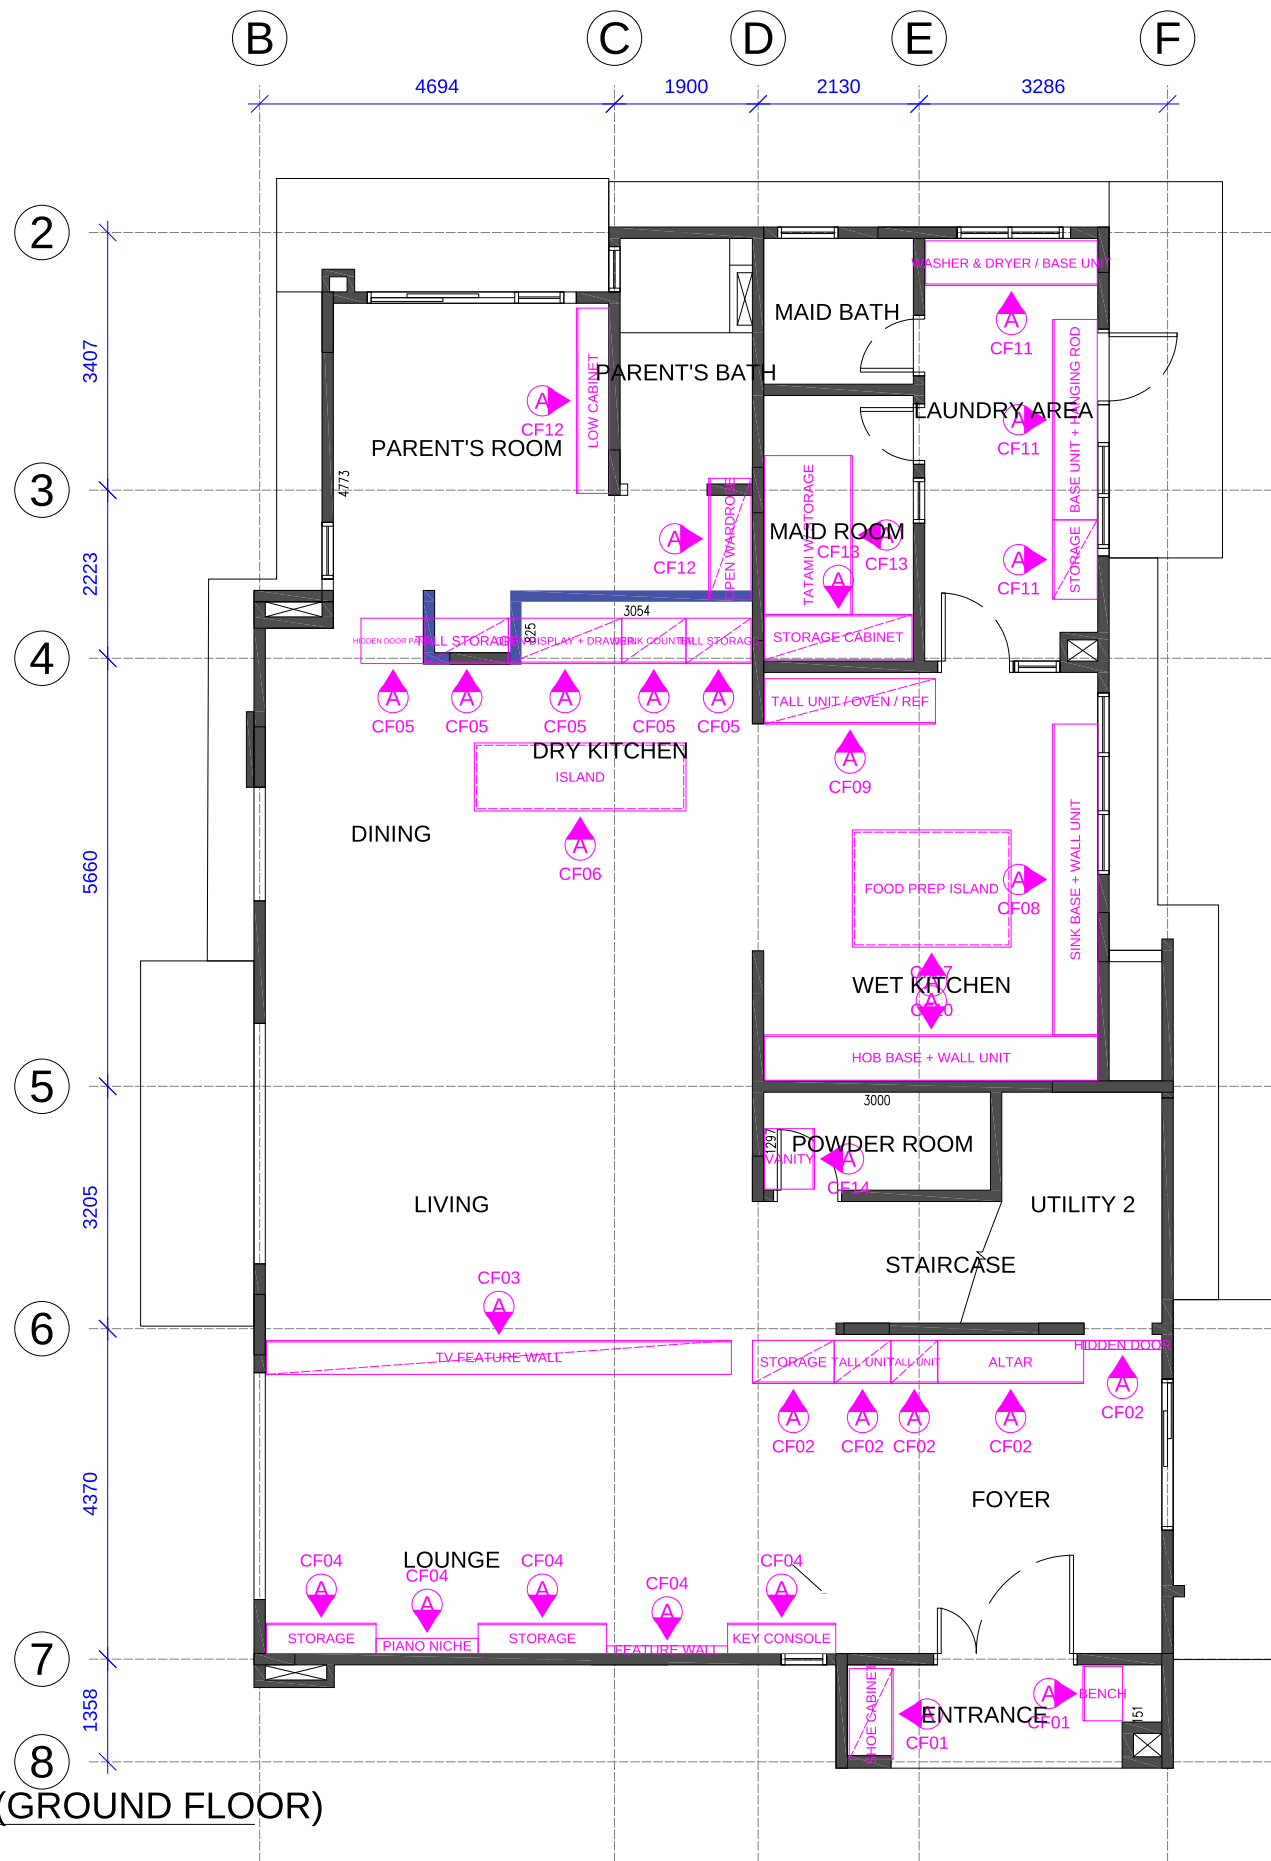

ELEVATION CODE:

CF01	CF01 - SHOE CABINET
CF02	CF02 - STORAGE
CF03	CF03 - TV FEATURE WALL
CF04	CF04 - STORAGE
CF05	CF05 - HIDDEN DOOR PANEL
CF06	CF06 - ISLAND
CF09	CF09 - TALL UNIT / OVEN / REF
CF08	CF08 - SINK BASE + WALL UNIT
CF07	CF07 - HOB BASE + WALL UNIT
CF10	CF10 - FOOD PREP ISLAND
CF11	CF11 - WASHER & DRYER / BASE UNIT
CF12	CF12 - LOW CABINET
CF13	CF13 - STORAGE CABINET
CF14	CF14 - VANITY

ID 01 ELEVATION CODE PLAN (GROUND FLOOR)
SCALE 1:100

ELEVATION CODE PLAN ID 21
GROUND FLOOR

PROJECT TYPE :	DESIGN & BUILD	DRAWING TITLE :	ELEVATION CODE PLAN (GROUND FLOOR)	DRAWING'S STATUS :	ALL DRAWINGS ARE COPY-RIGHT OF:	CLIENTS ACKNOWLEDGE & SIGN :
PROJECT :	HANA RESIDENCE, TROPICANA AMAN	INTERIOR DESIGNER :	YANXIANG & YS	SALE PERSON :	RAYMOND	
CLIENT :	MS SHEON & MR TEE	CHECK BY :	RAYMOND	ID.01.21		
"NOTICE TO CONTRACTOR: DO NOT SCALE DRAWINGS. All dimensions and site levels must be Verified In Field (V.I.F.) before any fabrication or commencement of work. Any discrepancies between these drawings and actual site conditions must be reported to the Designer immediately for clarification. Failure to do so will be at the Contractor's own risk."						


groospace

ALL DRAWINGS ARE COPY-RIGHT OF:
GROO SPACE SDN BHD (1662567-V)
LEVEL 3A, WISMA JAG, JALAN DESA UTAMA,
TAMAN DESA, 58100 KUALA LUMPUR
T: +6016-913 6785 / +6012-528 7212
E: groospacemy@gmail.com IG: @groospace.my



ELEVATION CODE PLAN


"NOTICE TO CONTRACTOR: DO NOT SCALE DRAWINGS. All dimensions and site levels must be Verified In Field (V.I.F.) before any fabrication or commencement of work. Any discrepancies between these drawings and actual site conditions must be reported to the Designer immediately for clarification. Failure to do so will be at the Contractor's own risk."

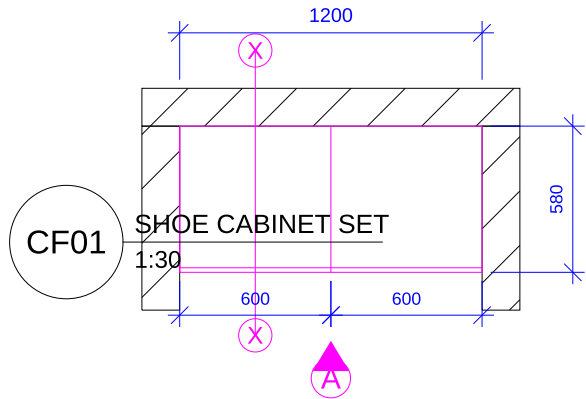


CF01

SHOE CABINET SET


1:30

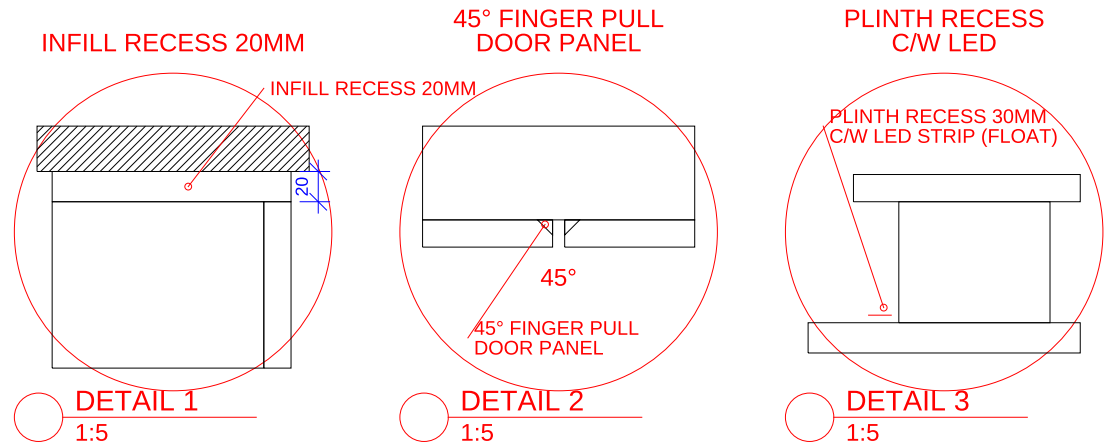


- NOTES:
- SHOE CABINET 580MM DEEP (SITE MEASURE 1200 x 580).
 - VENTILATION SLOT AT PLINTH, FLOATING LED 3000K.
 - BENCH 525 x 755 OPPOSITE: SOLID TOP ON BLACK LEG (REFER 3D).

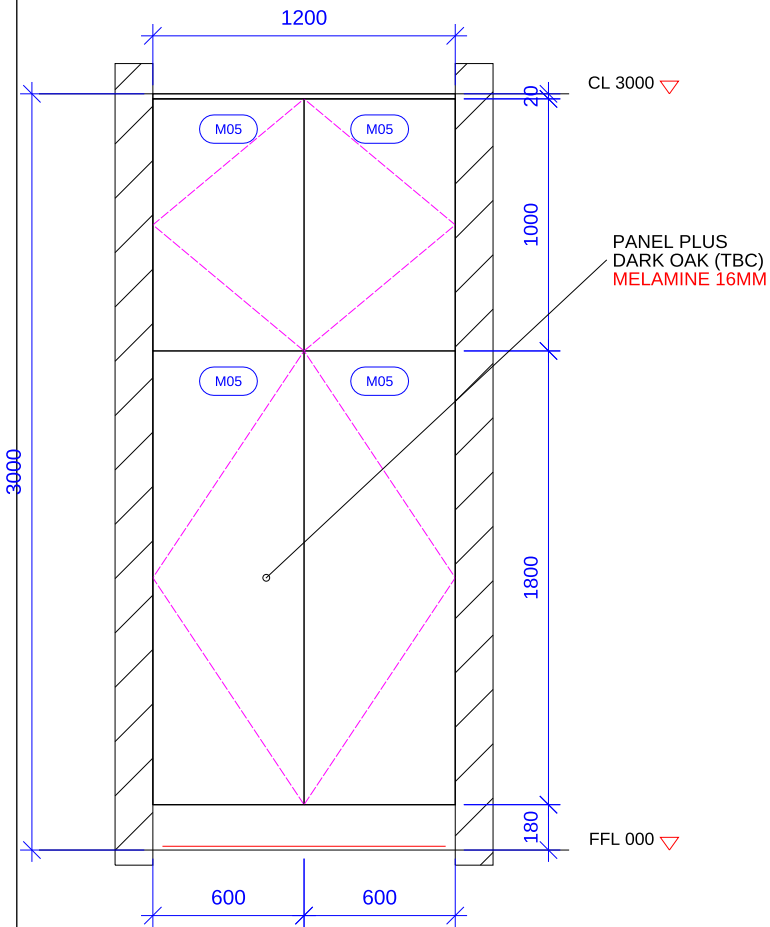

ELEVATION A
1:30

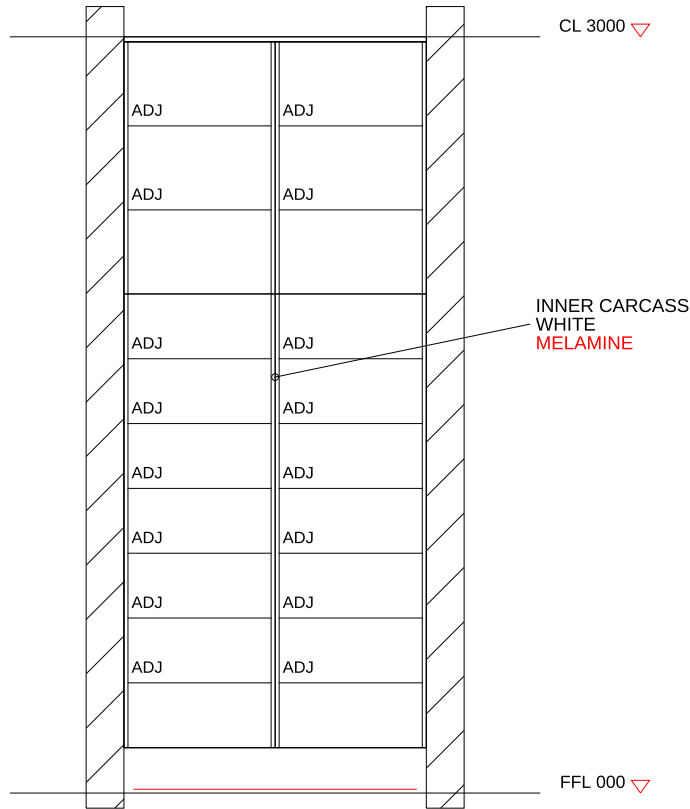

INNER CARCASS A
1:30

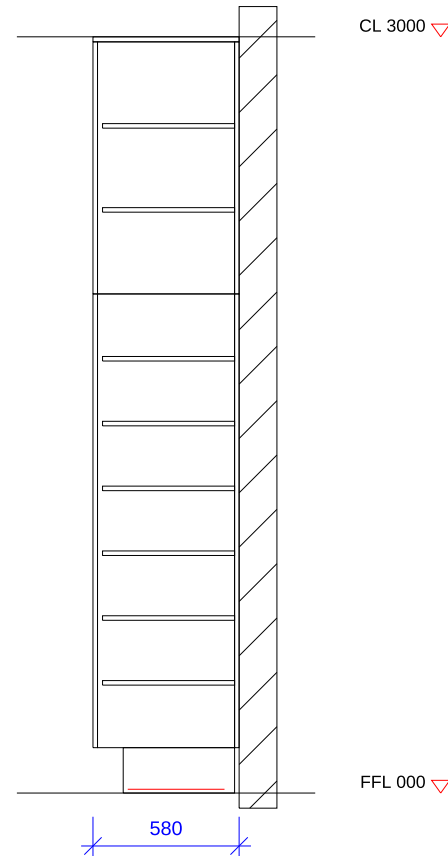

SECTION X-X
1:30


ENTRANCE - SHOE CABINET

ELEVATION PLAN

ID
02


PROJECT TYPE :	DESIGN & BUILD	DRAWING TITLE :	ENTRANCE SHOE CABINET ELEVATION	DRAWING'S STATUS :	ALL DRAWINGS ARE COPY-RIGHT OF:	CLIENTS ACKNOWLEDGE & SIGN :
PROJECT :	HANA RESIDENCE, TROPICANA AMAN	INTERIOR DESIGNER :	YANXIANG & YS	SALE PERSON :	RAYMOND	
CLIENT :	MS SHEON & MR TEE	CHECK BY :	RAYMOND	ID.02.01		

"NOTICE TO CONTRACTOR: DO NOT SCALE DRAWINGS. All dimensions and site levels must be Verified In Field (V.I.F.) before any fabrication or commencement of work. Any discrepancies between these drawings and actual site conditions must be reported to the Designer immediately for clarification. Failure to do so will be at the Contractor's own risk."

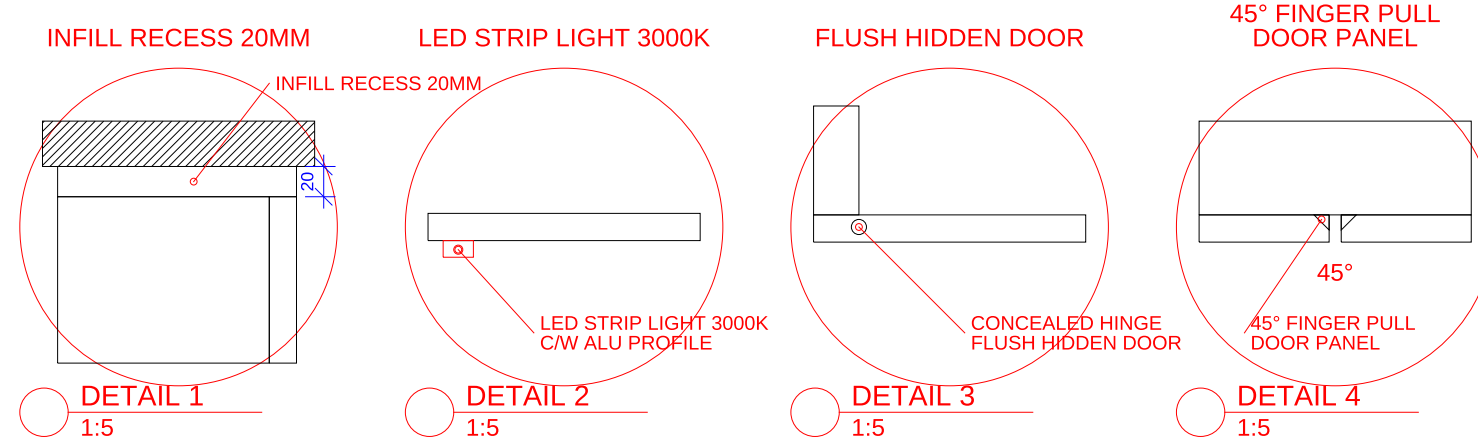

NOTES:

1. ALTAR NICHE BACK PANEL: PL0242 OAK C/W CONCEALED LED 3000K.
2. HIDDEN DOOR TO UTILITY 2: FLUSH, CONCEALED HINGE, PUSH LATCH.
3. ALTAR COUNTER SINTERED STONE 60MM (BUILT-UP EDGE).

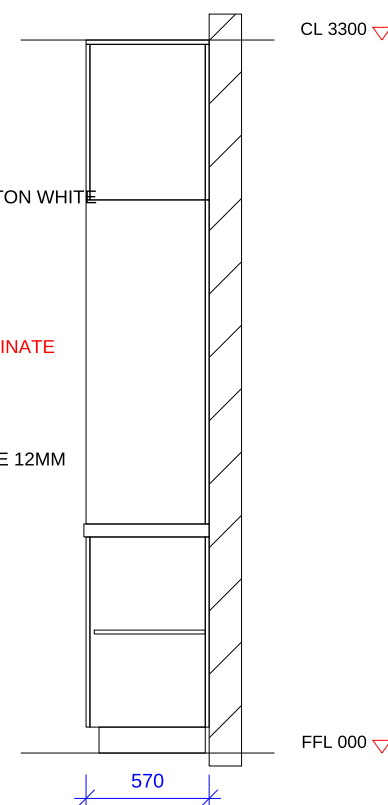

 ELEVATION A
1:35

SECTION X-X
1:35






FOYER - ALTAR & STORAGE WALL

ELEVATION PLAN



ID
02

PROJECT TYPE :		DESIGN & BUILD		DRAWING TITLE :			FOYER ALTAR & STORAGE WALL ELEVATION		DRAWING'S STATUS :		ALL DRAWINGS ARE COPY-RIGHT OF: groospace GROO SPACE SDN BHD (1662567-V) LEVEL 3A, WISMA JAG, JALAN DESA UTAMA, TAMAN DESA, 58100 KUALA LUMPUR T: +6016-913 6785 / +6012-528 7212 E: groospacemy@gmail.com IG: @groospace.my		CLIENTS ACKNOWLEDGE & SIGN :						
PROJECT :		HANA RESIDENCE, TROPICANA AMAN		INTERIOR DESIGNER :		YANXIANG & YS		SALE PERSON :		RAYMOND					1ST DRAFT (R0)		09 OCT' 26		
															AMENDMENT 01				
															AMENDMENT 02				
															AMENDMENT 03				
CLIENT :		MS SHEON & MR TEE		CHECK BY :		RAYMOND				ID.02.02		AMENDMENT 04							

"NOTICE TO CONTRACTOR: DO NOT SCALE DRAWINGS. All dimensions and site levels must be Verified In Field (V.I.F.) before any fabrication or commencement of work. Any discrepancies between these drawings and actual site conditions must be reported to the Designer immediately for clarification. Failure to do so will be at the Contractor's own risk."

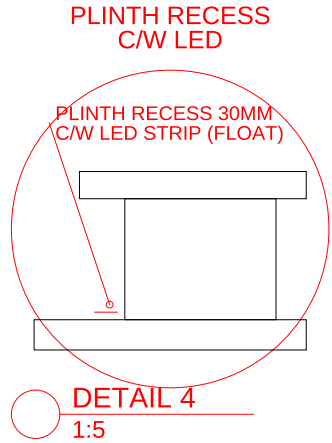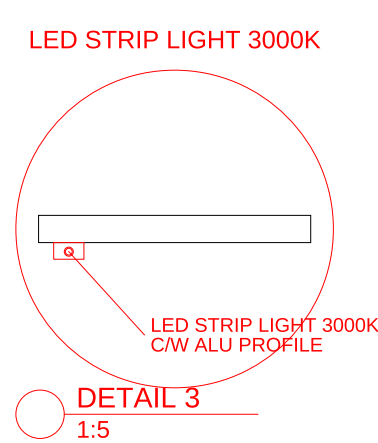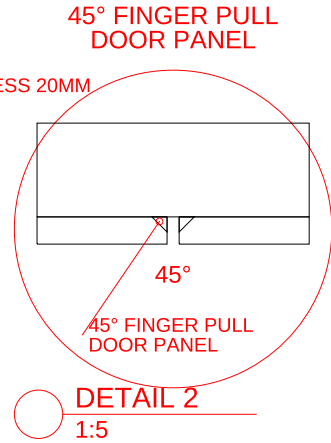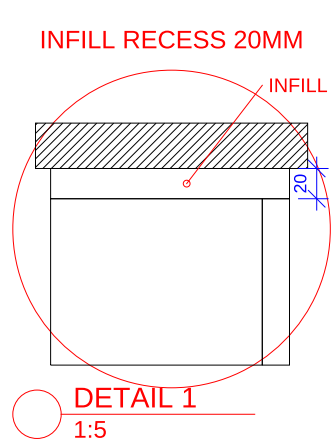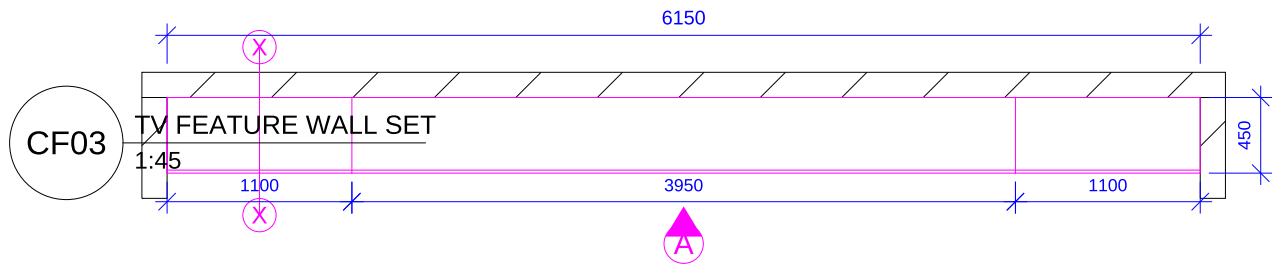

- NOTES:
- TV RECESS BACKED WITH FLUTED OAK PANEL C/W LED COVE.
 - CONCEALED CABLE TRUNKING TO CONSOLE.
 - SOUND BAR / AV EQUIPMENT IN CONSOLE - VENTILATED BACK.

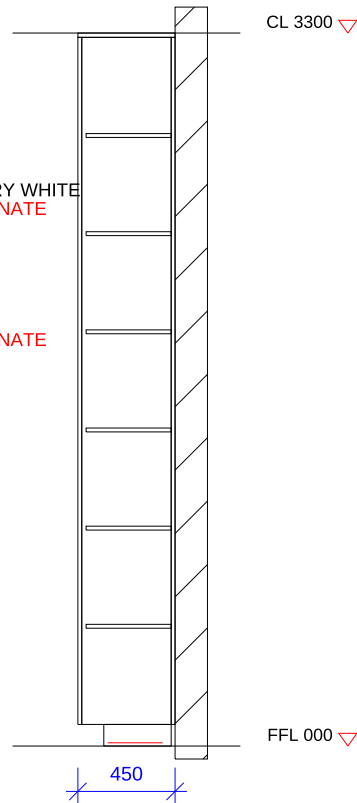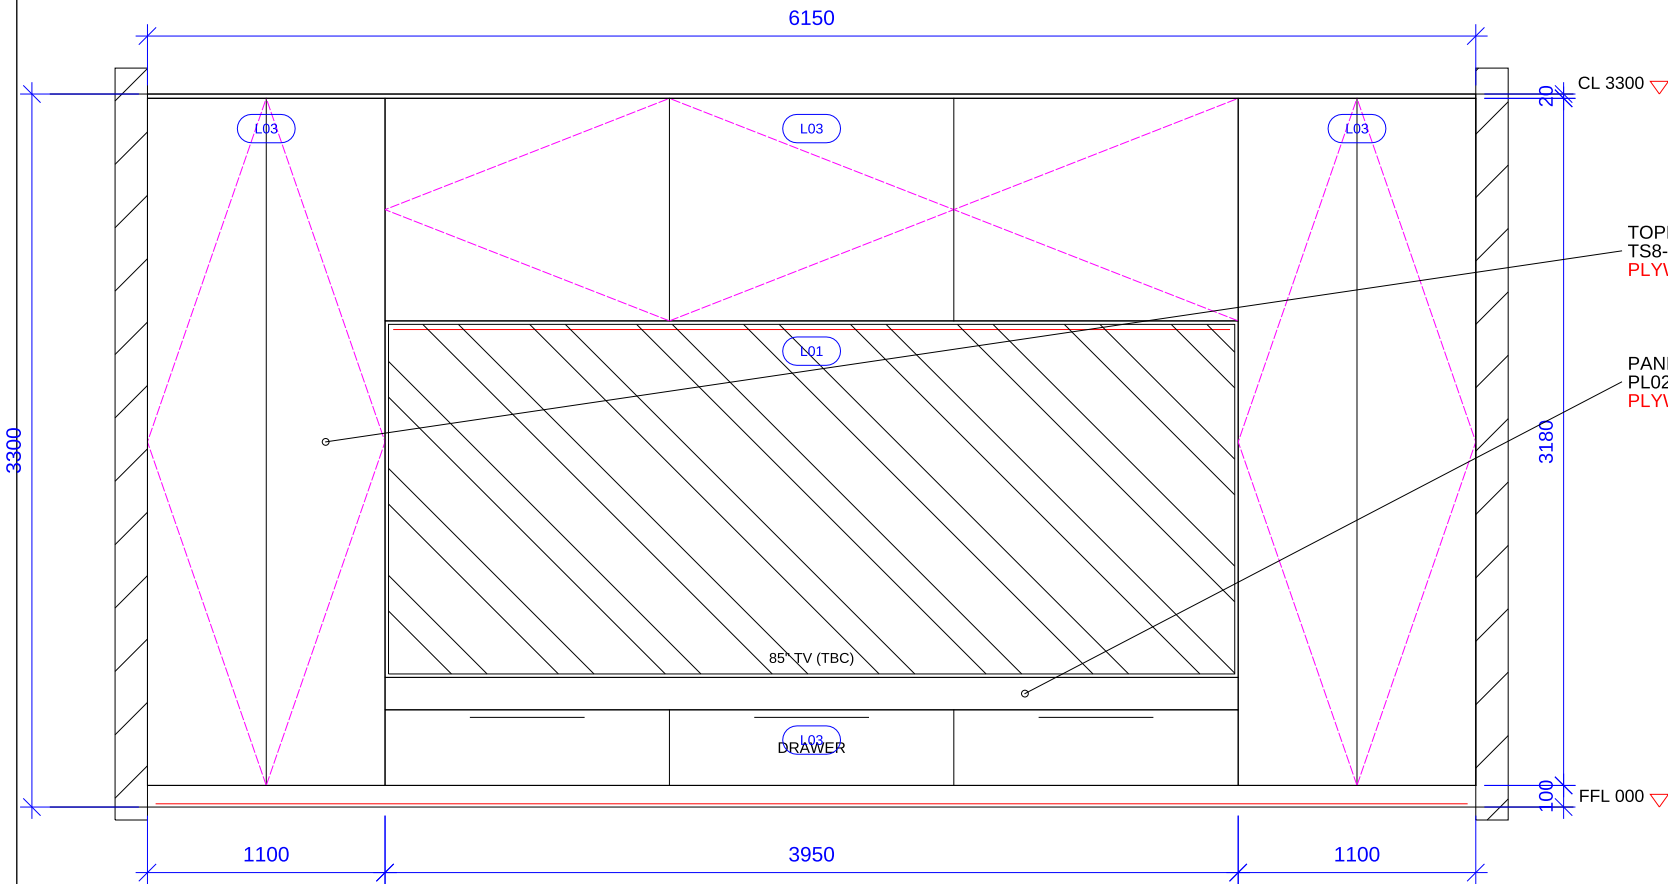

LIVING - TV FEATURE WALL


ELEVATION PLAN

ID
02

PROJECT TYPE :	DESIGN & BUILD	DRAWING TITLE :	LIVING TV FEATURE WALL ELEVATION	DRAWING'S STATUS :	ALL DRAWINGS ARE COPY-RIGHT OF:	CLIENTS ACKNOWLEDGE & SIGN :
PROJECT :	HANA RESIDENCE, TROPICANA AMAN	INTERIOR DESIGNER :	YANXIANG & YS	SALE PERSON :	RAYMOND	
CLIENT :	MS SHEON & MR TEE	CHECK BY :	RAYMOND	ID.02.03		

"NOTICE TO CONTRACTOR: DO NOT SCALE DRAWINGS. All dimensions and site levels must be Verified In Field (V.I.F.) before any fabrication or commencement of work. Any discrepancies between these drawings and actual site conditions must be reported to the Designer immediately for clarification. Failure to do so will be at the Contractor's own risk."


"NOTICE TO CONTRACTOR: DO NOT SCALE DRAWINGS. All dimensions and site levels must be Verified In Field (V.I.F.) before any fabrication or commencement of work. Any discrepancies between these drawings and actual site conditions must be reported to the Designer immediately for clarification. Failure to do so will be at the Contractor's own risk."

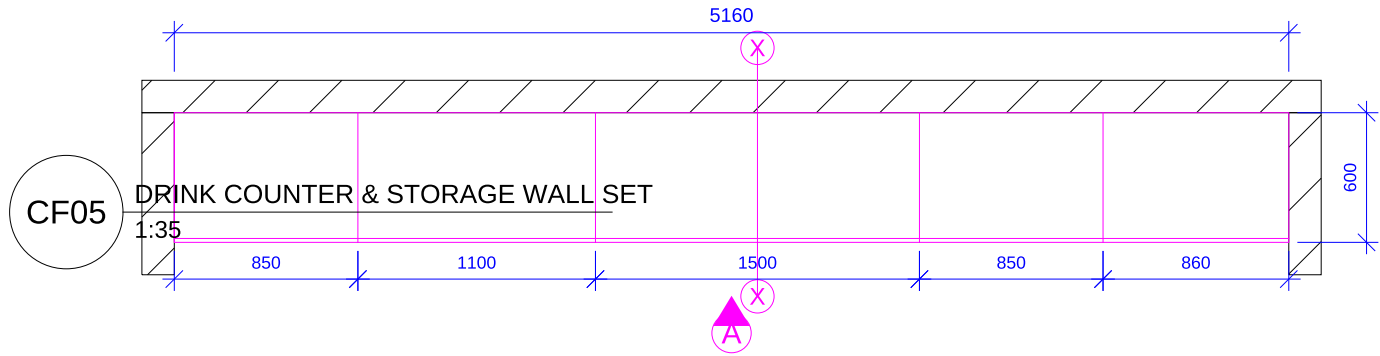


CF05

DRINK COUNTER & STORAGE WALL SET


1:35

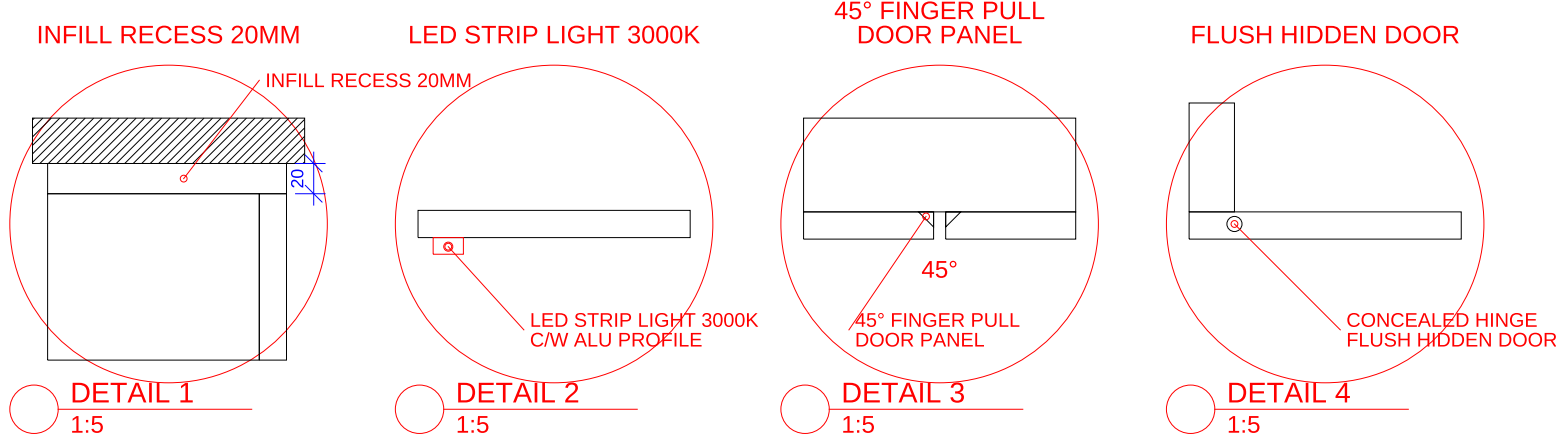

- NOTES:
- COFFEE STATION: 13A TWIN @ FFL 1050, WATER POINT FOR COFFEE MACHINE (TBC).
 - WINE CHILLER SUPPLIED BY OWNER - CUT-OUT TO MODEL SPEC.
 - OPEN NICHE BACK: SINTERED STONE / OAK (TBC).

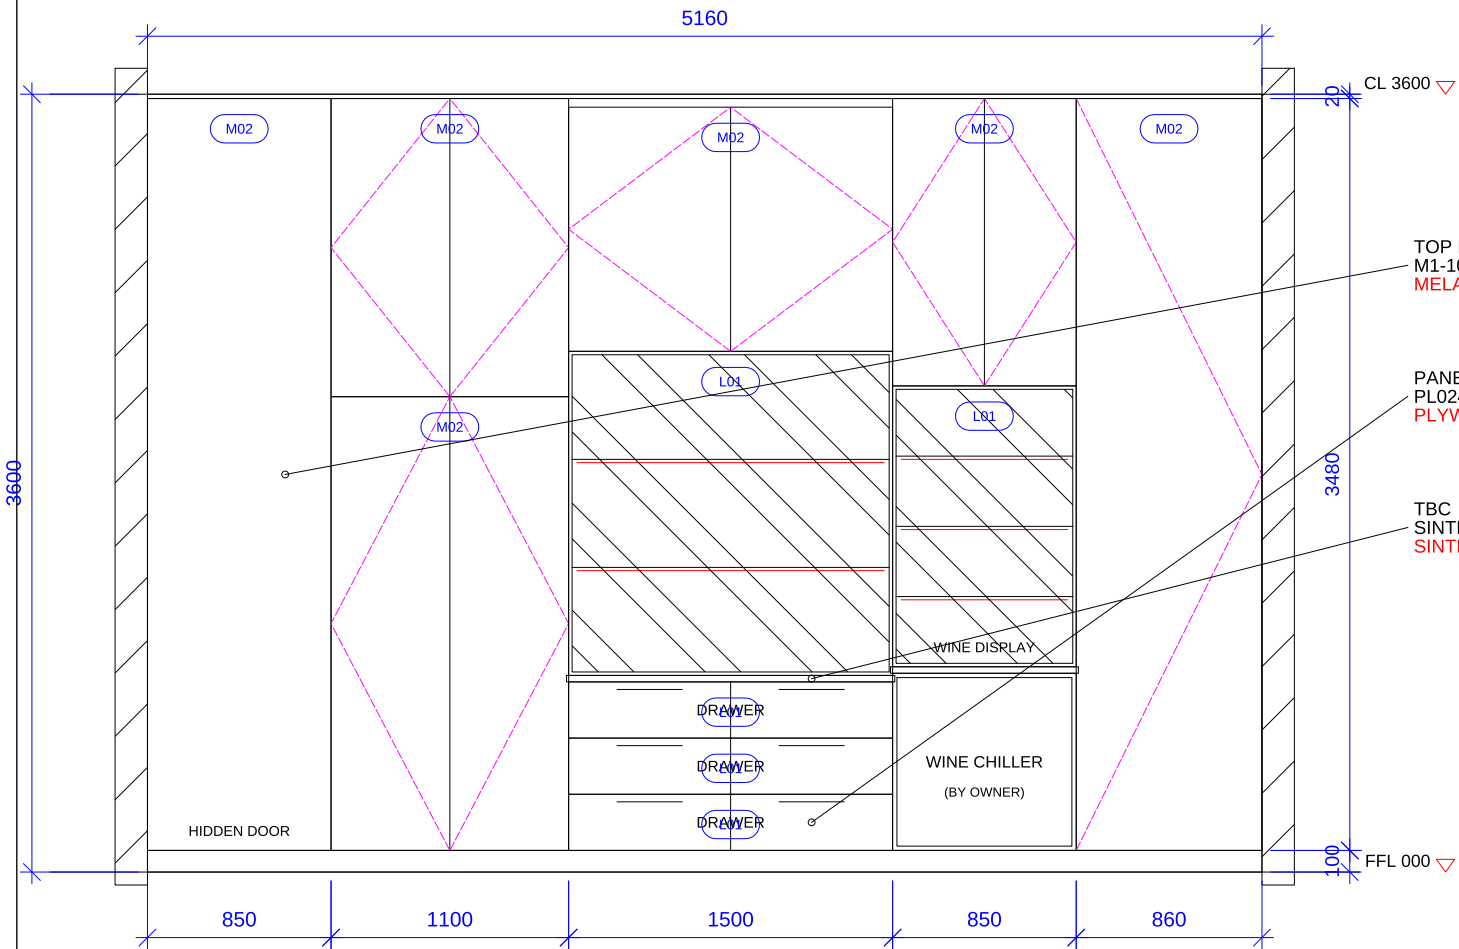

ELEVATION A
1:35

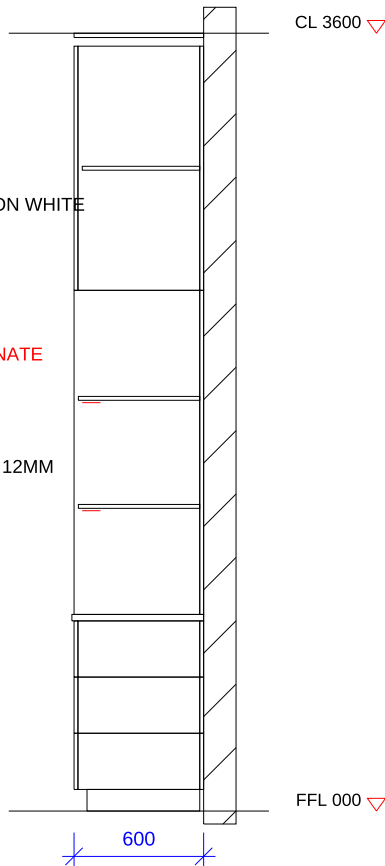

SECTION X-X
1:35


DRY KITCHEN - DRINK COUNTER & STORAGE WALL

ELEVATION PLAN

ID
02

PROJECT TYPE :	DESIGN & BUILD	DRAWING TITLE :	DRY KITCHEN DRINK COUNTER & STORAGE WALL ELEVATION	DRAWING'S STATUS :	ALL DRAWINGS ARE COPY-RIGHT OF:	CLIENTS ACKNOWLEDGE & SIGN :
PROJECT :	HANA RESIDENCE, TROPICANA AMAN	INTERIOR DESIGNER :	YANXIANG & YS	SALE PERSON :	RAYMOND	
CLIENT :	MS SHEON & MR TEE	CHECK BY :	RAYMOND	ID.02.05		


"NOTICE TO CONTRACTOR: DO NOT SCALE DRAWINGS. All dimensions and site levels must be Verified In Field (V.I.F.) before any fabrication or commencement of work. Any discrepancies between these drawings and actual site conditions must be reported to the Designer immediately for clarification. Failure to do so will be at the Contractor's own risk."

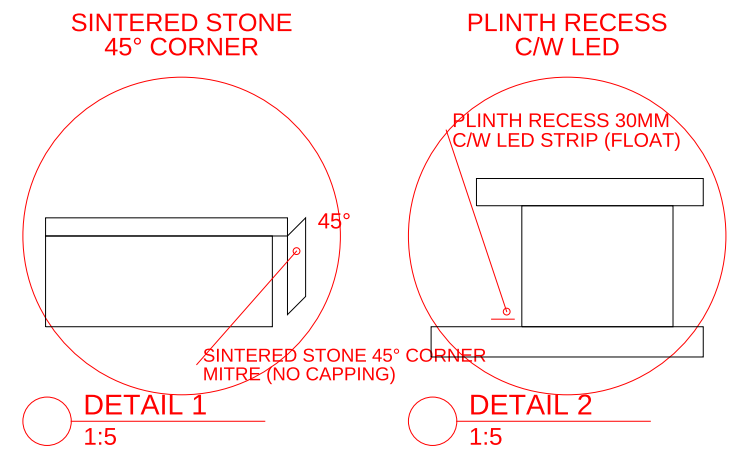

1. ISLAND 2800 x 900, SINTERED STONE 30MM C/W WATERFALL & CURVED END.
2. UNDERMOUNT ROUND SINK + POP-UP SOCKET.
3. WORKING SIDE: 2 x DOOR + 1 x DRAWER STACK (REFER PLAN).




PROJECT TYPE :	DESIGN & BUILD	DRAWING TITLE :		DRY KITCHEN ISLAND ELEVATION		DRAWING'S STATUS :		ALL DRAWINGS ARE COPY-RIGHT OF: GROO SPACE SDN BHD (1662567-V) LEVEL 3A, WISMA JAG, JALAN DESA UTAMA, TAMAN DESA, 58100 KUALA LUMPUR T: +6016-913 6785 / +6012-528 7212 E: groospacemy@gmail.com IG: @groospace.my		CLIENTS ACKNOWLEDGE & SIGN :	
PROJECT :	HANA RESIDENCE, TROPICANA AMAN	INTERIOR DESIGNER :	YANXIANG & YS	SALE PERSON :	RAYMOND	1ST DRAFT (R0)	09 OCT' 26				
						AMENDMENT 01					
						AMENDMENT 02					
						AMENDMENT 03					
CLIENT :	MS SHEON & MR TEE	CHECK BY :	RAYMOND		ID.02.06	AMENDMENT 04					
"NOTICE TO CONTRACTOR: DO NOT SCALE DRAWINGS. All dimensions and site levels must be Verified In Field (V.I.F.) before any fabrication or commencement of work. Any discrepancies between these drawings and actual site conditions must be reported to the Designer immediately for clarification. Failure to do so will be at the Contractor's own risk."											

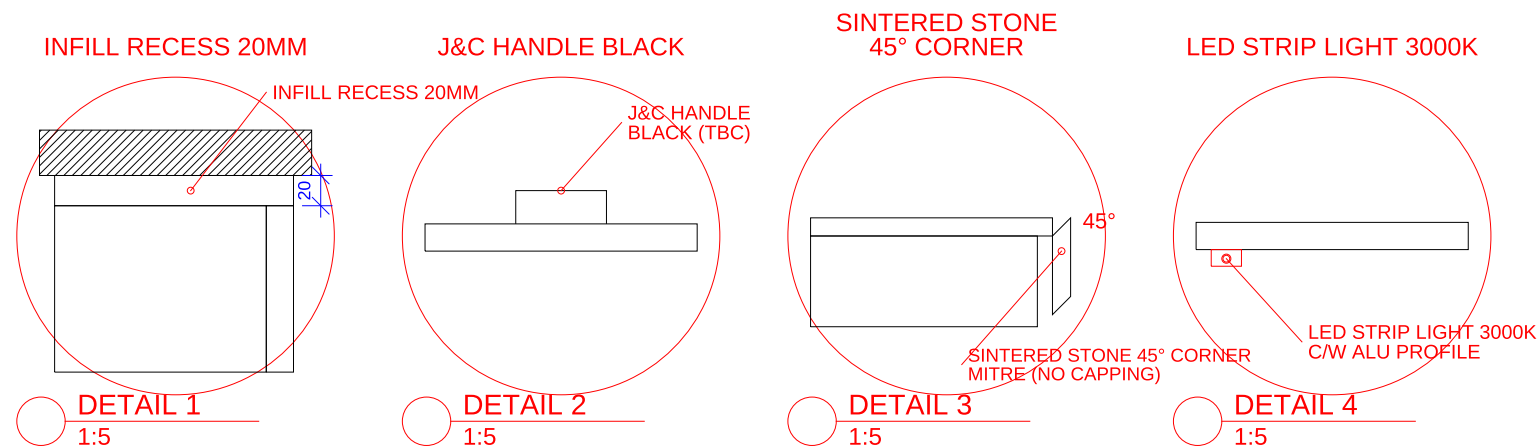

NOTES:

1. BACKSPLASH: LIMESTONE JH12352GZ 600x1200 STRUCTURED (T05).
2. HOB & HOOD BY OWNER - CUT-OUT TO MODEL SPEC.
3. LIFT-UP WALL CABINET C/W BLUM AVENTOS (TBC). UNDER-CABINET LED.


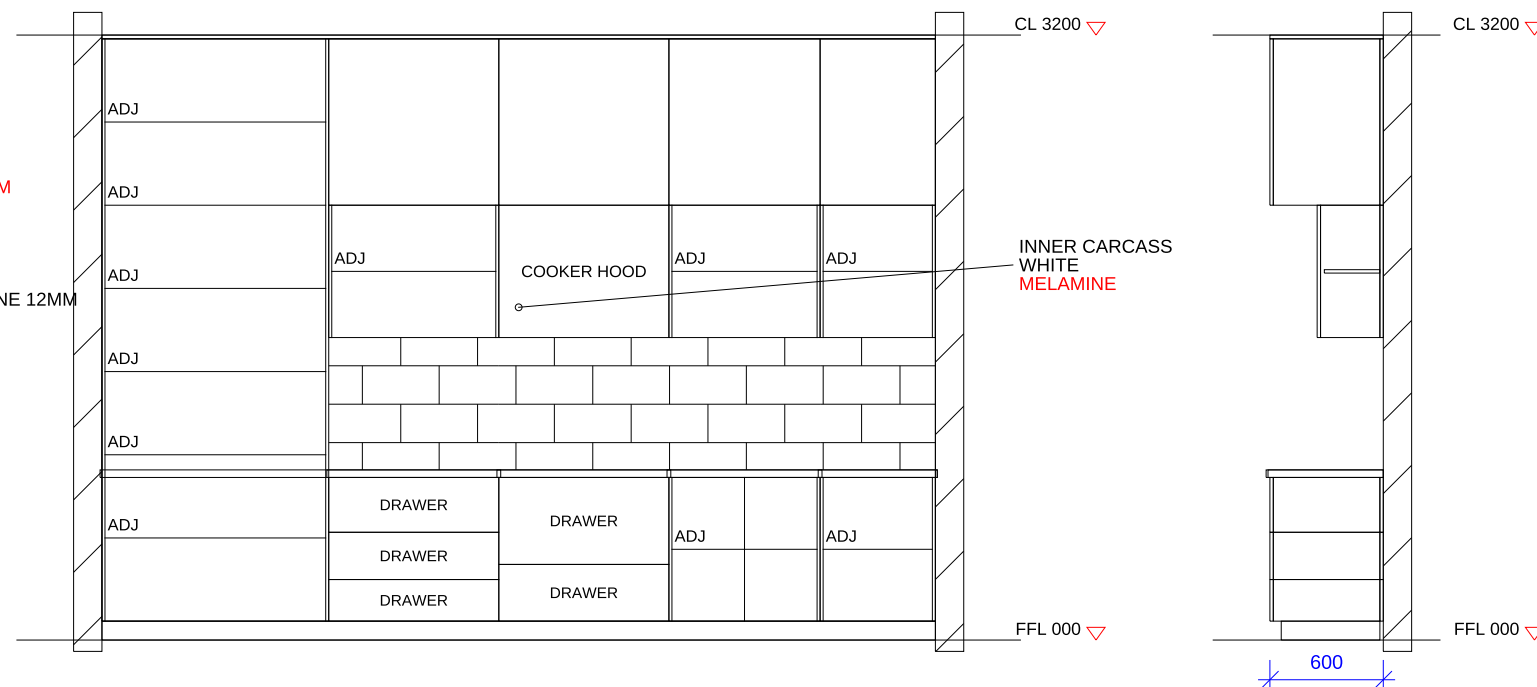


SECTION X-X
1:40




ELEVATION PLAN

PROJECT TYPE :		DESIGN & BUILD		DRAWING TITLE :		WET KITCHEN HOB WALL BASE & WALL CABINET ELEVATION		DRAWING'S STATUS :		ALL DRAWINGS ARE COPY-RIGHT OF:  GROO SPACE SDN BHD (1662567-V) LEVEL 3A, WISMA JAG, JALAN DESA UTAMA, TAMAN DESA, 58100 KUALA LUMPUR T: +6016-913 6785 / +6012-528 7212 E: groospacemy@gmail.com IG: @groospace.my		CLIENTS ACKNOWLEDGE & SIGN :			
						1ST DRAFT (R0)		09 OCT' 26							
PROJECT :		HANA RESIDENCE, TROPICANA AMAN		INTERIOR DESIGNER :		YANXIANG & YS		SALE PERSON :						RAYMOND	
CLIENT :		MS SHEON & MR TEE		CHECK BY :		RAYMOND		ID.02.07							

"NOTICE TO CONTRACTOR: DO NOT SCALE DRAWINGS. All dimensions and site levels must be Verified In Field (V.I.F.) before any fabrication or commencement of work. Any discrepancies between these drawings and actual site conditions must be reported to the Designer immediately for clarification. Failure to do so will be at the Contractor's own risk."

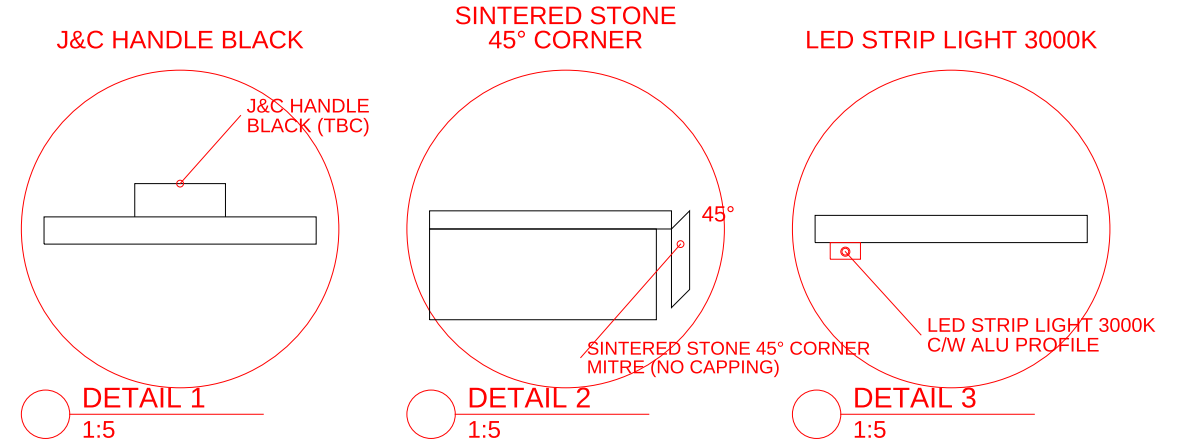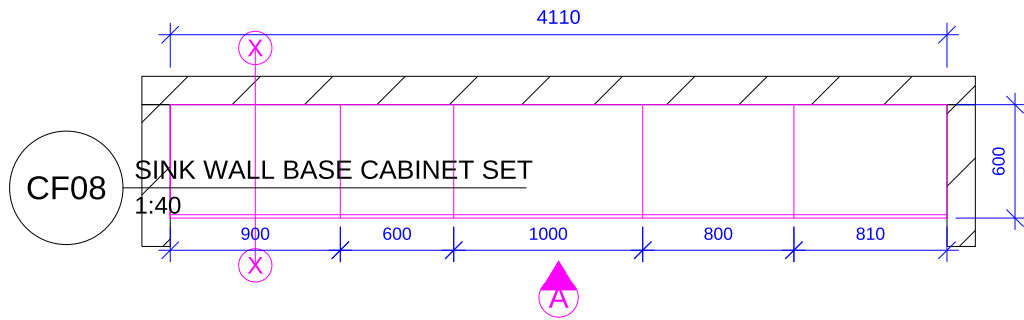

- NOTES:
- WINDOW W2400 FFL920 H450 (SITE MEASURE) - WALL CABINET STOPS AT WINDOW.
 - DISHWASHER BY OWNER (600 BUILT-IN).
 - UNDERMOUNT DOUBLE SINK + PULL-OUT TAP (BY OWNER).

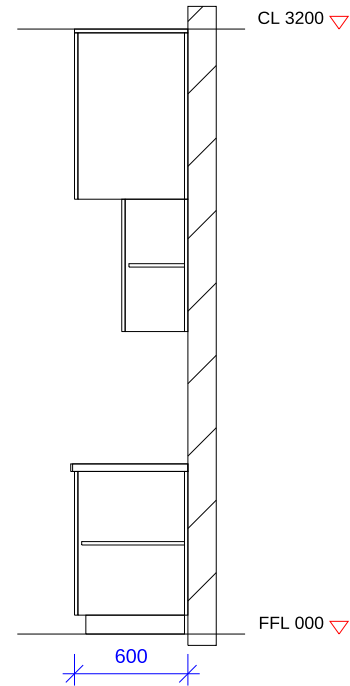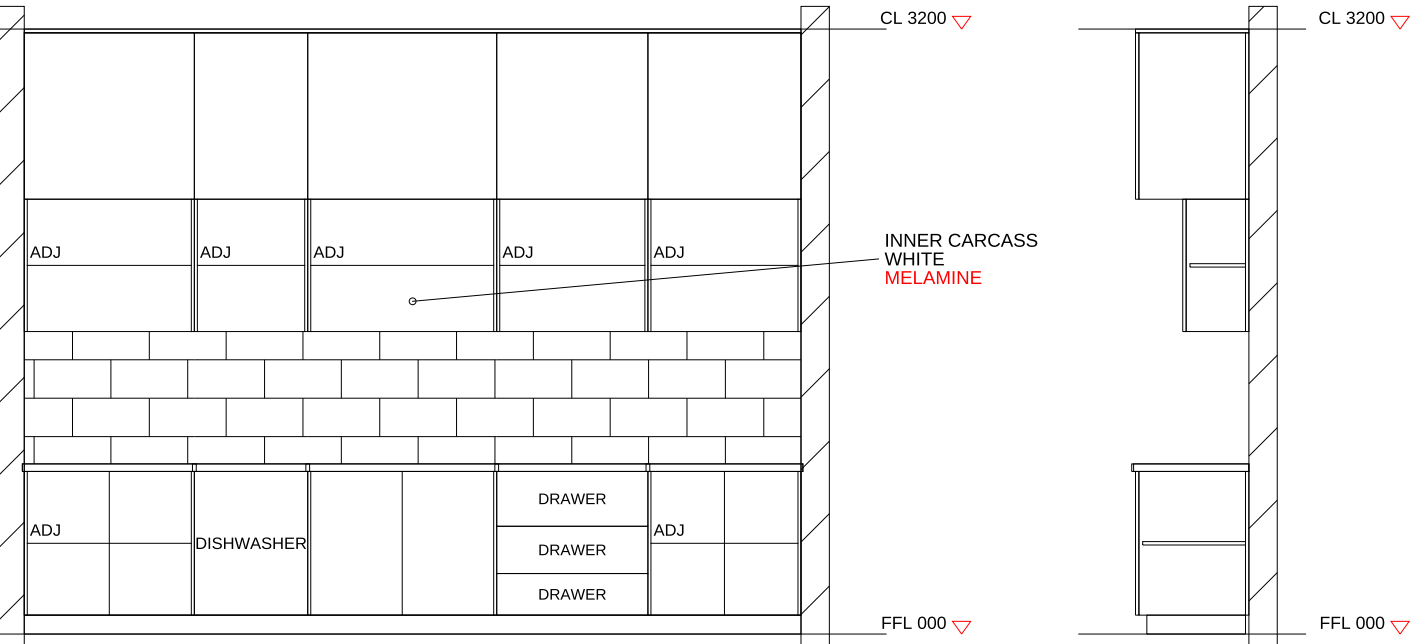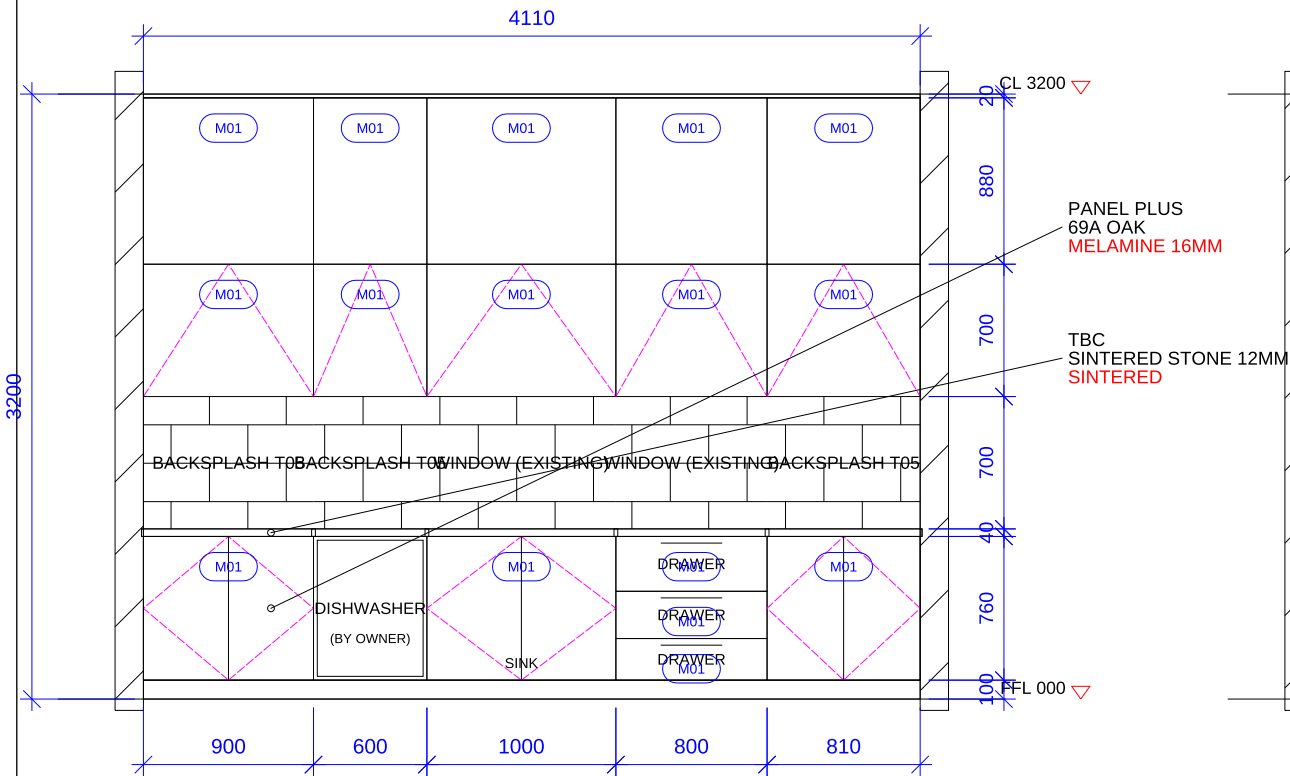

ELEVATION A
1:40

INNER CARCASS A
1:40

SECTION X-X
1:40



WET KITCHEN - SINK WALL BASE CABINET

ELEVATION PLAN




ID
02

PROJECT TYPE :	DESIGN & BUILD	DRAWING TITLE :	WET KITCHEN SINK WALL BASE CABINET ELEVATION	DRAWING'S STATUS :	1ST DRAFT (R0)	09 OCT' 26	ALL DRAWINGS ARE COPY-RIGHT OF:	CLIENTS ACKNOWLEDGE & SIGN :
PROJECT :	HANA RESIDENCE, TROPICANA AMAN	INTERIOR DESIGNER :	YANXIANG & YS	SALE PERSON :	RAYMOND		GROO SPACE SDN BHD (1662567-V)	
CLIENT :	MS SHEON & MR TEE	CHECK BY :	RAYMOND	ID.02.08			LEVEL 3A, WISMA JAG, JALAN DESA UTAMA, TAMAN DESA, 58100 KUALA LUMPUR	
							T: +6016-913 6785 / +6012-528 7212	
							E: groospacemy@gmail.com IG: @groospace.my	

"NOTICE TO CONTRACTOR: DO NOT SCALE DRAWINGS. All dimensions and site levels must be Verified In Field (V.I.F.) before any fabrication or commencement of work. Any discrepancies between these drawings and actual site conditions must be reported to the Designer immediately for clarification. Failure to do so will be at the Contractor's own risk."

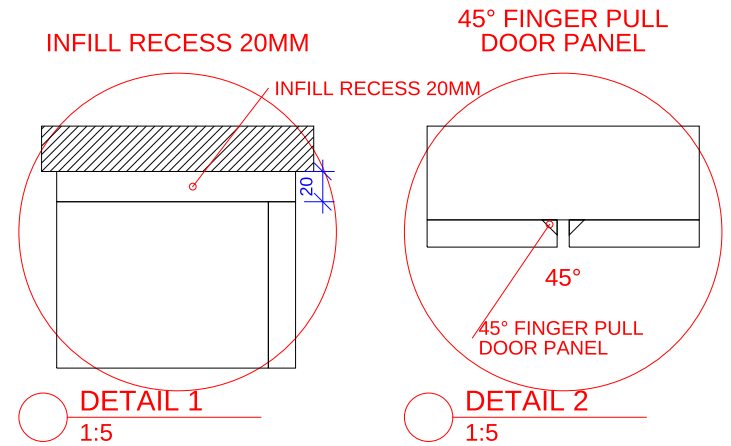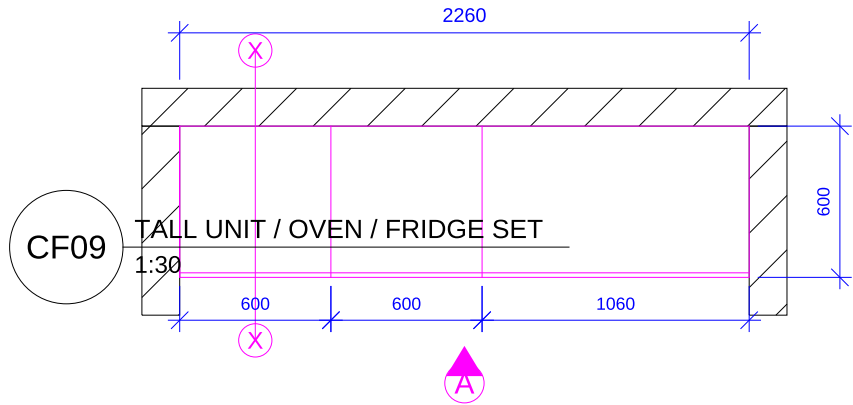

- NOTES:
- FRIDGE HOUSING: 30MM VENT GAP EACH SIDE & TOP, VENT GRILLE AT PLINTH.
 - OVEN / MICROWAVE MODEL TBC - CUT-OUT TO SPEC.

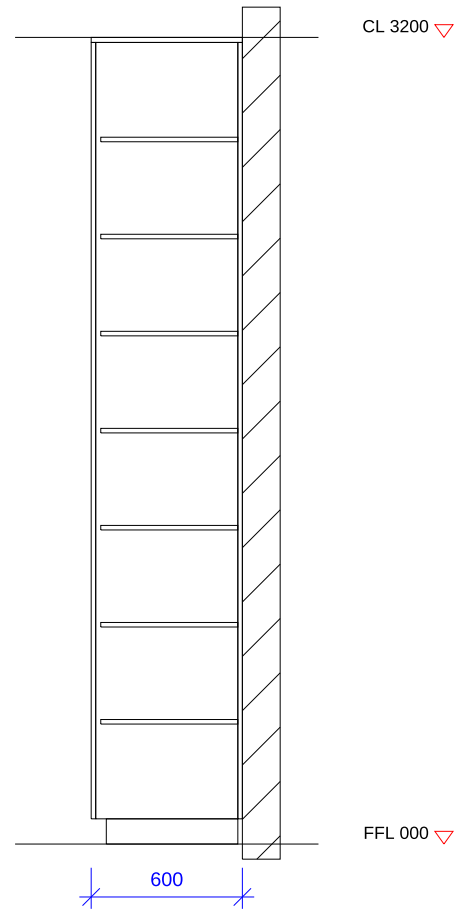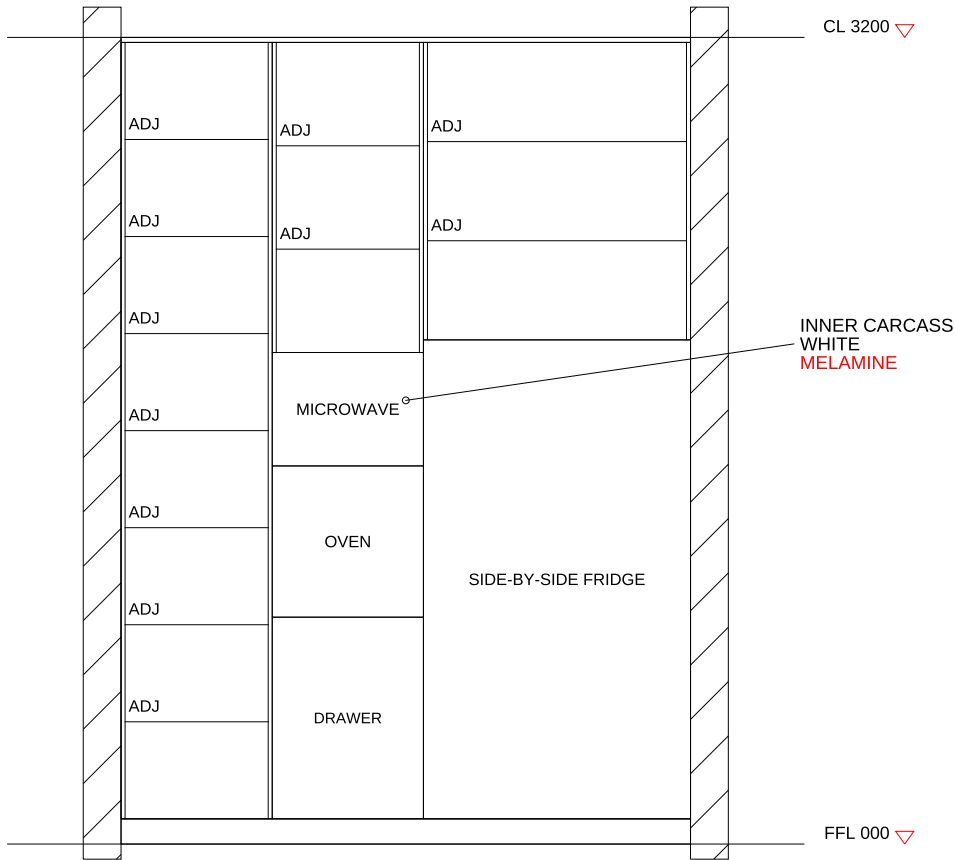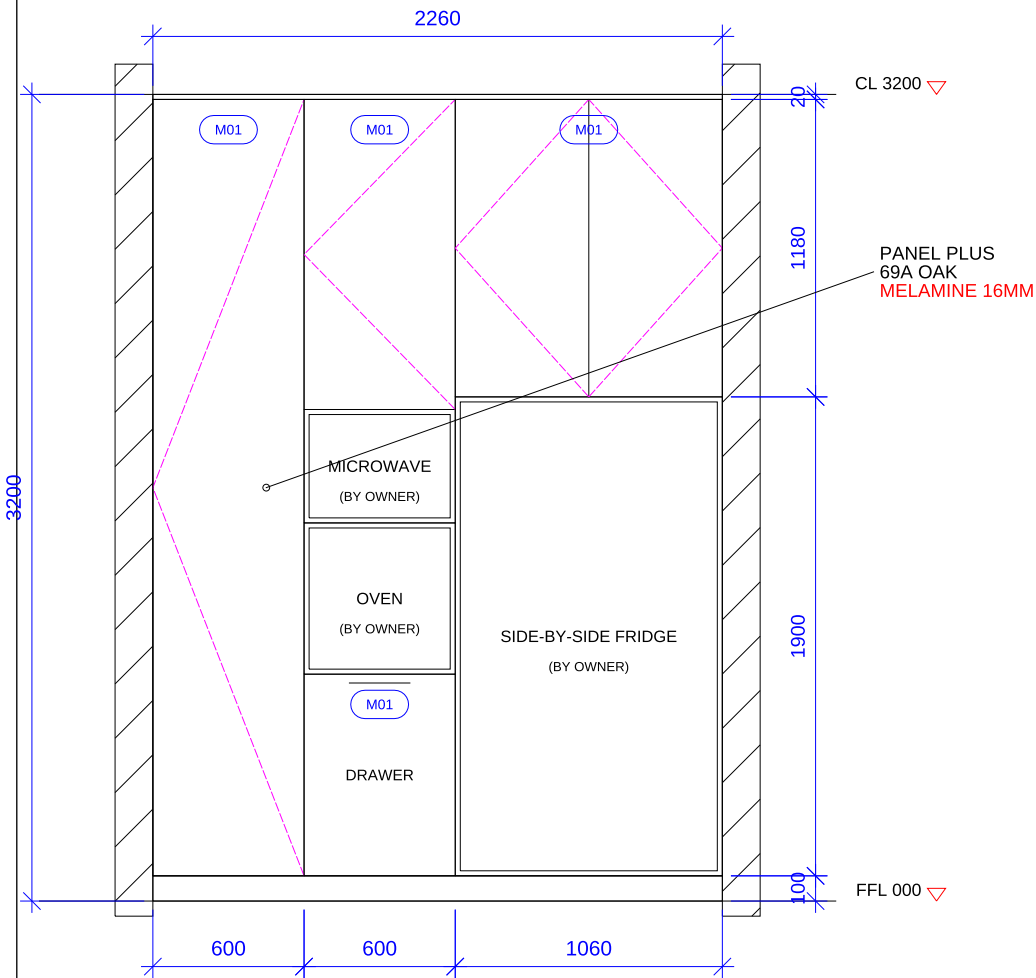

ELEVATION A
1:30

INNER CARCASS A
1:30

SECTION X-X
1:30


WET KITCHEN - TALL UNIT / OVEN / FRIDGE

ELEVATION PLAN


ID
02

PROJECT TYPE :	DESIGN & BUILD	DRAWING TITLE :	WET KITCHEN TALL UNIT / OVEN / FRIDGE ELEVATION	DRAWING'S STATUS :	1ST DRAFT (R0)	09 OCT' 26	ALL DRAWINGS ARE COPY-RIGHT OF:	CLIENTS ACKNOWLEDGE & SIGN :
PROJECT :	HANA RESIDENCE, TROPICANA AMAN	INTERIOR DESIGNER :	YANXIANG & YS	SALE PERSON :	RAYMOND		GROO SPACE SDN BHD (1662567-V)	
CLIENT :	MS SHEON & MR TEE	CHECK BY :	RAYMOND	ID.02.09			LEVEL 3A, WISMA JAG, JALAN DESA UTAMA, TAMAN DESA, 58100 KUALA LUMPUR	
							T: +6016-913 6785 / +6012-528 7212	
							E: groospacemy@gmail.com IG: @groospace.my	

"NOTICE TO CONTRACTOR: DO NOT SCALE DRAWINGS. All dimensions and site levels must be Verified In Field (V.I.F.) before any fabrication or commencement of work. Any discrepancies between these drawings and actual site conditions must be reported to the Designer immediately for clarification. Failure to do so will be at the Contractor's own risk."

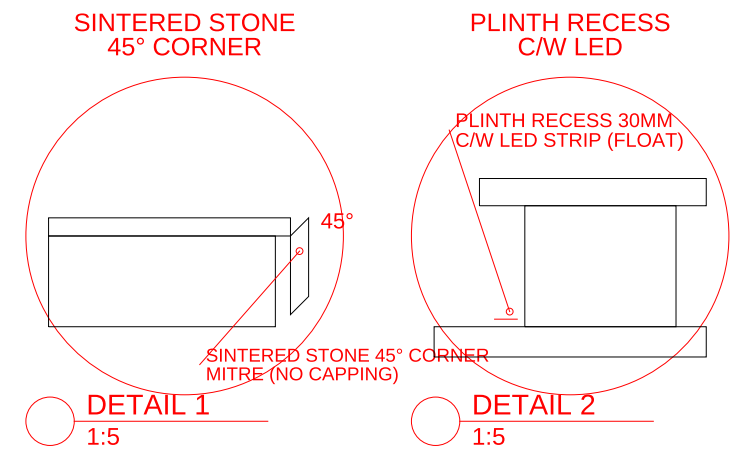



1. CURVED (SOFT TRIANGLE) ISLAND - SET OUT FROM PLAN TEMPLATE ON SITE.
2. BODY CLAD WITH TERRAZZO-LOOK SINTERED STONE.
3. TOP: SINTERED STONE 30MM, BULLNOSE EDGE.

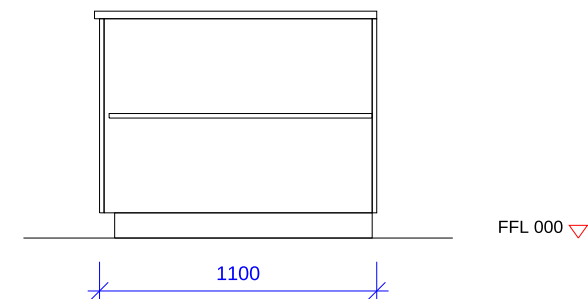




SECTION X-X
1:30

ELEVATION PLAN (C)

"NOTICE TO CONTRACTOR: DO NOT SCALE DRAWINGS. All dimensions and site levels must be Verified In Field (V.I.F.) before any fabrication or commencement of work. Any discrepancies between these drawings and actual site conditions must be reported to the Designer immediately for clarification. Failure to do so will be at the Contractor's own risk."

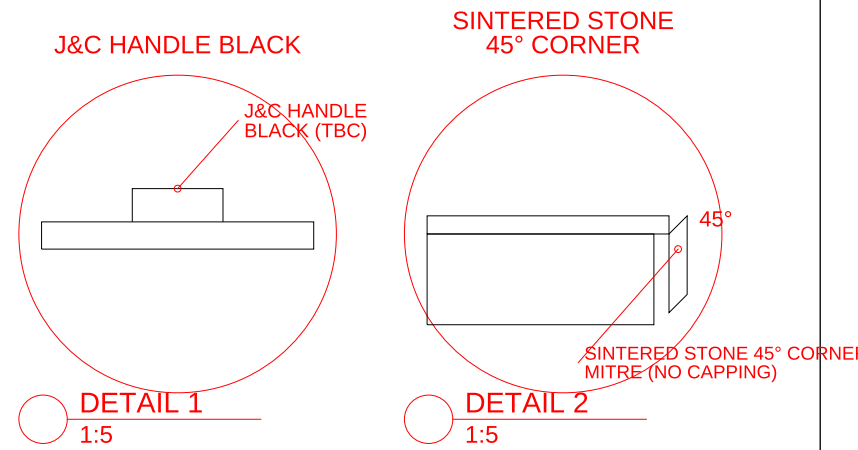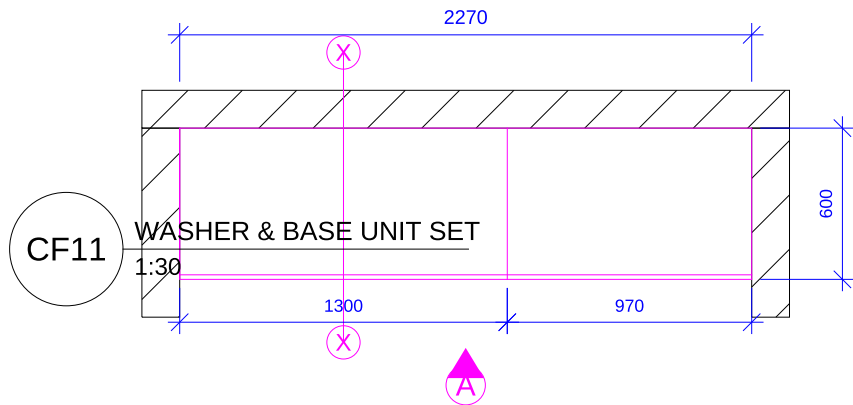

- NOTES:
1. WASHER & DRYER SIDE BY SIDE UNDER COUNTER (FRONT LOAD, BY OWNER).
 2. WINDOW W1500 H1450 ABOVE (SITE MEASURE).
 3. EAST WALL: BASE UNIT + CEILING HUNG BLACK HANGING ROD (REFER PLAN).

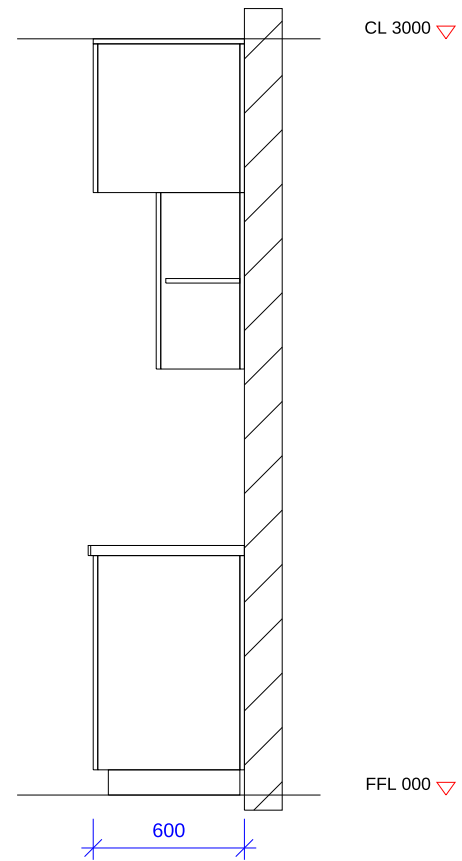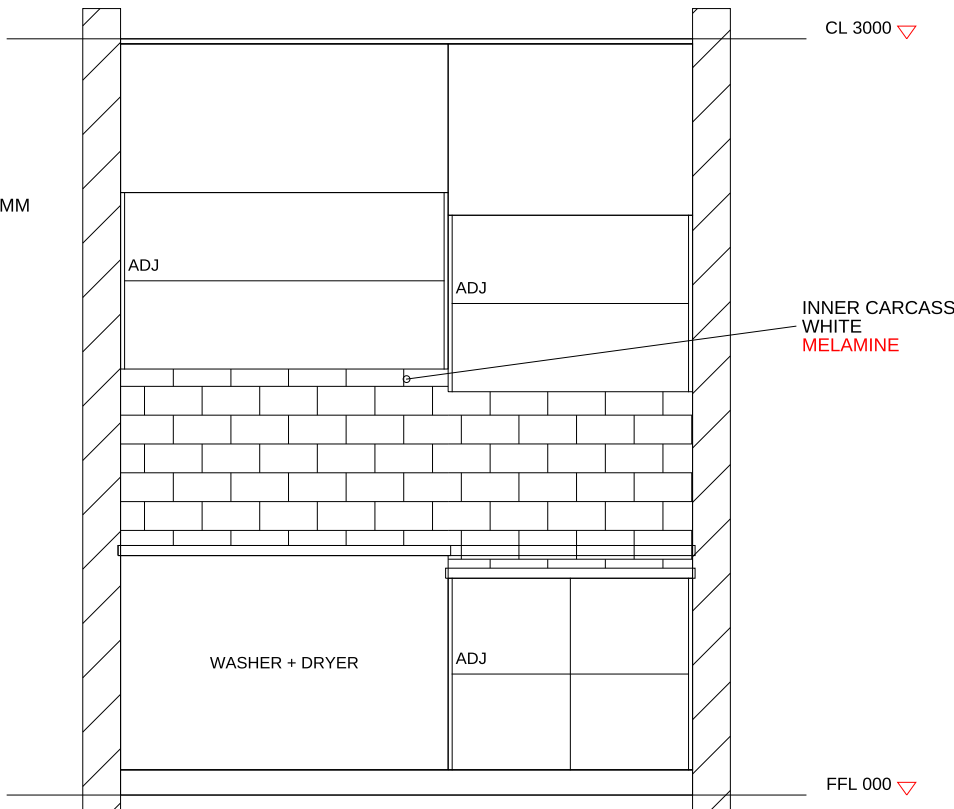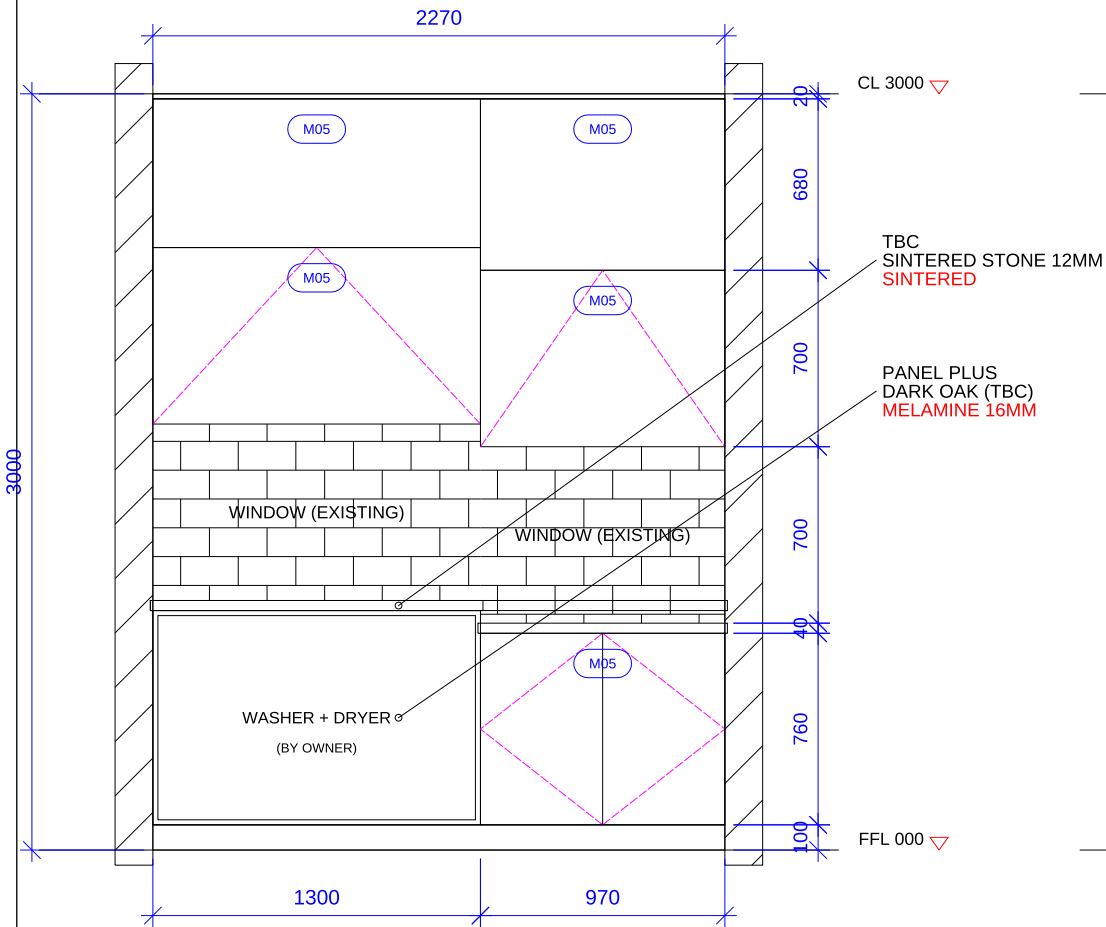


LAUNDRY AREA - WASHER & BASE UNIT

ELEVATION PLAN


ID
02

PROJECT TYPE :	DESIGN & BUILD	DRAWING TITLE :	LAUNDRY AREA WASHER & BASE UNIT ELEVATION	DRAWING'S STATUS :	1ST DRAFT (R0)	09 OCT' 26	ALL DRAWINGS ARE COPY-RIGHT OF:	CLIENTS ACKNOWLEDGE & SIGN :
PROJECT :	HANA RESIDENCE, TROPICANA AMAN	INTERIOR DESIGNER :	YANXIANG & YS	SALE PERSON :	RAYMOND		GROO SPACE SDN BHD (1662567-V)	
CLIENT :	MS SHEON & MR TEE	CHECK BY :	RAYMOND	ID.02.11			LEVEL 3A, WISMA JAG, JALAN DESA UTAMA, TAMAN DESA, 58100 KUALA LUMPUR	
							T: +6016-913 6785 / +6012-528 7212	
							E: groospacemy@gmail.com IG: @groospace.my	

"NOTICE TO CONTRACTOR: DO NOT SCALE DRAWINGS. All dimensions and site levels must be Verified In Field (V.I.F.) before any fabrication or commencement of work. Any discrepancies between these drawings and actual site conditions must be reported to the Designer immediately for clarification. Failure to do so will be at the Contractor's own risk."

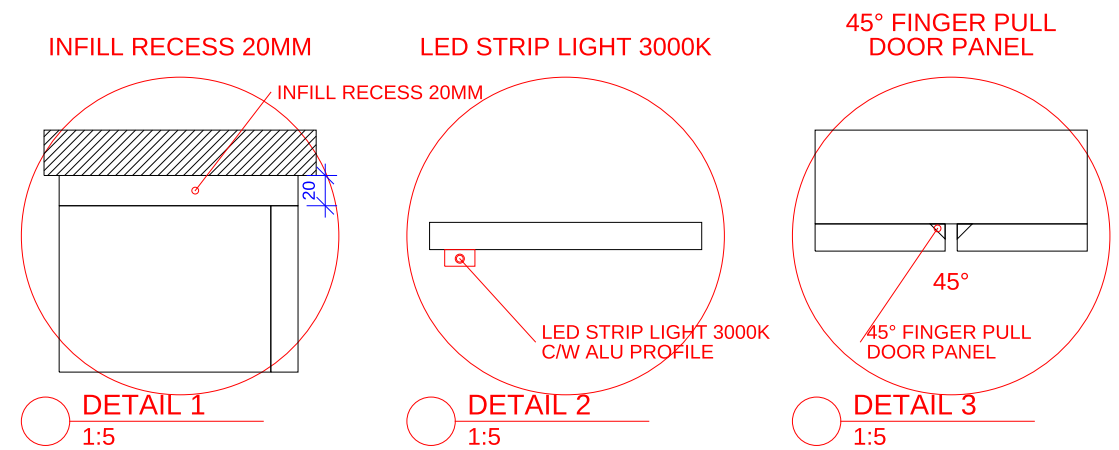

1. OPEN WARDROBE 1600 x 560 (SITE 2030 RECESS - V.I.F.).
2. LOW CABINET 2450 x 440 x 750H ON EAST WALL - CURVED END (REFER 3D).


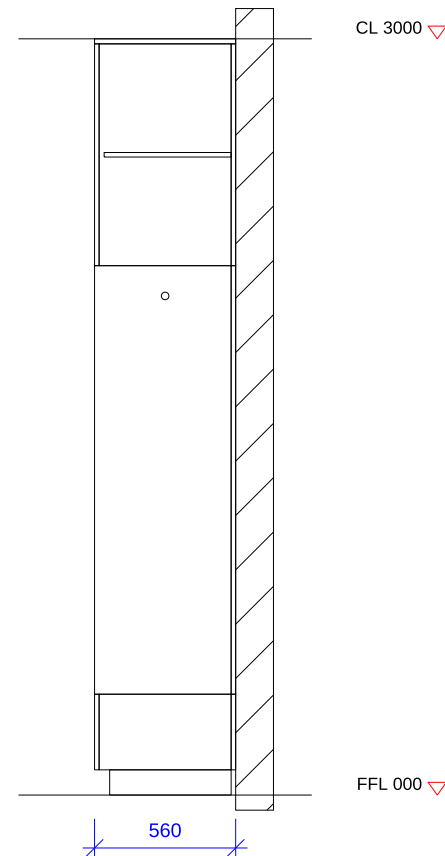


SECTION X-X
1:30




ELEVATION PLAN (0)

PROJECT TYPE :	DESIGN & BUILD	DRAWING TITLE :	PARENT'S ROOM OPEN WARDROBE ELEVATION		DRAWING'S STATUS :		ALL DRAWINGS ARE COPY-RIGHT OF:  GROO SPACE SDN BHD (1662567-V) LEVEL 3A, WISMA JAG, JALAN DESA UTAMA, TAMAN DESA, 58100 KUALA LUMPUR T: +6016-913 6785 / +6012-528 7212 E: groospacemy@gmail.com IG: @groospace.my	CLIENTS ACKNOWLEDGE & SIGN :
PROJECT :	HANA RESIDENCE, TROPICANA AMAN	INTERIOR DESIGNER :	YANXIANG & YS	SALE PERSON :	RAYMOND	1ST DRAFT (R0) 09 OCT' 26 AMENDMENT 01 AMENDMENT 02		
CLIENT :	MS SHEON & MR TEE	CHECK BY :	RAYMOND		ID.02.12	AMENDMENT 03 AMENDMENT 04		

"NOTICE TO CONTRACTOR: DO NOT SCALE DRAWINGS. All dimensions and site levels must be Verified In Field (V.I.F.) before any fabrication or commencement of work. Any discrepancies between these drawings and actual site conditions must be reported to the Designer immediately for clarification. Failure to do so will be at the Contractor's own risk."

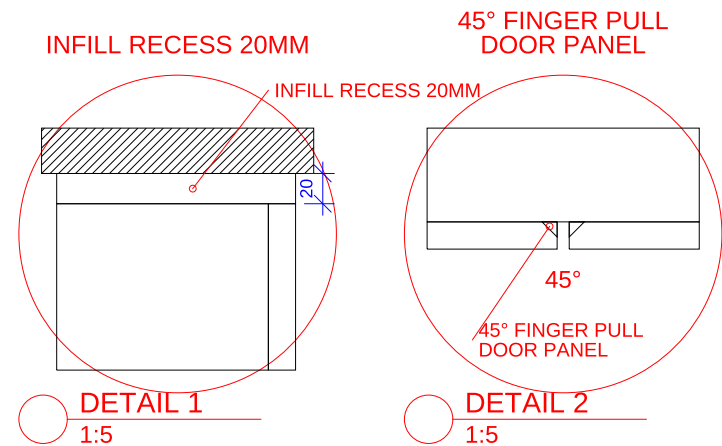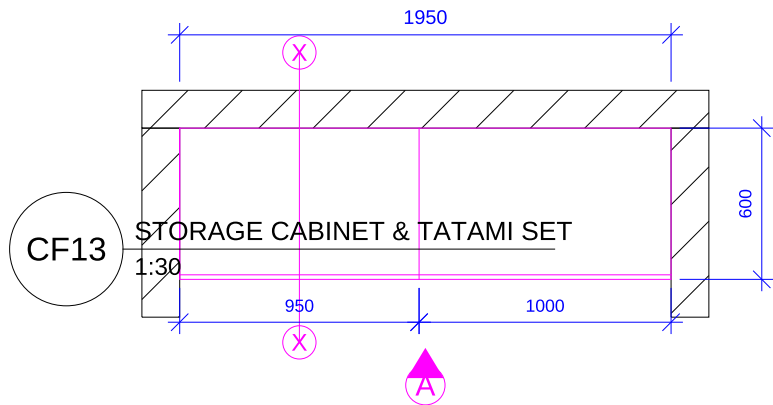

- NOTES:
- 1. TATAMI 1160 x 2100 x 400H C/W LIFT-UP STORAGE (GAS STRUT).
 - 2. HEADBOARD SHELF C/W LED (REFER 3D).

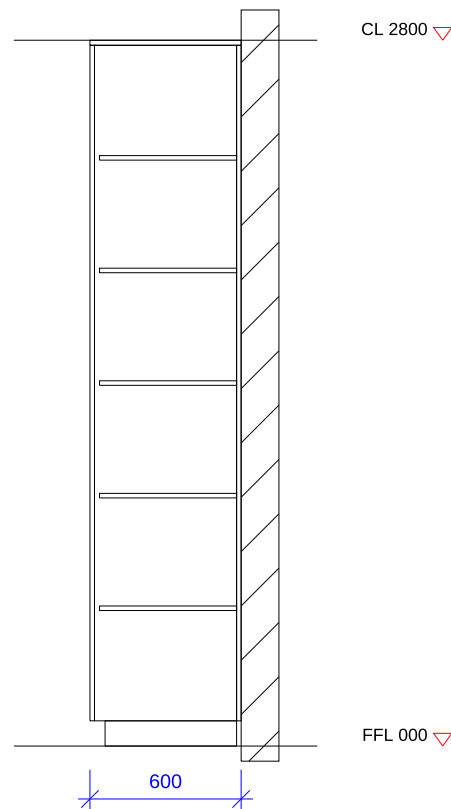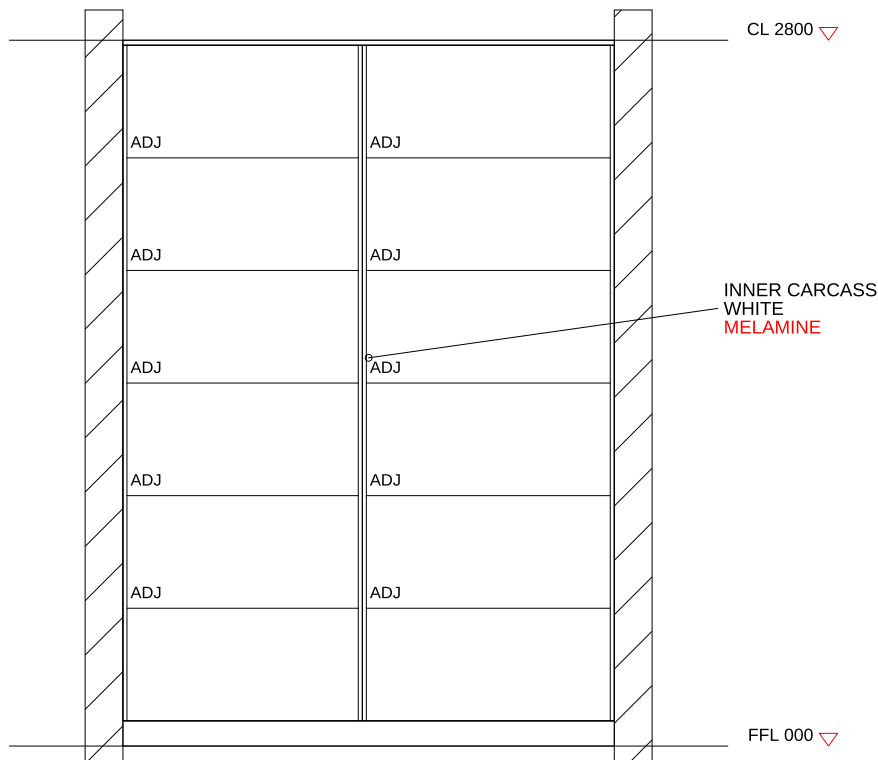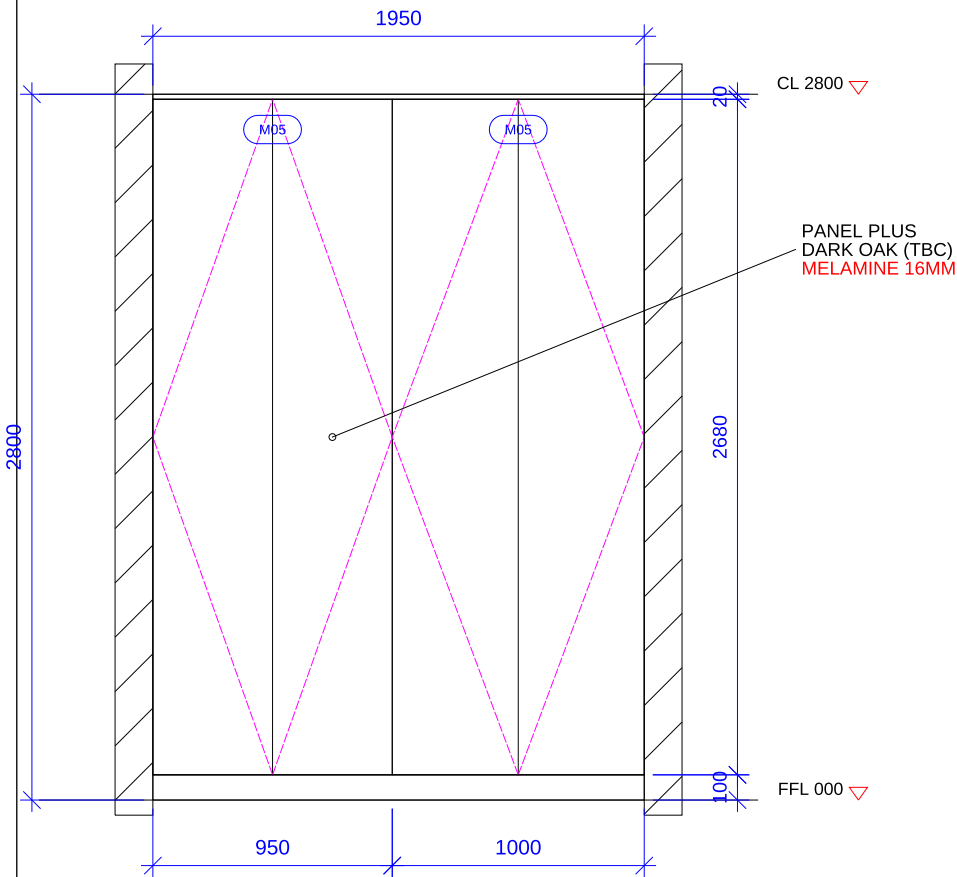


MAID ROOM - STORAGE CABINET & TATAMI

ELEVATION PLAN


ID
02

PROJECT TYPE :		DESIGN & BUILD		DRAWING TITLE :		MAID ROOM STORAGE CABINET & TATAMI ELEVATION		DRAWING'S STATUS :		ALL DRAWINGS ARE COPY-RIGHT OF:		CLIENTS ACKNOWLEDGE & SIGN :	
PROJECT :		HANA RESIDENCE, TROPICANA AMAN		INTERIOR DESIGNER :		YANXIANG & YS		SALE PERSON :		RAYMOND			groospace GROO SPACE SDN BHD (1662567-V) LEVEL 3A, WISMA JAG, JALAN DESA UTAMA, TAMAN DESA, 58100 KUALA LUMPUR T: +6016-913 6785 / +6012-528 7212 E: groospacemy@gmail.com IG: @groospace.my
CLIENT :		MS SHEON & MR TEE		CHECK BY :		RAYMOND		ID.02.13		09 OCT' 26			

"NOTICE TO CONTRACTOR: DO NOT SCALE DRAWINGS. All dimensions and site levels must be Verified In Field (V.I.F.) before any fabrication or commencement of work. Any discrepancies between these drawings and actual site conditions must be reported to the Designer immediately for clarification. Failure to do so will be at the Contractor's own risk."

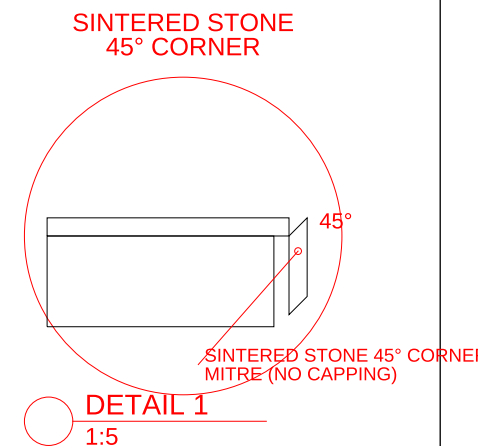

1. PEDESTAL STONE BASIN (BY OWNER) - REFER 3D.
2. WALL & FLOOR: AMAZON TRAVERTINE 600x1200 MATT (T04).

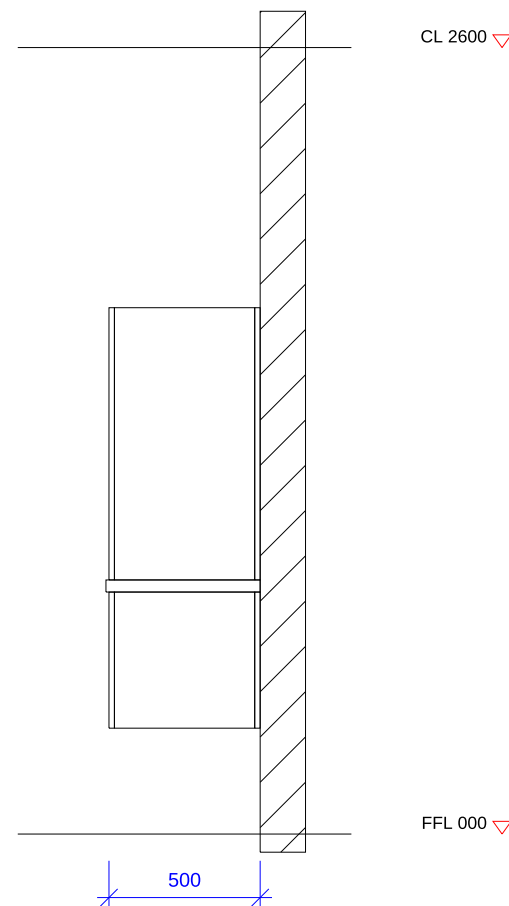

SECTION X-X
1:25


POWDER ROOM - VANITY

ELEVATION PLAN


ID

02

"NOTICE TO CONTRACTOR: DO NOT SCALE DRAWINGS. All dimensions and site levels must be Verified In Field (V.I.F.) before any fabrication or commencement of work. Any discrepancies between these drawings and actual site conditions must be reported to the Designer immediately for clarification. Failure to do so will be at the Contractor's own risk."

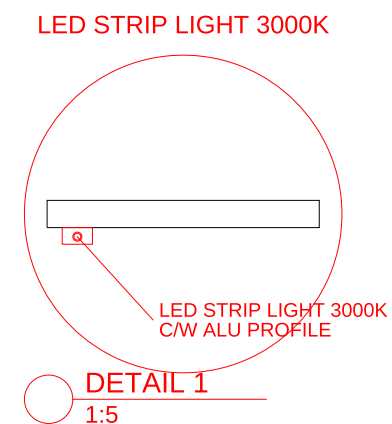



1. FLOATING BEDSIDE DRAWER C/W UNDER-LED.
2. WALL PANEL REVEAL 3MM BLACK GROOVE (REFER 3D).

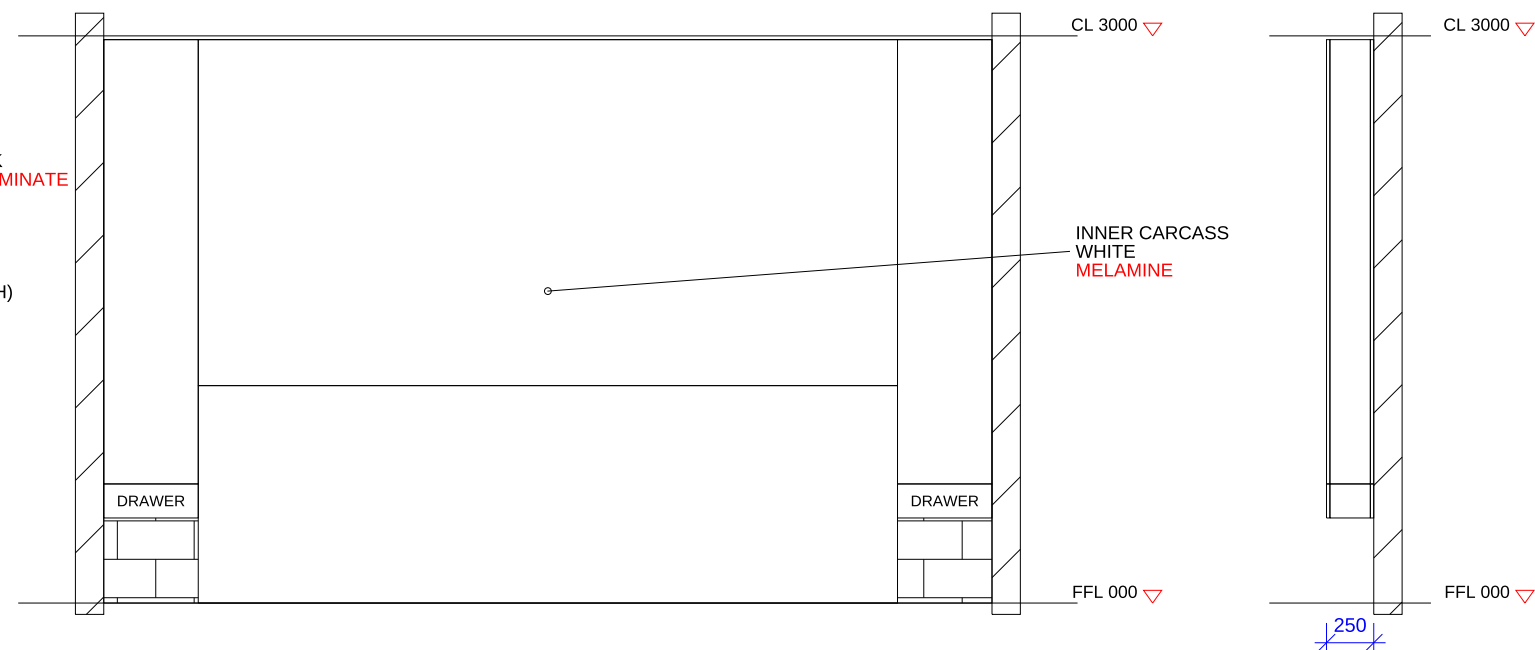



SECTION X-X
1:40

ELEVATION PLAN

"NOTICE TO CONTRACTOR: DO NOT SCALE DRAWINGS. All dimensions and site levels must be Verified In Field (V.I.F.) before any fabrication or commencement of work. Any discrepancies between these drawings and actual site conditions must be reported to the Designer immediately for clarification. Failure to do so will be at the Contractor's own risk."

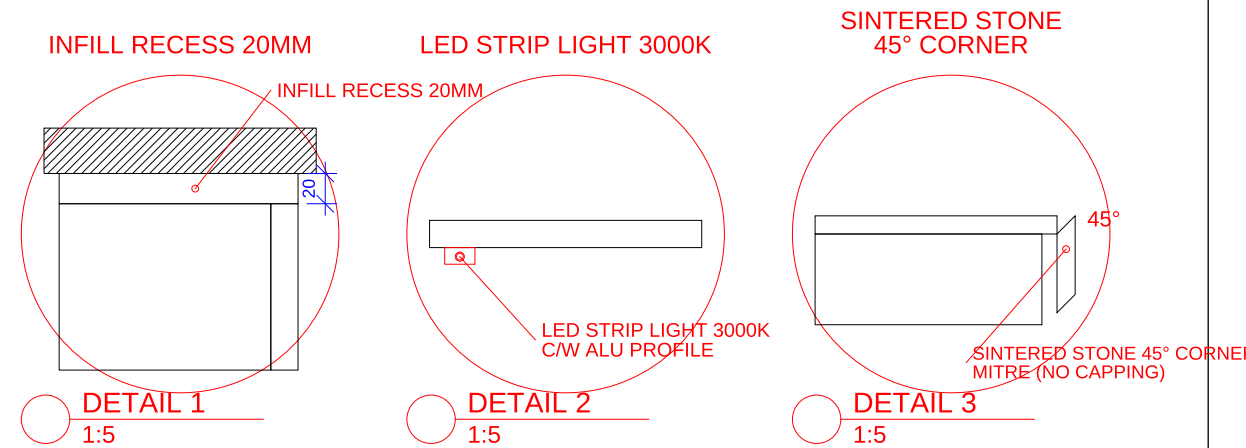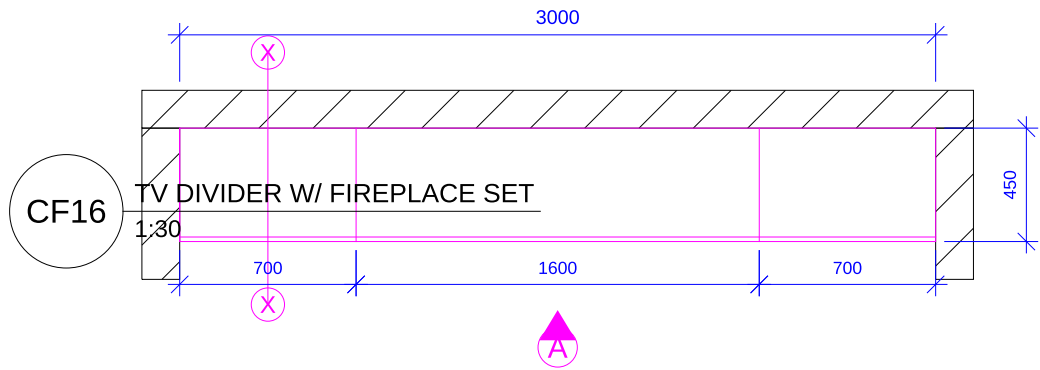

- NOTES:
- FIREPLACE SUPPLIED BY OWNER - NON-COMBUSTIBLE LINING (SINTERED STONE) AROUND FIREBOX.
 - OPT 2: TWIN TIMBER COLUMNS EITHER SIDE (REFER 3D).

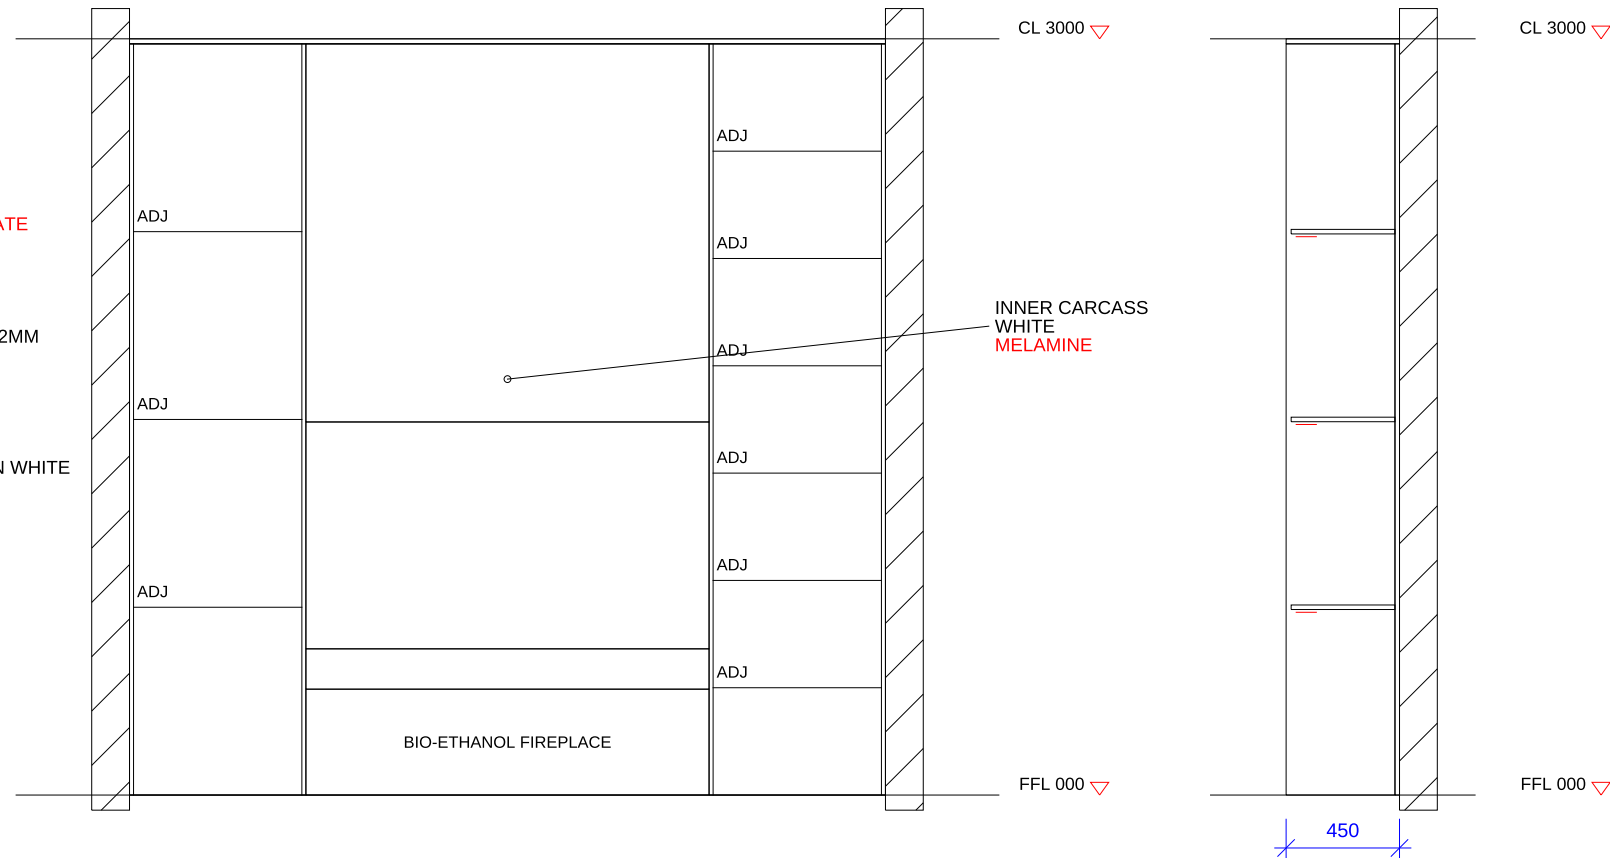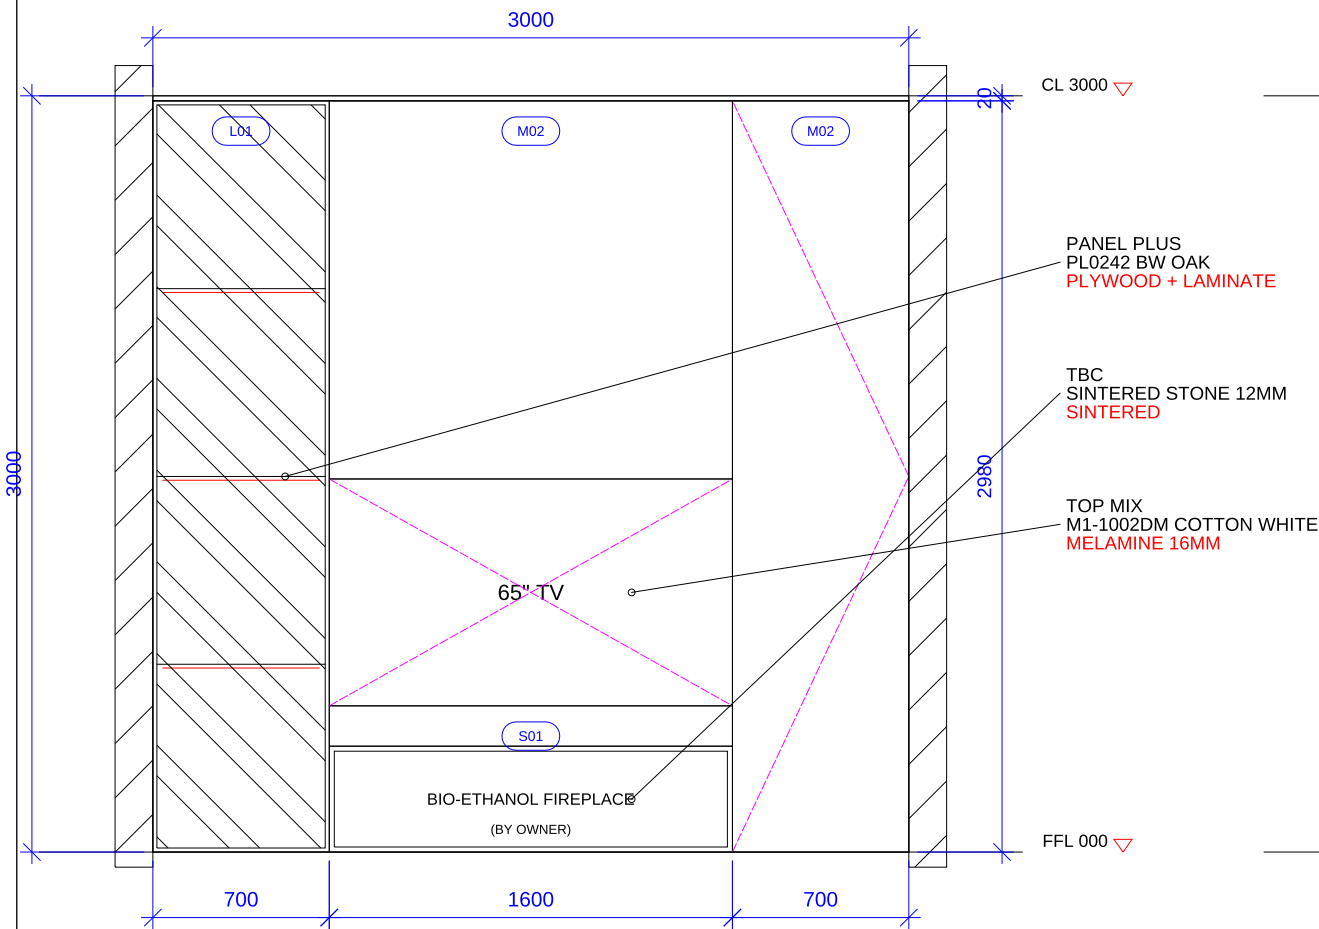

SECTION X-X
1:30


MASTER BEDROOM - TV DIVIDER W/ FIREPLACE

ELEVATION PLAN

ID
03


PROJECT TYPE :	DESIGN & BUILD	DRAWING TITLE :	MASTER BEDROOM TV DIVIDER W/ FIREPLACE ELEVATION	DRAWING'S STATUS :	1ST DRAFT (R0)	09 OCT' 26	ALL DRAWINGS ARE COPY-RIGHT OF:	CLIENTS ACKNOWLEDGE & SIGN :
PROJECT :	HANA RESIDENCE, TROPICANA AMAN	INTERIOR DESIGNER :	YANXIANG & YS	SALE PERSON :	RAYMOND		GROO SPACE SDN BHD (1662567-V) LEVEL 3A, WISMA JAG, JALAN DESA UTAMA, TAMAN DESA, 58100 KUALA LUMPUR T: +6016-913 6785 / +6012-528 7212 E: groospacemy@gmail.com IG: @groospace.my	
CLIENT :	MS SHEON & MR TEE	CHECK BY :	RAYMOND	ID.03.02				

"NOTICE TO CONTRACTOR: DO NOT SCALE DRAWINGS. All dimensions and site levels must be Verified In Field (V.I.F.) before any fabrication or commencement of work. Any discrepancies between these drawings and actual site conditions must be reported to the Designer immediately for clarification. Failure to do so will be at the Contractor's own risk."

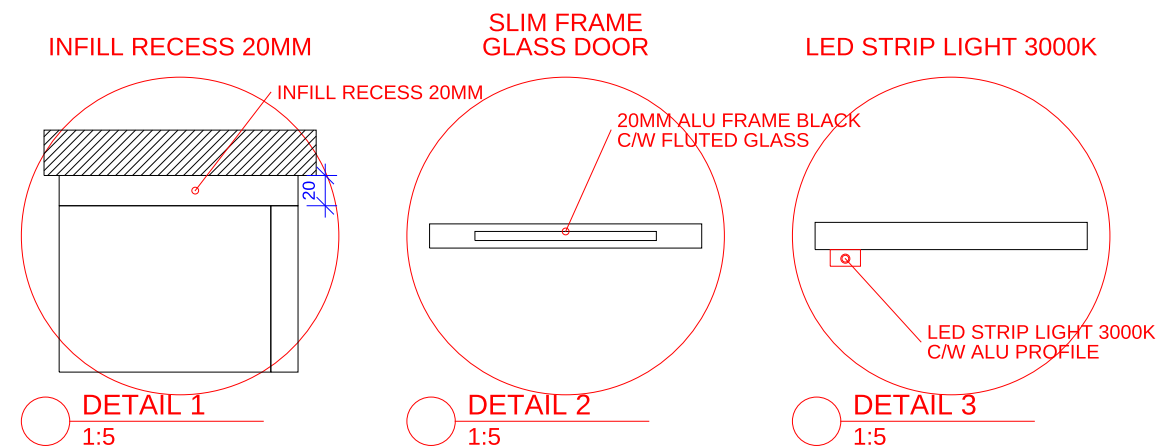

NOTES:

1. 20MM BLACK ALU FRAME C/W TINTED / FLUTED GLASS DOOR.
2. LED PROFILE AT EACH SHELF, DOOR-ACTIVATED SENSOR.

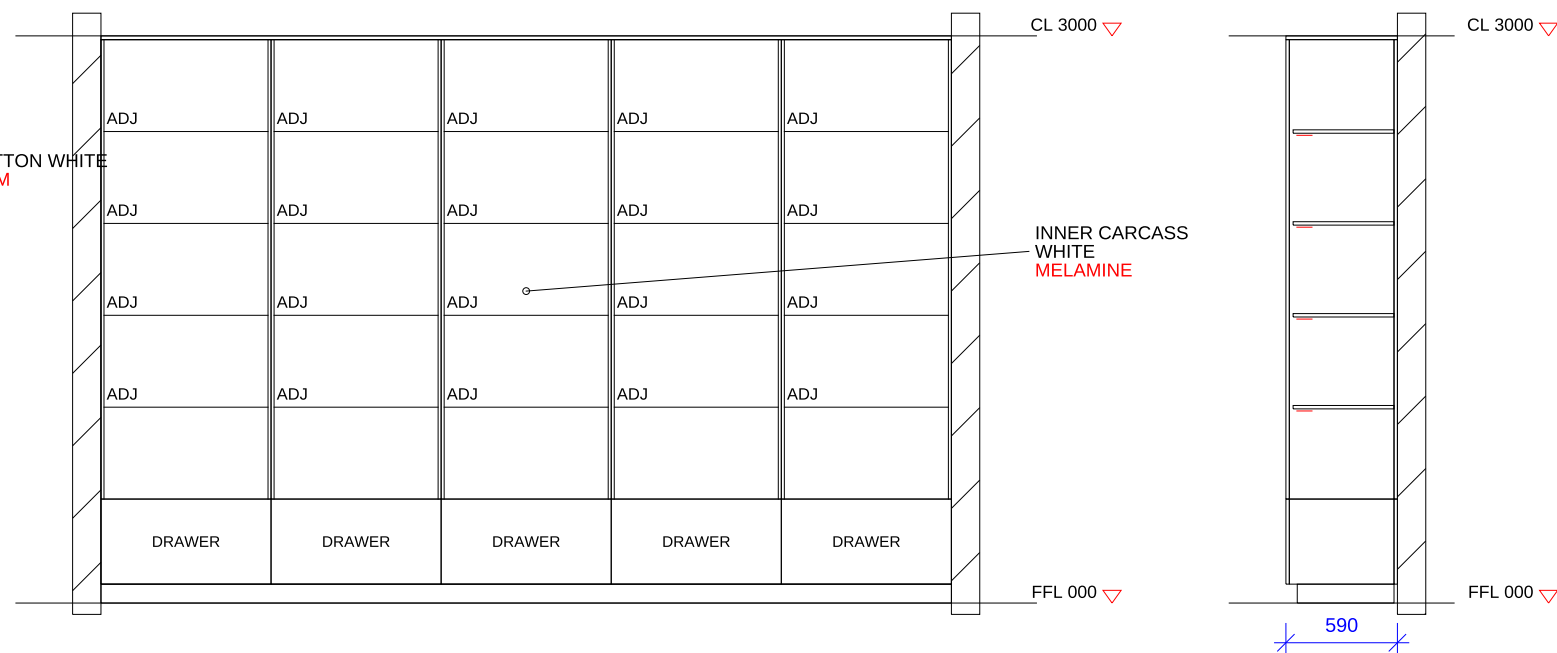


SECTION X-X
1:40

ELEVATION PLAN


PROJECT TYPE :		DESIGN & BUILD		DRAWING TITLE : WALK IN CLOSET WARDROBE (GLASS DOOR) ELEVATION		DRAWING'S STATUS : 1ST DRAFT (R0) 09 OCT' 26		ALL DRAWINGS ARE COPY-RIGHT OF: GROO SPACE SDN BHD (1662567-V) LEVEL 3A, WISMA JAG, JALAN DESA UTAMA, TAMAN DESA, 58100 KUALA LUMPUR T: +6016-913 6785 / +6012-528 7212 E: groospacemy@gmail.com IG: @groospace.my	CLIENTS ACKNOWLEDGE & SIGN :
PROJECT :		HANA RESIDENCE, TROPICANA AMAN		INTERIOR DESIGNER : YANXIANG & YS	SALE PERSON : RAYMOND	AMENDMENT 01			
CLIENT :		MS SHEON & MR TEE		CHECK BY : RAYMOND	ID.03.03	AMENDMENT 02			
						AMENDMENT 03			
						AMENDMENT 04			

"NOTICE TO CONTRACTOR: DO NOT SCALE DRAWINGS. All dimensions and site levels must be Verified In Field (V.I.F.) before any fabrication or commencement of work. Any discrepancies between these drawings and actual site conditions must be reported to the Designer immediately for clarification. Failure to do so will be at the Contractor's own risk."

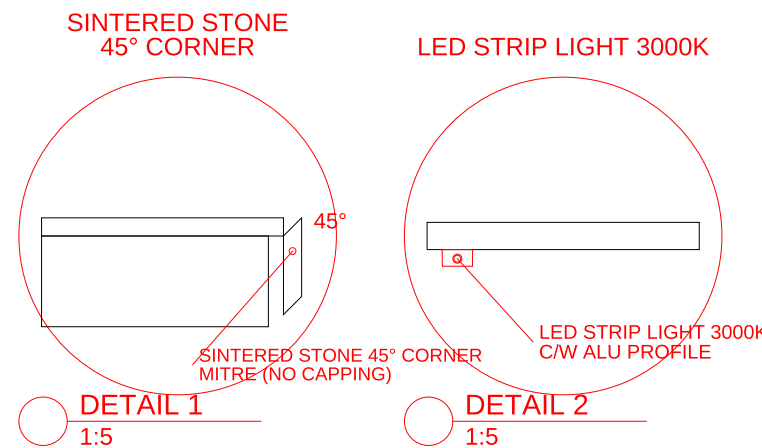

NOTES:

1. FLOATING VANITY C/W UNDER-CABINET LED.
2. MARBLE-LOOK SINTERED STONE TOP C/W 2 x COUNTERTOP BASIN (BY OWNER).

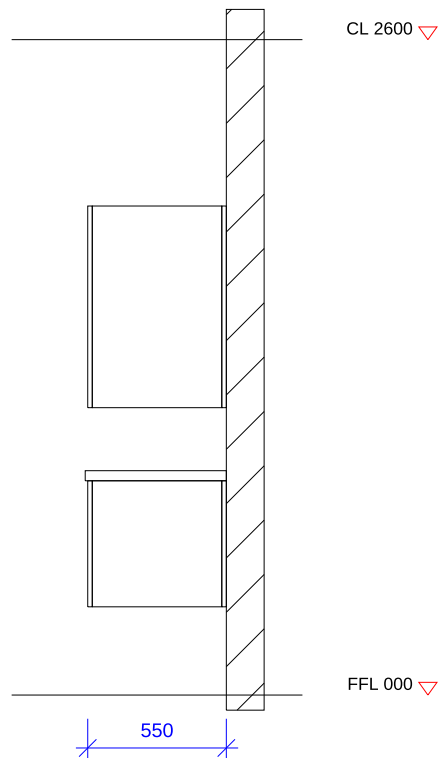


SECTION X-X
1:30

ELEVATION PLAN

PROJECT TYPE :		DESIGN & BUILD		DRAWING TITLE :		MASTER BATH DOUBLE VANITY ELEVATION		DRAWING'S STATUS :		ALL DRAWINGS ARE COPY-RIGHT OF: GROO SPACE SDN BHD (1662567-V) LEVEL 3A, WISMA JAG, JALAN DESA UTAMA, TAMAN DESA, 58100 KUALA LUMPUR T: +6016-913 6785 / +6012-528 7212 E: groospacemy@gmail.com IG: @groospace.my groospace		CLIENTS ACKNOWLEDGE & SIGN :			
PROJECT :		HANA RESIDENCE, TROPICANA AMAN		INTERIOR DESIGNER : YANXIANG & YS		SALE PERSON : RAYMOND		1ST DRAFT (R0)						09 OCT' 26	
								AMENDMENT 01							
								AMENDMENT 02							
								AMENDMENT 03							
CLIENT :		MS SHEON & MR TEE		CHECK BY :		RAYMOND		ID.03.04				AMENDMENT 04			

NOTICE TO CONTRACTOR: DO NOT SCALE DRAWINGS. All dimensions and site levels must be Verified In Field (V.I.F.) before any fabrication or commencement of work. Any discrepancies between these drawings and actual site conditions must be reported to the Designer immediately for clarification. Failure to do so will be at the Contractor's own risk.

"NOTICE TO CONTRACTOR: DO NOT SCALE DRAWINGS. All dimensions and site levels must be Verified In Field (V.I.F.) before any fabrication or commencement of work. Any discrepancies between these drawings and actual site conditions must be reported to the Designer immediately for clarification. Failure to do so will be at the Contractor's own risk."

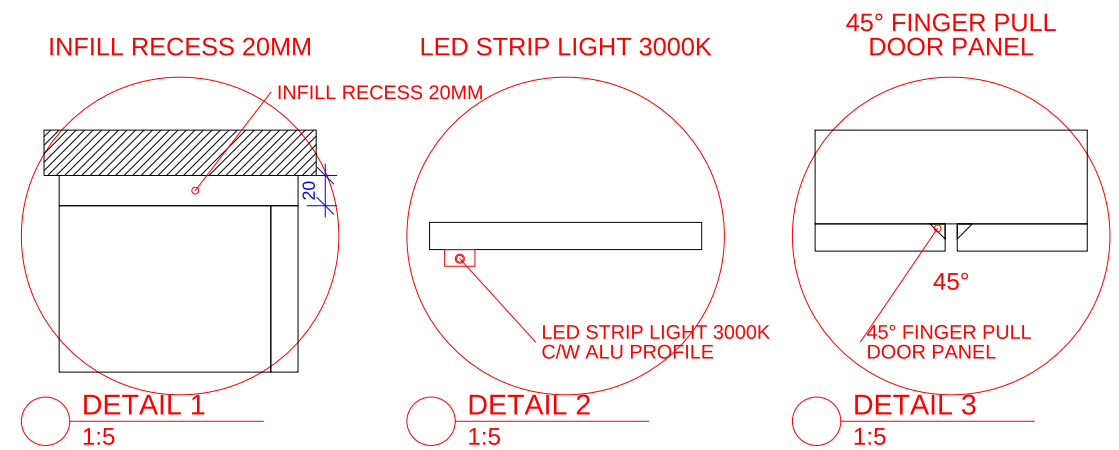

1. DARK FINISH TS4-1017 M BLACK (L02) C/W WARM DISPLAY BACK PANEL.
2. STUDY DESK C/W WALL-HUNG DISPLAY - REFER PLAN.





 ELEVATION A
1:30



ELEVATION PLAN

PROJECT TYPE :		DESIGN & BUILD		DRAWING TITLE : SON'S ROOM WARDROBE & DISPLAY ELEVATION		DRAWING'S STATUS : 1ST DRAFT (R0) 09 OCT' 26		ALL DRAWINGS ARE COPY-RIGHT OF: groospace GROO SPACE SDN BHD (1662567-V) LEVEL 3A, WISMA JAG, JALAN DESA UTAMA, TAMAN DESA, 58100 KUALA LUMPUR T: +6016-913 6785 / +6012-528 7212 E: groospacemy@gmail.com IG: @groospace.my	CLIENTS ACKNOWLEDGE & SIGN :
PROJECT :		HANA RESIDENCE, TROPICANA AMAN		INTERIOR DESIGNER :	YANXIANG & YS	SALE PERSON :	RAYMOND		
CLIENT :		MS SHEON & MR TEE		CHECK BY :	RAYMOND		ID.03.06		

"NOTICE TO CONTRACTOR: DO NOT SCALE DRAWINGS. All dimensions and site levels must be Verified In Field (V.I.F.) before any fabrication or commencement of work. Any discrepancies between these drawings and actual site conditions must be reported to the Designer immediately for clarification. Failure to do so will be at the Contractor's own risk."

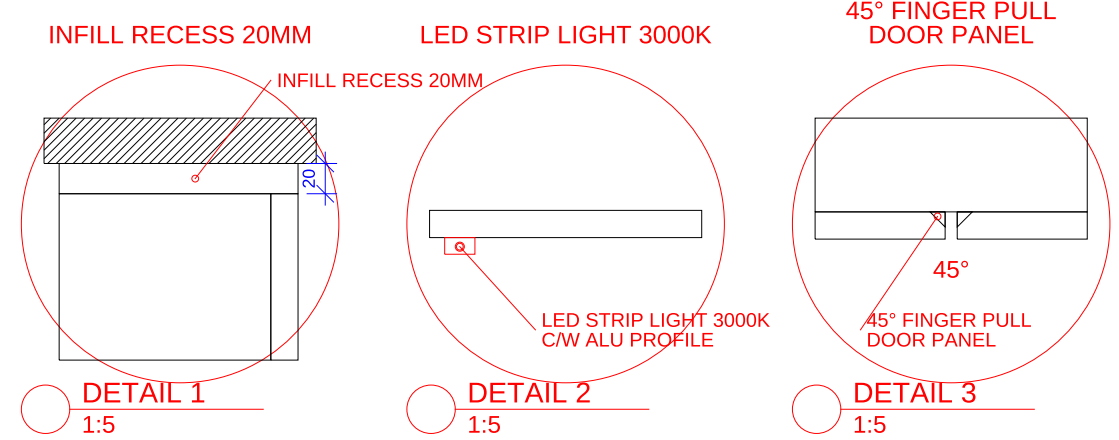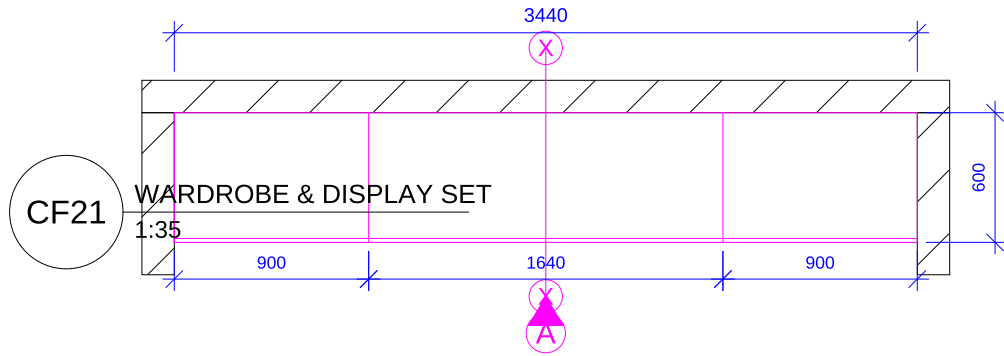

- NOTES:
- OAK FRAME C/W WHITE DOOR PANEL (REFER 3D).
 - DRESSING / STUDY DESK AT WINDOW - REFER PLAN.

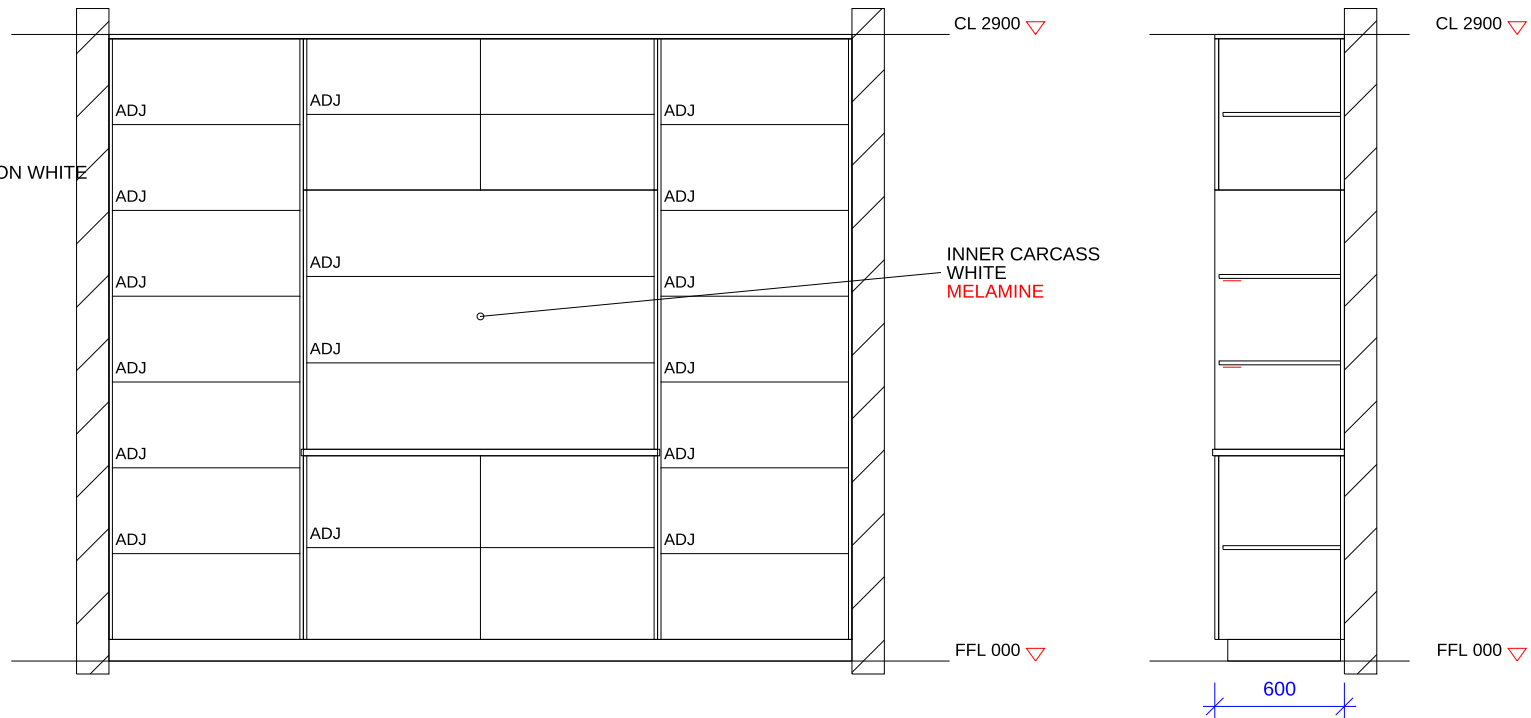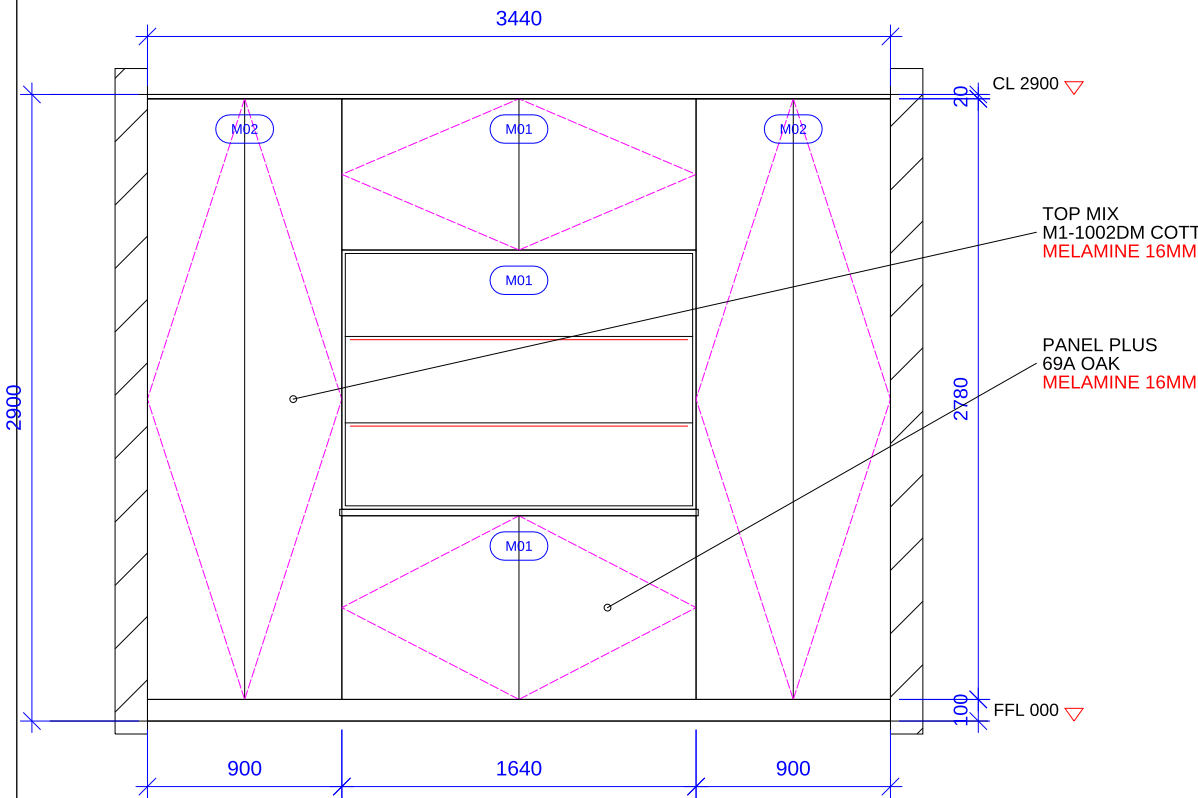


SECTION X-X
1:35

DAUGHTER'S ROOM - WARDROBE & DISPLAY
ELEVATION PLAN

ID
03


PROJECT TYPE :	DESIGN & BUILD	DRAWING TITLE :	DAUGHTER'S ROOM WARDROBE & DISPLAY ELEVATION	DRAWING'S STATUS :	1ST DRAFT (R0)	09 OCT '26	ALL DRAWINGS ARE COPY-RIGHT OF:	CLIENTS ACKNOWLEDGE & SIGN :
PROJECT :	HANA RESIDENCE, TROPICANA AMAN	INTERIOR DESIGNER :	YANXIANG & YS	SALE PERSON :	RAYMOND		GROO SPACE SDN BHD (1662567-V)	
CLIENT :	MS SHEON & MR TEE	CHECK BY :	RAYMOND	ID.03.07			LEVEL 3A, WISMA JAG, JALAN DESA UTAMA, TAMAN DESA, 58100 KUALA LUMPUR	
"NOTICE TO CONTRACTOR: DO NOT SCALE DRAWINGS. All dimensions and site levels must be Verified In Field (V.I.F.) before any fabrication or commencement of work. Any discrepancies between these drawings and actual site conditions must be reported to the Designer immediately for clarification. Failure to do so will be at the Contractor's own risk."							T: +6016-913 6785 / +6012-528 7212	
							E: groospacemy@gmail.com IG: @groospace.my	

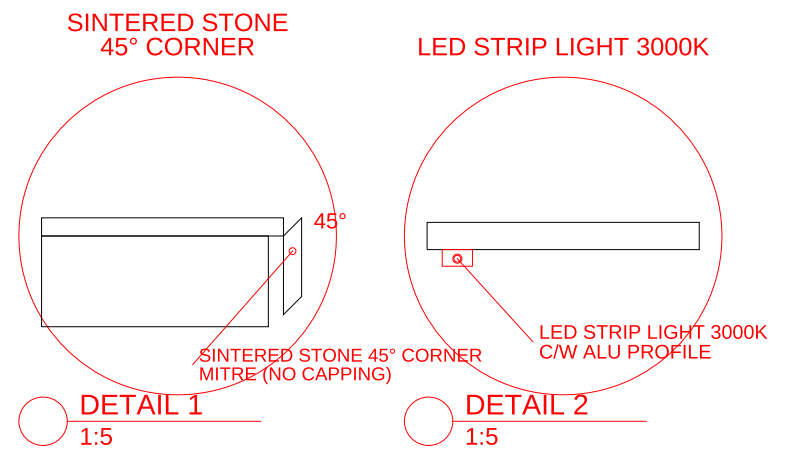

SON'S / DAUGHTER'S BATH - VANITY

ELEVATION PLAN

ID 03

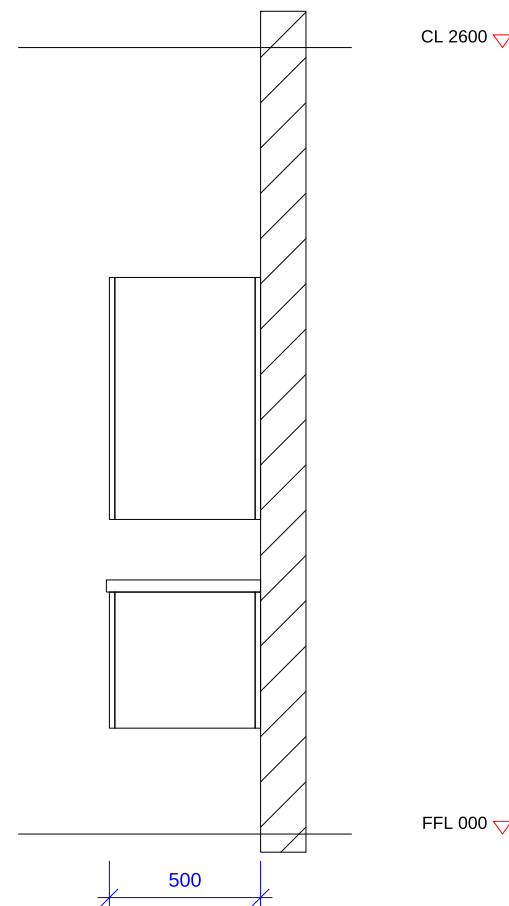

SECTION X-X
1:25

PROJECT TYPE :		DESIGN & BUILD		DRAWING TITLE :		SON'S / DAUGHTER'S BATH VANITY ELEVATION		DRAWING'S STATUS :		ALL DRAWINGS ARE COPY-RIGHT OF:		CLIENTS ACKNOWLEDGE & SIGN :	
PROJECT :		HANA RESIDENCE, TROPICANA AMAN		INTERIOR DESIGNER :		YANXIANG & YS		SALE PERSON :		RAYMOND		RAYMOND	
CLIENT :		MS SHEON & MR TEE		CHECK BY :		RAYMOND		ID.03.08		groospace		groospace	
"NOTICE TO CONTRACTOR: DO NOT SCALE DRAWINGS. All dimensions and site levels must be Verified In Field (V.I.F.) before any fabrication or commencement of work. Any discrepancies between these drawings and actual site conditions must be reported to the Designer immediately for clarification. Failure to do so will be at the Contractor's own risk."													